


Согласовано



Инв. № подл.	Подп. и дата	Взам. инв. №


						155-05-21 -			
						г. Кемерово			
Изм.	Кол.уч	Лист	№ док.	Подпись	Дата	Каркасный дом	Стадия	Лист	Листов
							П	001	
Чертил	Мухина ЕА					Стадия АР	30Ж		
Проверил									
Норм. контр.									

Экспликация помещений на отм.
0.000
1 : 100

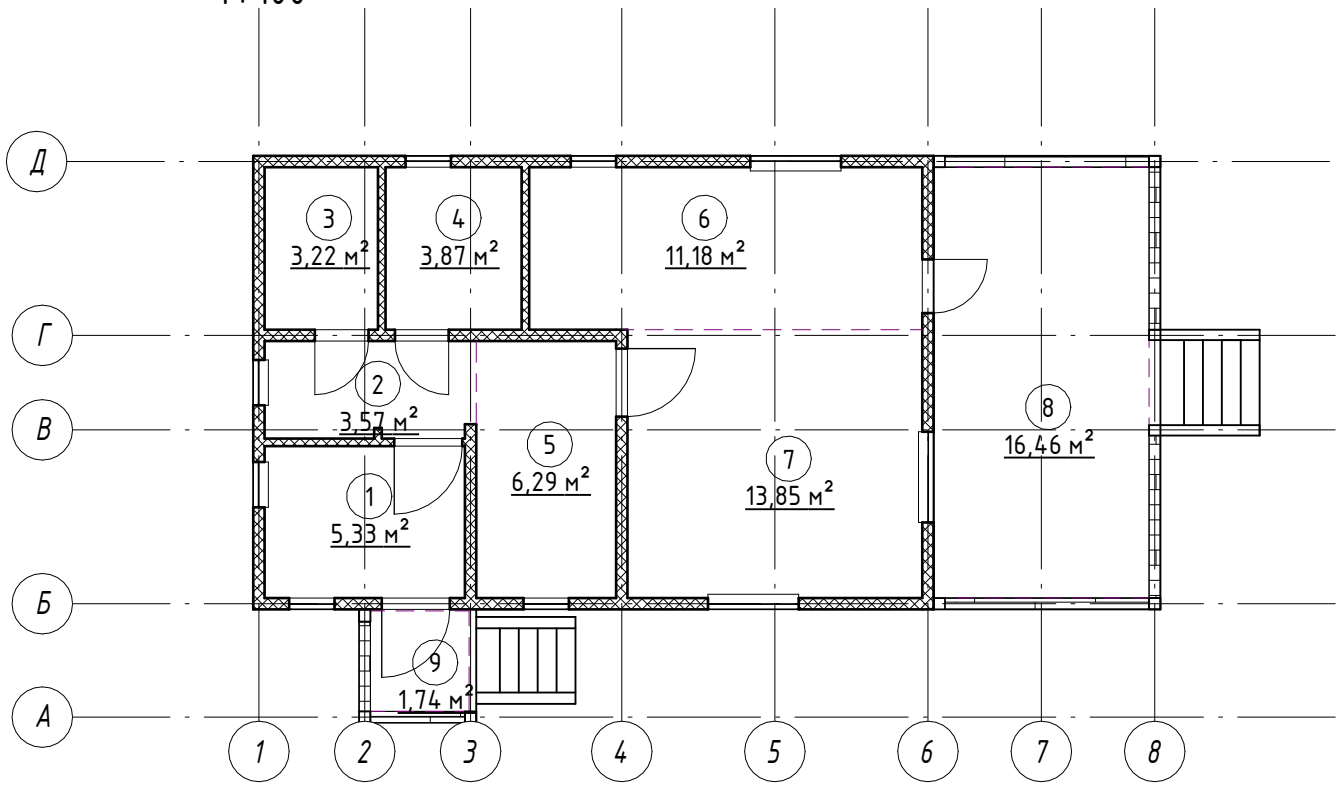

Экспликация помещений 1 этаж		
№ пом	Наименование	Площадь, м²
1	Тамбур	5,33 м²
2	Прихожая	3,57 м²
3	Тех.комната	3,22 м²
4	Сан.узел	3,87 м²
5	Лестница	6,29 м²
6	Кухня	11,18 м²
7	Зал	13,85 м²
8	Терраса	16,46 м²
9	Крыльцо	1,74 м²
Общий итог: 9		65,50 м²

Экспликация помещений на
отм.+2.850
1 : 100

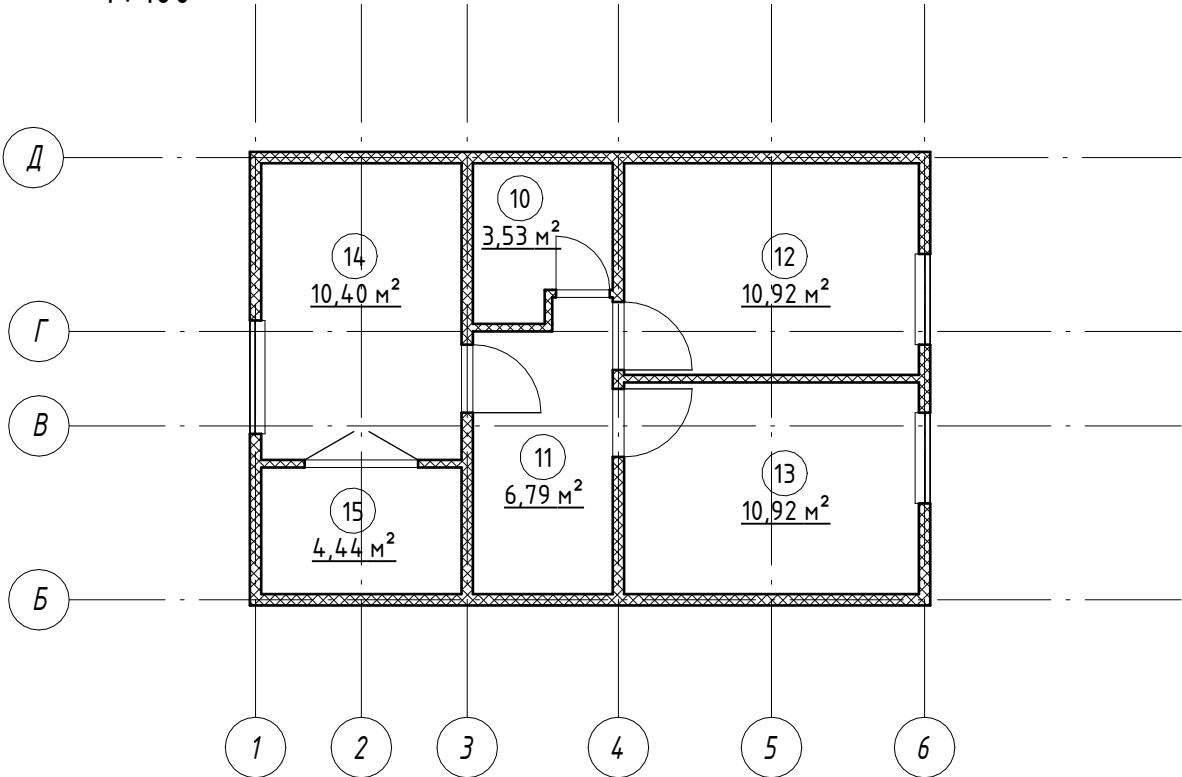

Экспликация помещений 2 этаж		
№ пом	Наименование	Площадь, м²
10	Сан.узел 2	3,53 м²
11	Холл/Лестница	6,79 м²
12	Спальня-1	10,92 м²
13	Спальня-2	10,92 м²
14	Кабинет	10,40 м²
15	Гардеробная	4,44 м²
Общий итог: 6		46,99 м²

Согласовано					
Взам. инв. №					
Подп. и дата					
Инв. № подл.					

						155-05-21 - АР			
						г. Кемерово			
Изм.	Кол.уч	Лист	№ док.	Подпись	Дата	Каркасный дом	Стадия	Лист	Листов
							П	02	
Чертил							30Ж		
Проверил						Экспликация помещений			
Норм. контр.									

Схема заполнения оконных и
дверных проемов на отм. 0.000
1:100


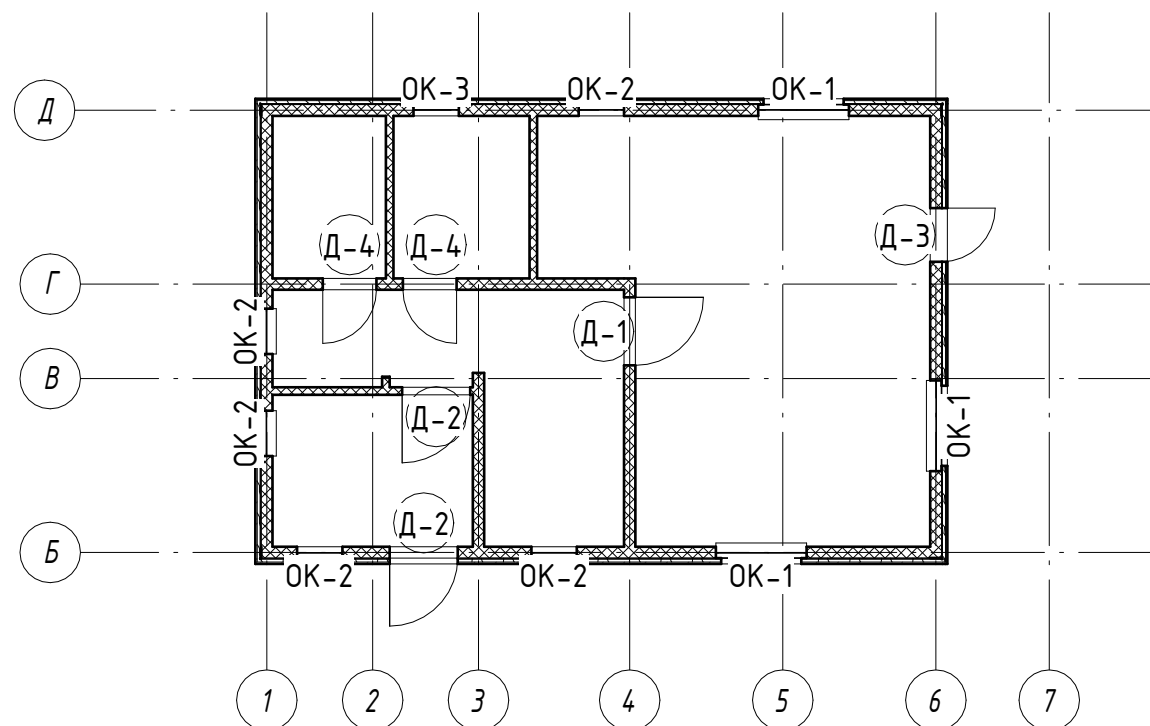


Схема заполнения оконных и
дверных проемов на отм. +2.850
1:100

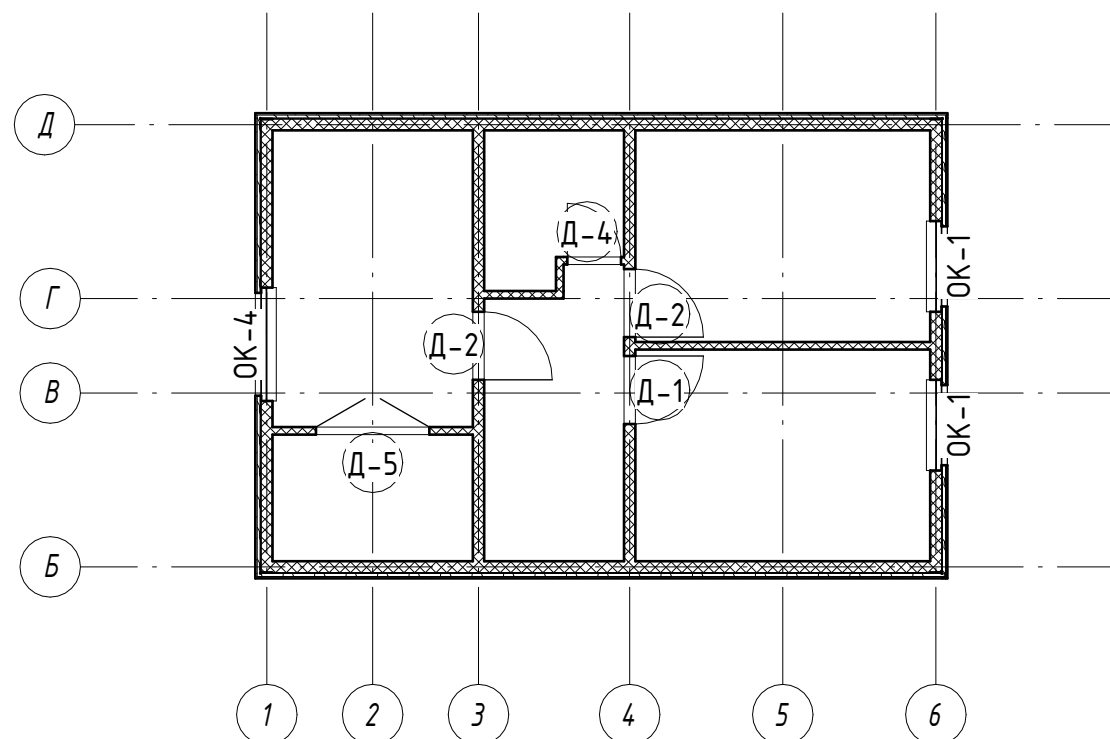


Спецификация дверей				
Поз.	Тип	Высота	Ширина	Кол.
План на отм. 0.000				
Д-1	ДГ 21-9	2100	900	1
Д-2	ДГ 21-9 л	2100	900	2
Д-3	ДГ 21-7 л ГОСТ 6629-88	2050	670	1
Д-4	ДГ 21-7 ГОСТ 6629-88	2050	670	2
План на отм. +2.850				
Д-1	ДГ 21-9	2100	900	1
Д-2	ДГ 21-9 л	2100	900	2
Д-4	ДГ 21-7 ГОСТ 6629-88	2050	670	1
Д-5	ДАК СПО ДВ 2100-1500	2100	1500	1

Спецификация окон				
Поз.	Обозначение	Наименование	Кол.	Тип
План на отм. 0.000				
ОК-1	ГОСТ 23166-99	ОП ОСП 15-15 П	3	1200 x 1350
ОК-2	ГОСТ 23166-99	ОП ОСП 15-7 л	5	600 x 1350
ОК-3	ГОСТ 23166-99	ОП ОСП 15-7 л	1	600 x 600
План на отм. +2.850				
ОК-1	ГОСТ 23166-99	ОП ОСП 15-15 П	2	1200 x 1350
ОК-4	ГОСТ 23166-99	ОП ОСП 15-13 П	1	1500 x 1350


Спецификация подоконных досок			
Маркировка типоразмера	Обозначение	Наименование	Кол-во
ПВ-1	ГОСТ 30673-99	ПД ПВХ 20x250x1450	8

						155-05-21 - АР			
						г. Кемерово			
Изм.	Кол.уч	Лист	№ док.	Подпись	Дата	Каркасный дом	Стадия	Лист	Листов
							П	03	
Чертил							30Ж		
Проверил									
Норм. контр.						Экспликация окон и дверей			

Восточный
1 : 100

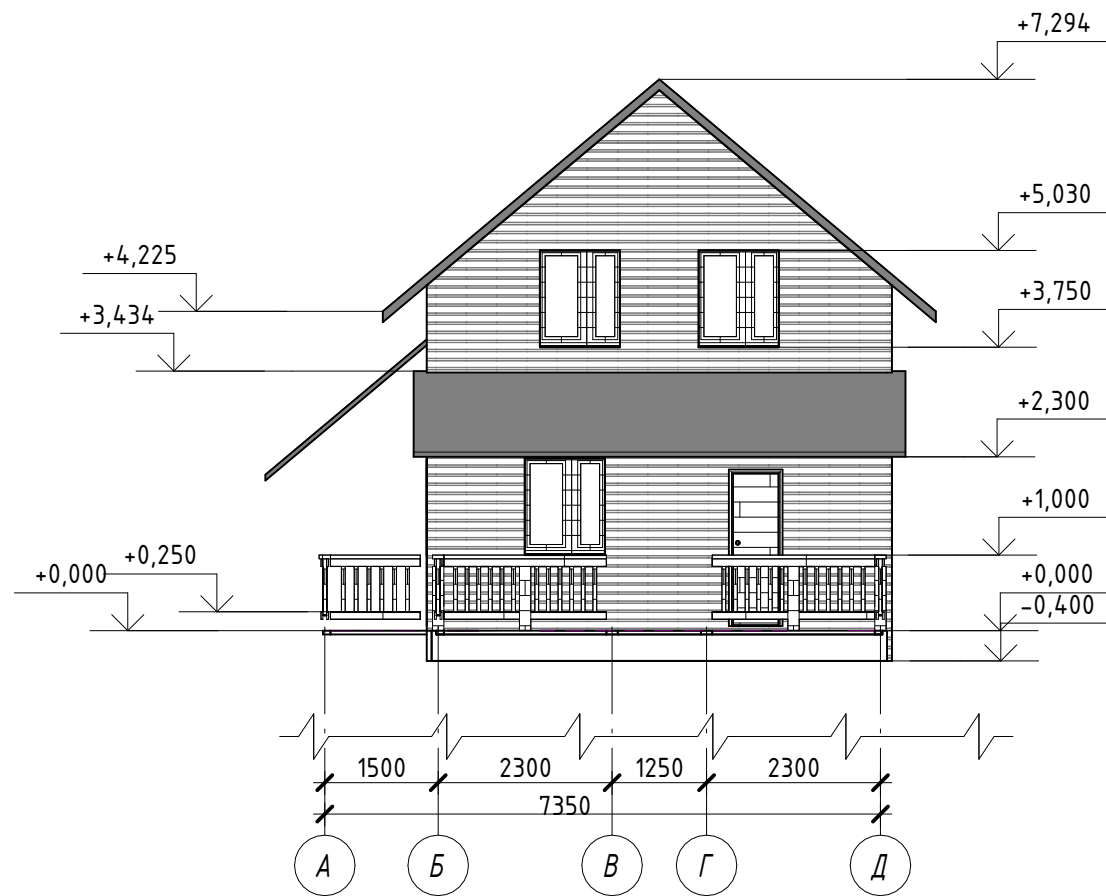

Южный
1 : 100

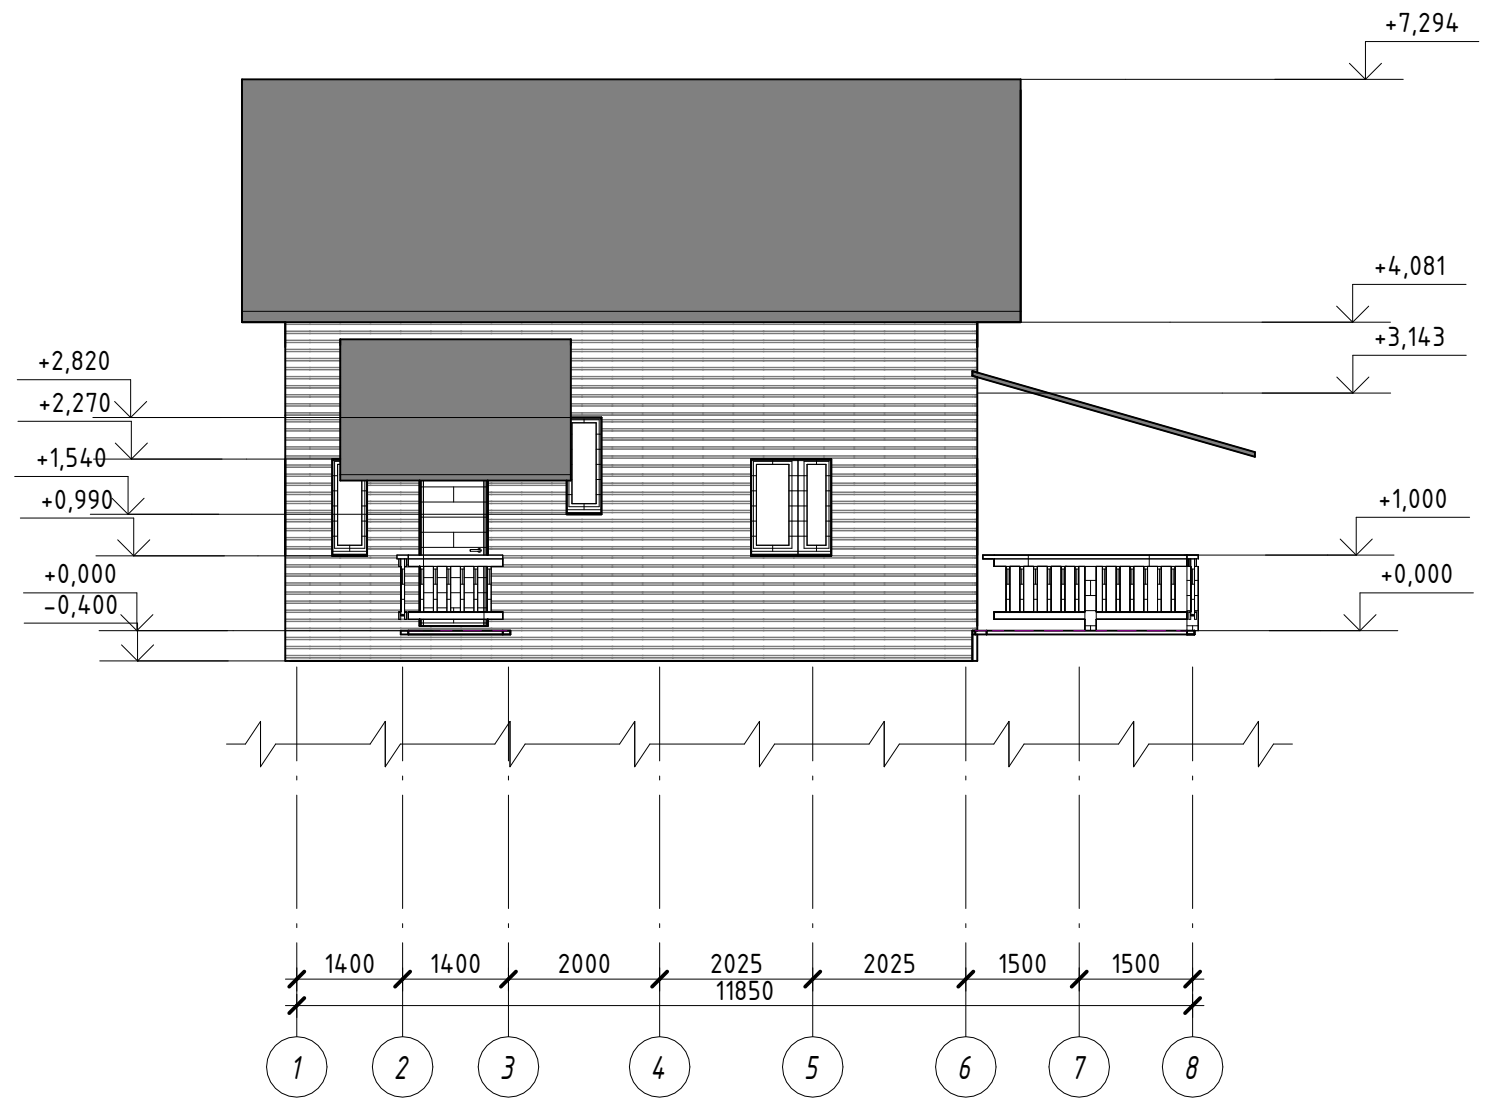

Согласовано

Взам. инв. №

Подп. и дата

Инв. № подл.


155-05-21 - АР

г. Кемерово


Изм.	Кол.уч	Лист	№ док.	Подпись	Дата				
						Каркасный дом			
						Фасад А-Д 1-2			
						Стадия	Лист	Листов	
						П	04		
						30Ж			

Формат: А3А

Западный
1 : 100

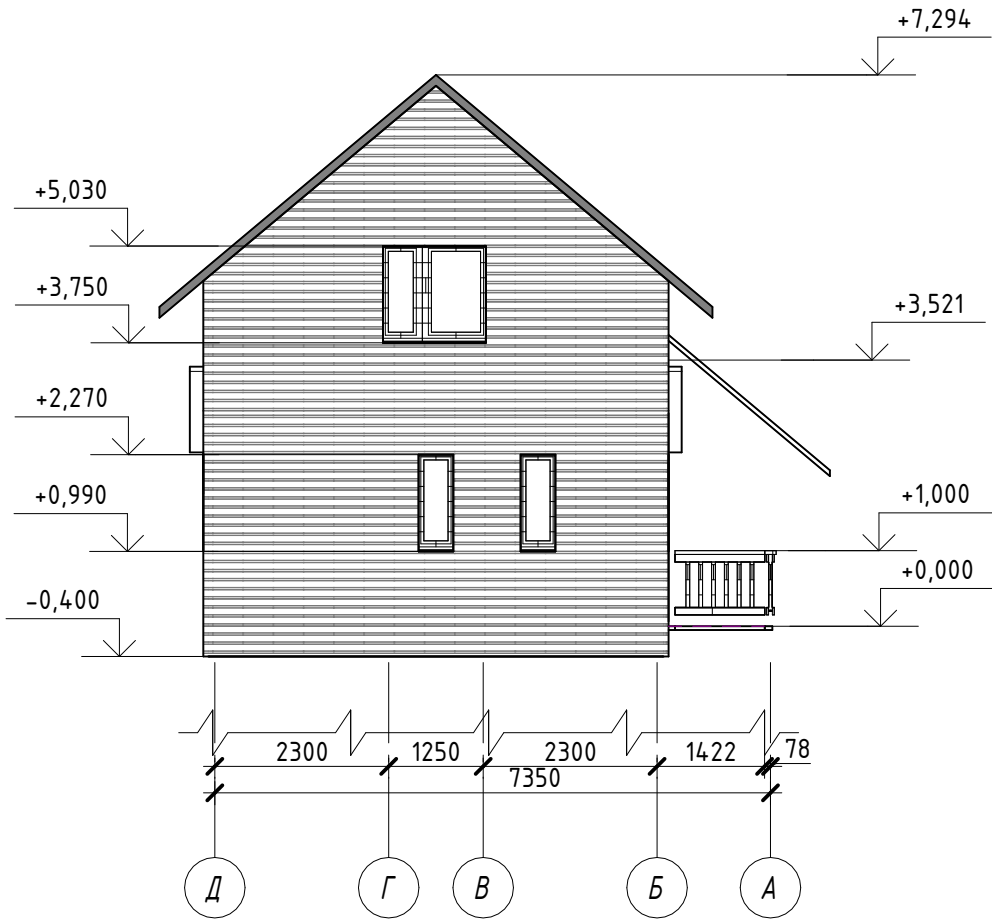


Северный
1 : 100

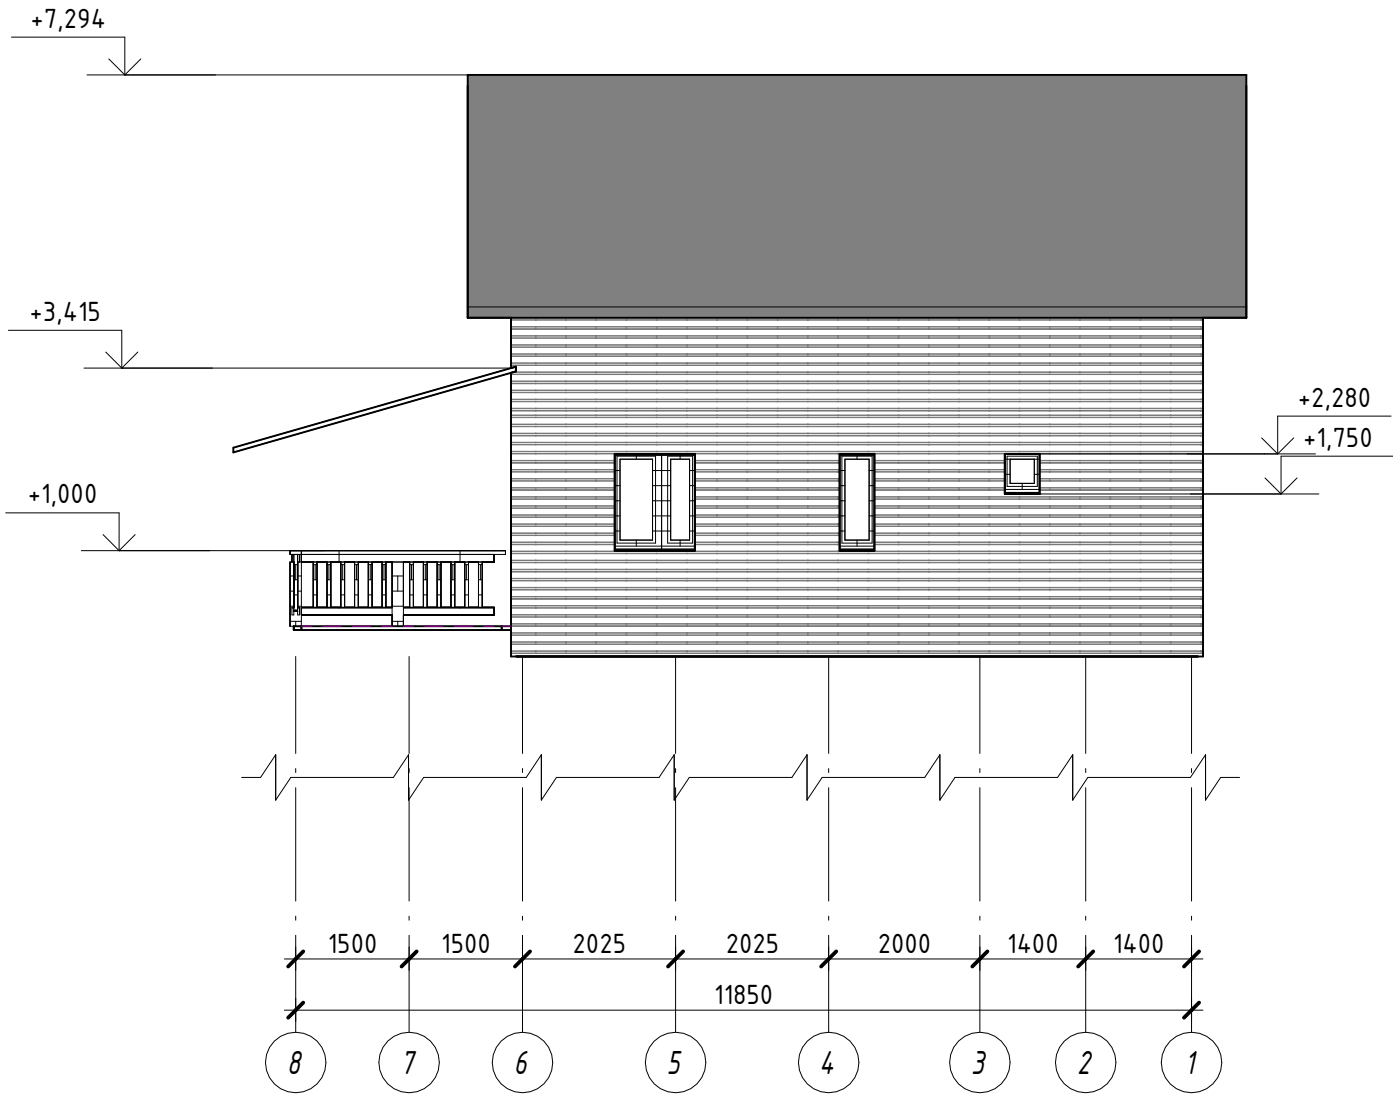

Согласовано			
Взам. инв. №			
Подп. и дата			
Инв. № подл.			

						155-05-21 - АР					
						г. Кемерово					
Изм.	Кол.уч	Лист	№ док.	Подпись	Дата						
		Мухина ЕА				Каркасный дом	Стадия	Лист	Листов		
							П	05			
Чертил		Мухина ЕА					30Ж				
Проверил						Фасад Д-А 8-1					
Норм. контр.											

Согласовано

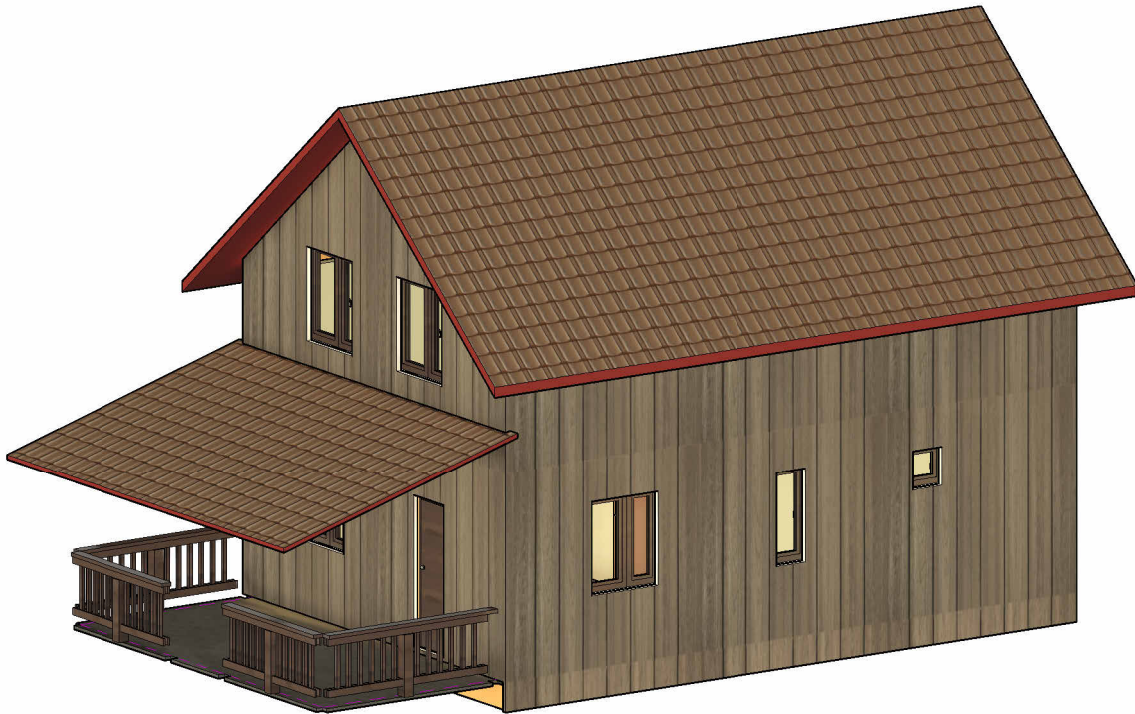

						155-05-21 -			
						г. Кемерово			
Изм.	Кол.уч	Лист	№ док.	Подпись	Дата	Каркасный дом	Стадия	Лист	Листов
							П	06	
Чертил	Мухина ЕА					ЗД Виды	30Ж		
Проверил									
Норм. контр.									

Инв. № подл.

Подп. и дата

Взам. инв. №