


Проект каркасного дома

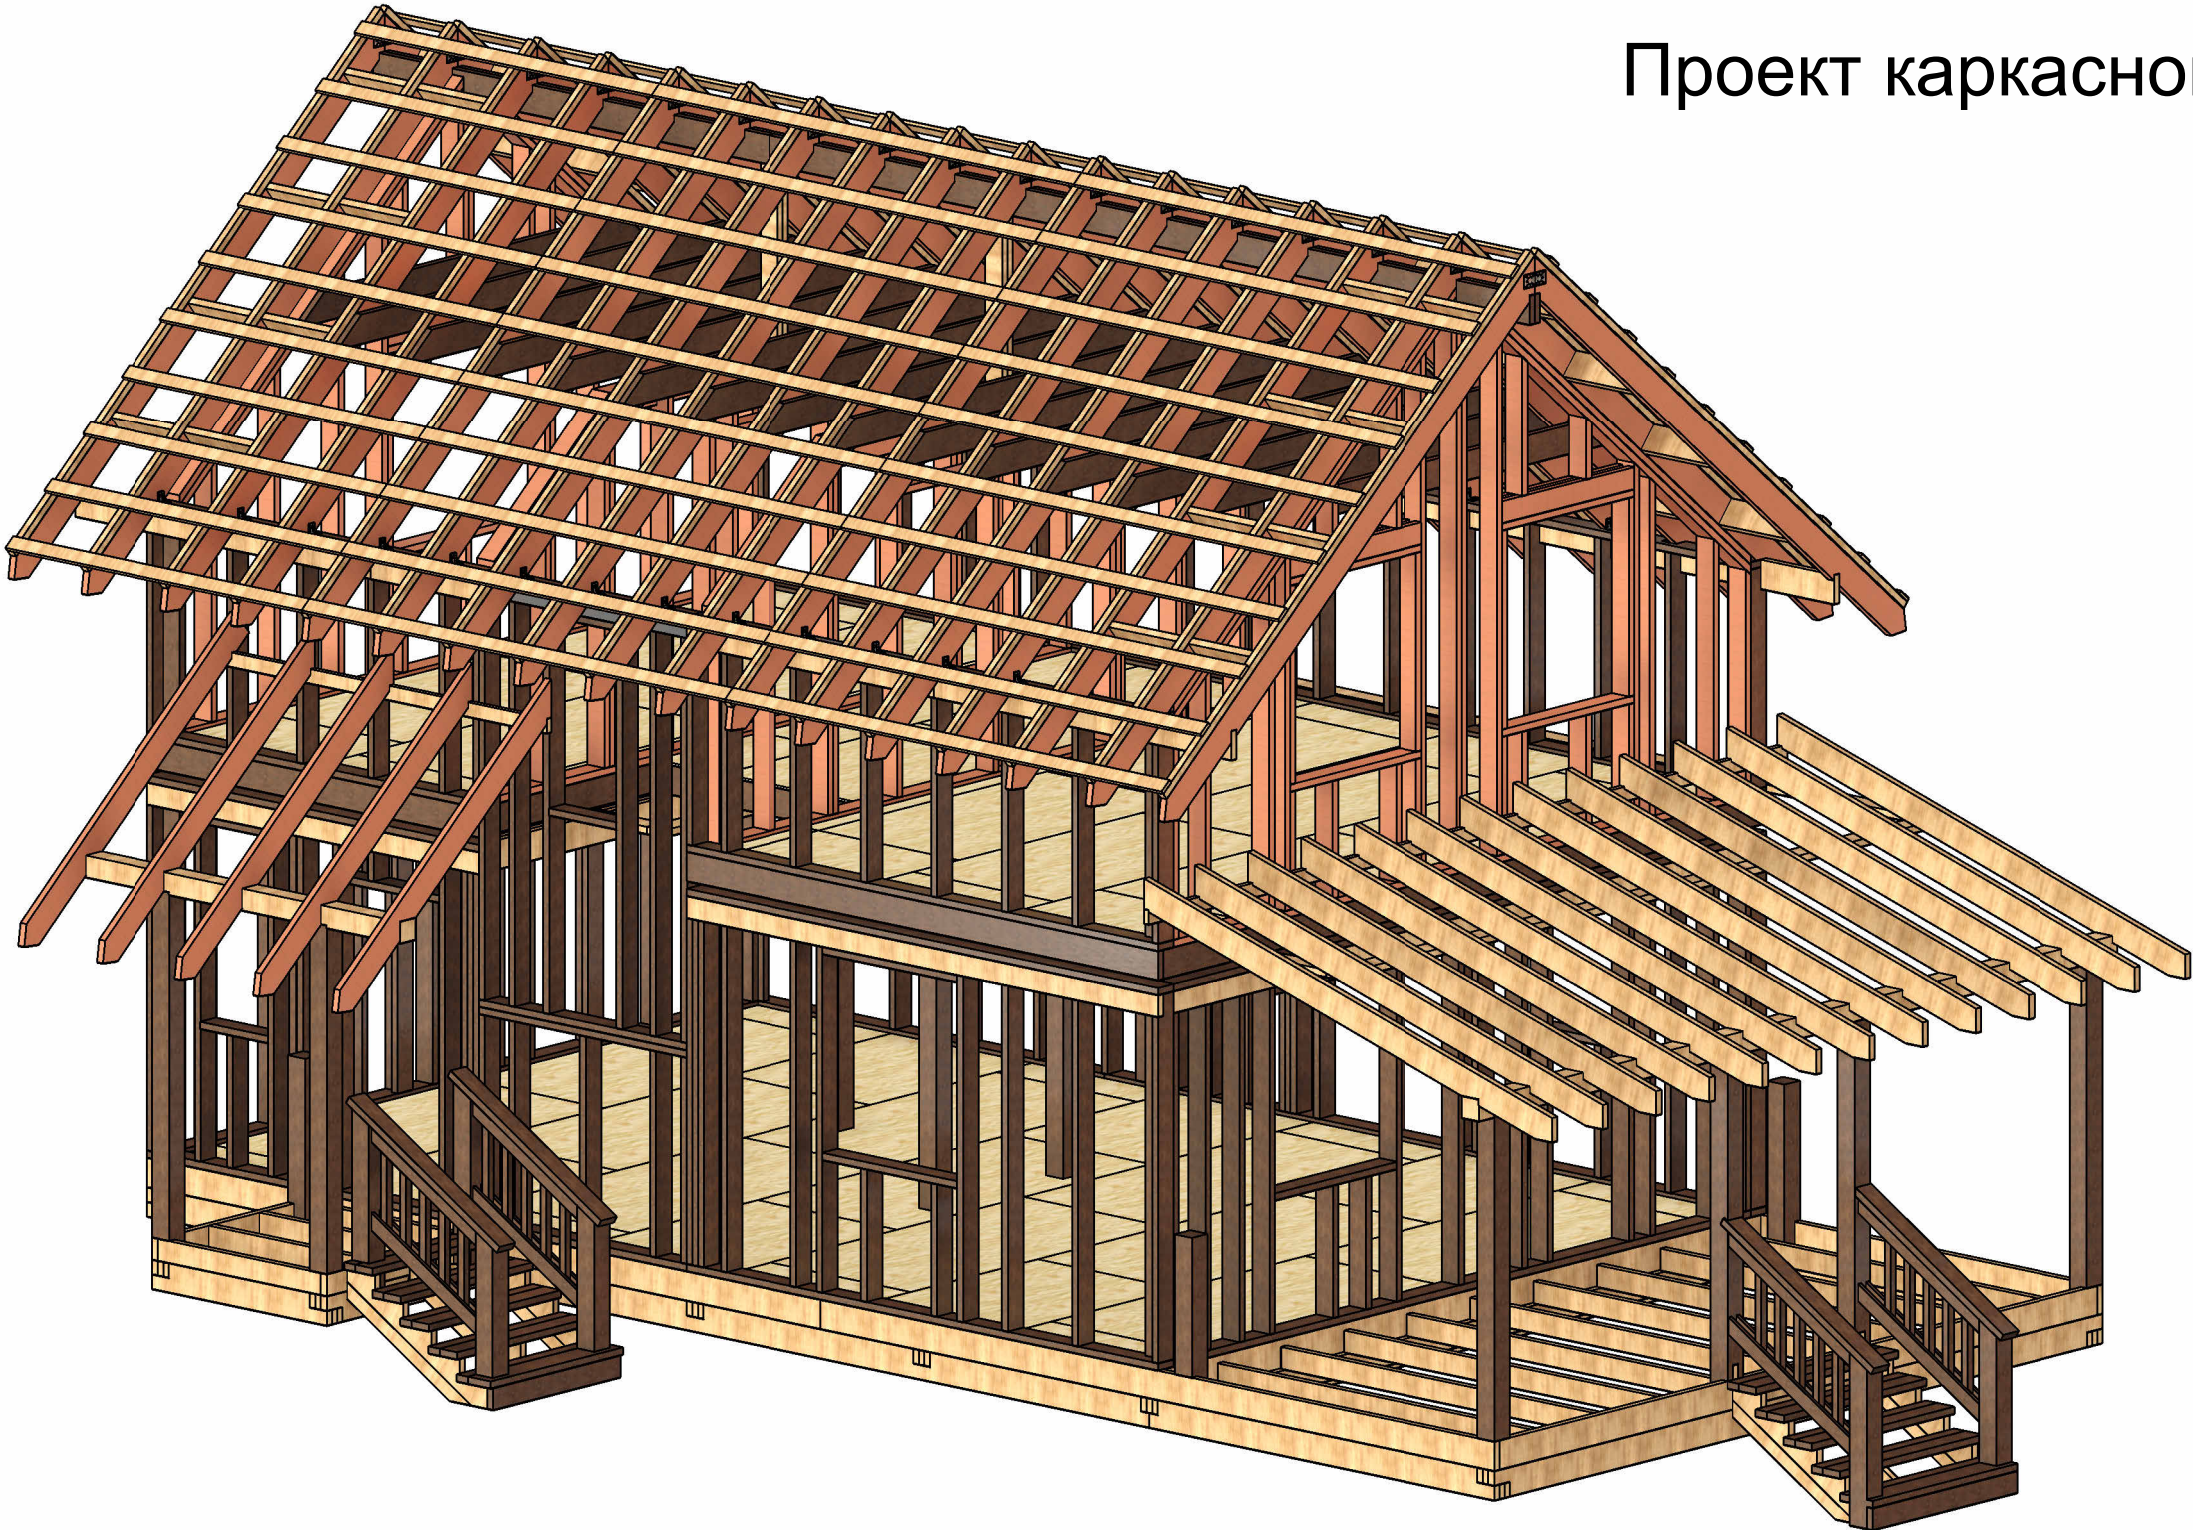

Согласовано					
Взам. инв. №					
Подп. и дата					
Инв. № подл.					

						№ проекта -			
						Россия, г.Кемерово			
Изм.	Кол.уч	Лист	№ док.	Подпись	Дата				
						Проект каркасного дома	Стадия	Лист	Листов
							КР	001	
						Титульный лист			

Согласовано			
Взам. инв. №			
Подп. и дата			
Инв. № подл.			

Раскрой. Нижняя обвязка			
Поз.	Наименование	Размер.мм	Колич. .шт
1	Доска балки	4875x200x50	2
2	Доска балки	5100x200x50	2
3	Доска балки	2025x200x50	2
4	Доска балки	6050x200x50	4
5	Доска балки	3075x200x50	4
6	Доска балки	2875x200x50	4
7	Доска балки	1575x200x50	1
8	Доска балки	5925x200x50	1
9	Доска балки	3875x200x50	2
10	Доска балки	3625x200x50	2
11	Доска балки	6000x200x50	15
12	Доска балки	1450x150x50	4
12	Доска балки	1488x150x50	2
12	Доска балки	1550x200x50	3
12	Доска балки	2850x<варианты>	2
13	Доска балки	1650x200x50	3

ОСНОВНЫЕ ТЭП

Общие указания:

1. Класс ответственности здания – 2;
2. Категорию здания по конструктивной пожарной опасности – С0;
3. Степень огнестойкости здания II;
4. Функциональная пожарная безопасность здания Ф1.3

а.

Ведомость основных комплектов рабочих чертежей (Ведомость ссылочных и прилагаемых документов, Содержание тома и т.п.)


Обозначение	Наименование	Примечание
Обозначение основного комплекта рабочих чертежей	Наименование основного комплекта рабочих чертежей	Дополнительные сведения

Ведомость материала настила полов						
Наименование	Материал	Изображение	Площадь, м2	Площадь, кф 1.1	Кол.листов	Комментарии
Плита пола 1250x2500x18мм	Древесина хвоя		49,50 м²	54,45 м²	17	
Плита пола 1250x2500x18мм	Древесина хвоя		44,92 м²	49,41 м²	16	
			94,42 м²	103,86 м²	33	


Спецификация крепежа				
№	Наимен.	Обозначение	Кол.	Примечание
ПЛ-1	210x90x2 мм	Гост 2111-92	17	
УГ-1	70x55x2.5 мм	Гост 2111-92	30	

						№ проекта – КР			
						Россия, г. Кемерово			
Изм.	Кол.уч.	Лист	№ док.	Подпись	Дата	Проект каркасного дома	Стадия	Лист	Листов
ГАП							КР	02	
ГИП									
Рук.пр									
Чертил	Мухина ЕА					Общие данные			
Проверил									
Норм. контр.									

Схема расположения свай на
отм. -0.400
1: 75

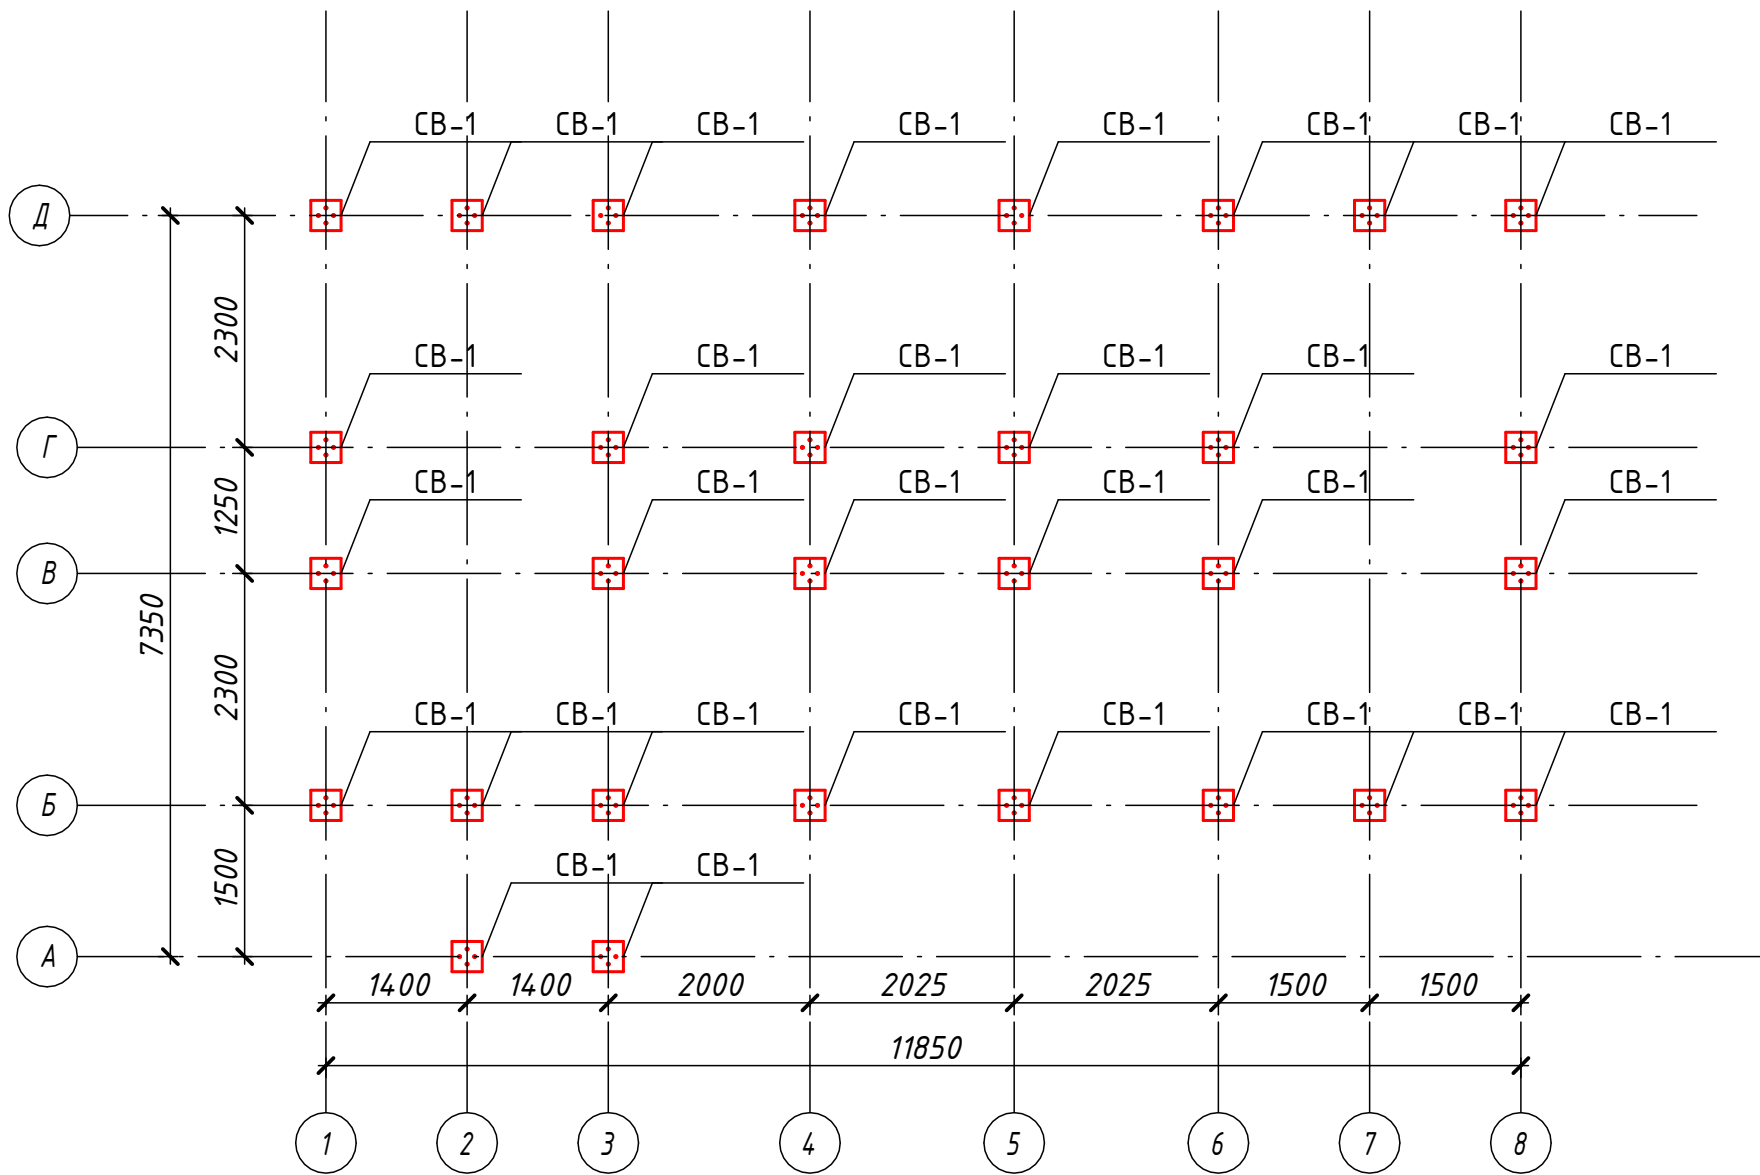

Спецификация несущих колонн (свай)		
Поз.	Размер, мм	Колич.
CB-1	108х3500 мм	30

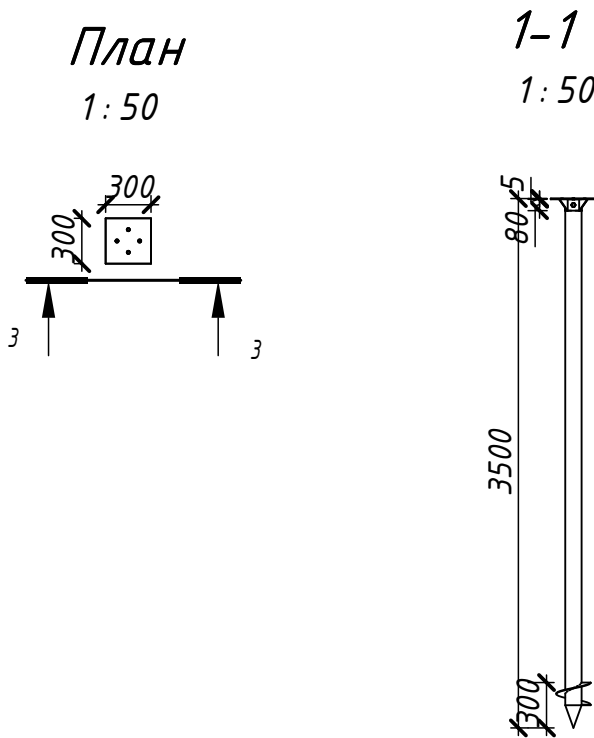


Согласовано				
Инв. № подл.	Взам. инв. №	Подп. и дата		

						№ проекта -		
						Россия, г. Кемерово		
Изм.	Кол.уч.	Лист	№ док.	Подпись	Дата	Проект каркасного дома	Стадия	Лист
							КР	03
						Схема расположения свай на отм -0.400		

Обвязка свай на отм. -0.400

1:50

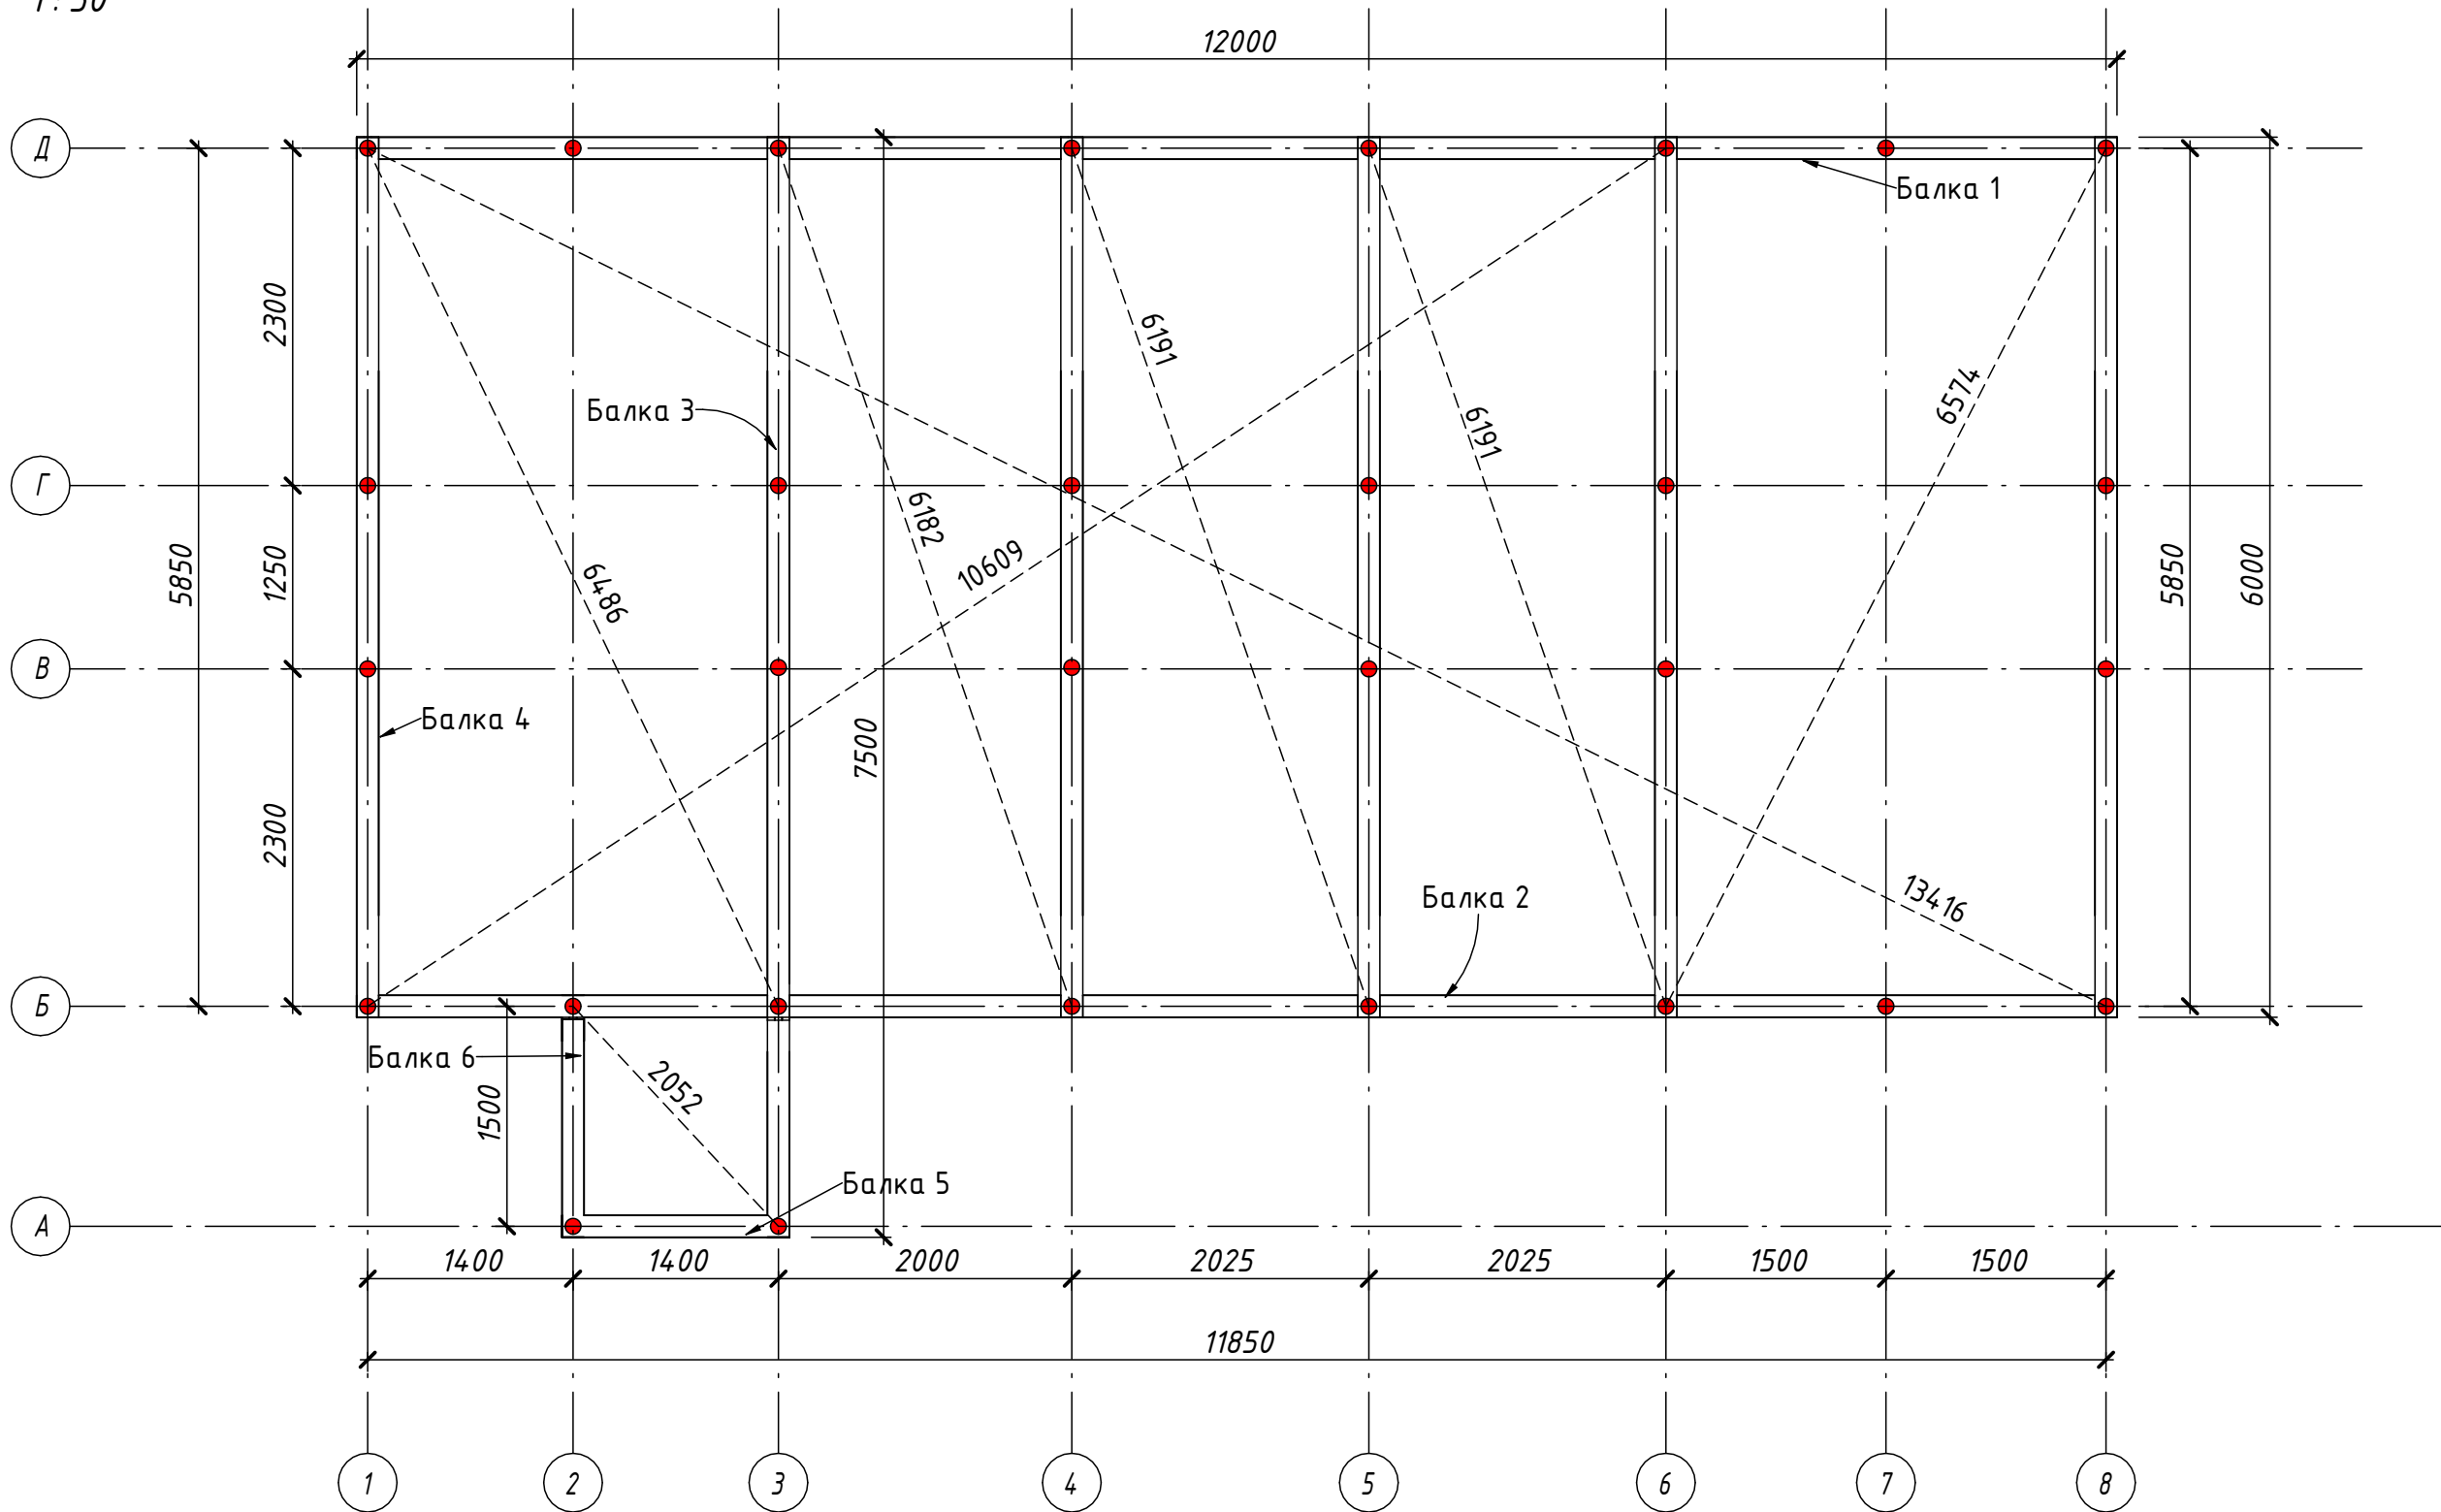

Согласовано				
Взам. инв. №				
Подп. и дата				
Инв. № подл.				

						№ проекта -				
						Россия, г. Кемерово				
Изм.	Кол.уч	Лист	№ док.	Подпись	Дата	Проект каркасного дома		Стадия	Лист	Листов
								КР	04	
						Схема обвязки свай				


Согласовано

Взам. инв. №


Подп. и дата

Инв. № подл.

Балка 1

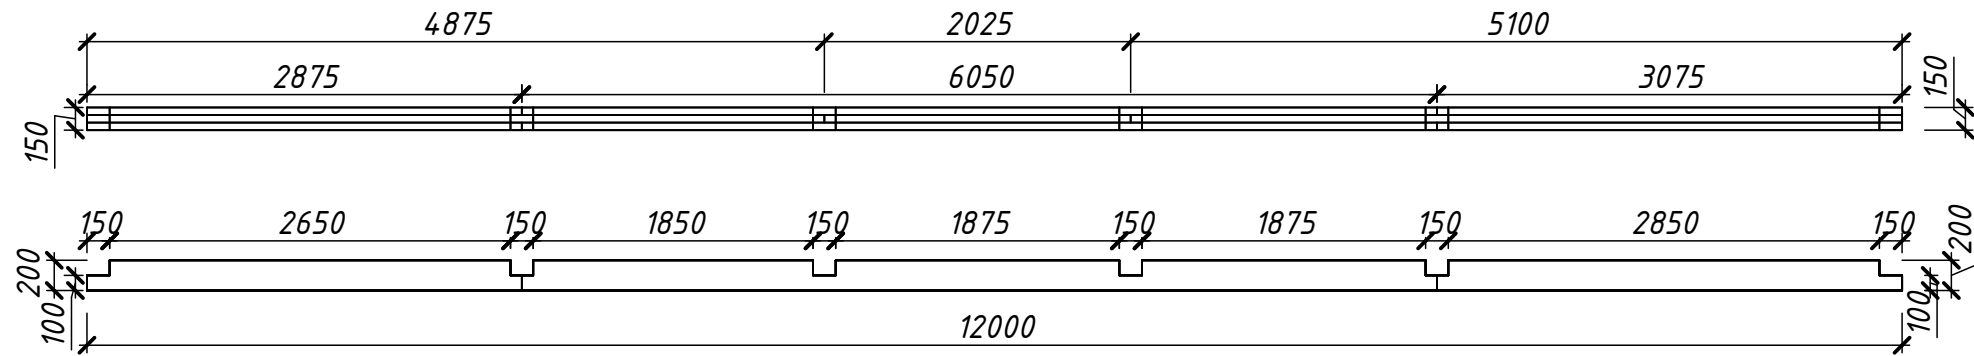

Балка 2

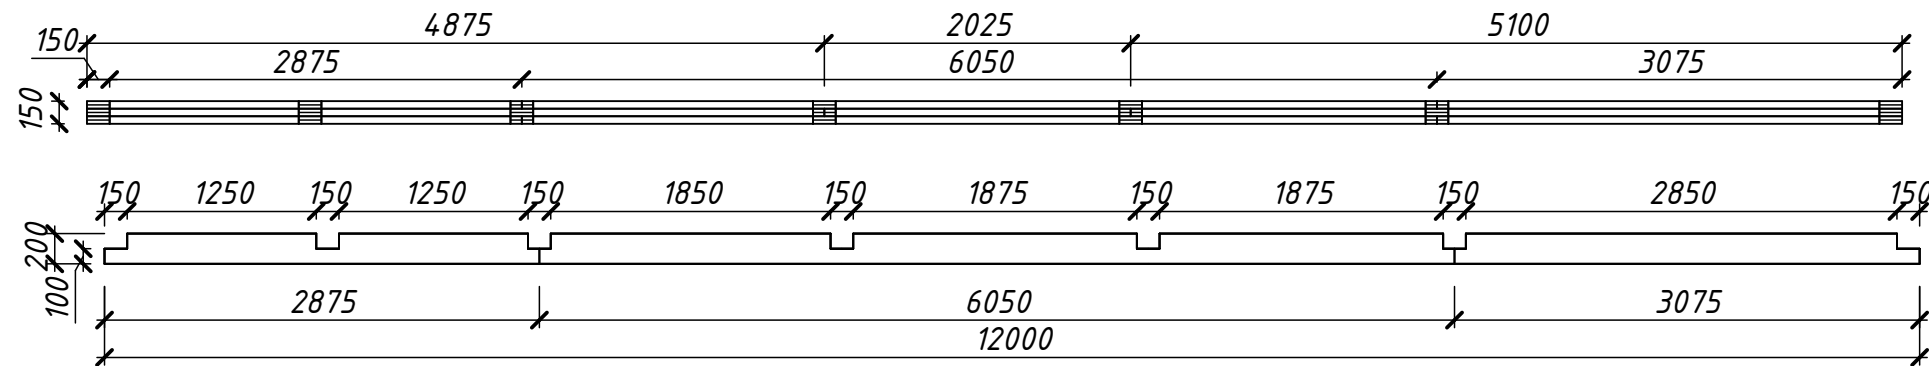

Раскрой. Нижняя обвязка

Поз.	Наименование	Размер.мм	Колич. .шт
1	Доска балки	4875x200x50	2
2	Доска балки	5100x200x50	2
3	Доска балки	2025x200x50	2
4	Доска балки	6050x200x50	4
5	Доска балки	3075x200x50	4
6	Доска балки	2875x200x50	4
7	Доска балки	1575x200x50	1
8	Доска балки	5925x200x50	1
9	Доска балки	3875x200x50	2
10	Доска балки	3625x200x50	2
11	Доска балки	6000x200x50	15
12	Доска балки	1450x150x50	4
12	Доска балки	1488x150x50	2
12	Доска балки	1550x200x50	3
12	Доска балки	2850x<варианты>	2
13	Доска балки	1650x200x50	3

№ проекта -


Россия, г. Кемерово

Проект каркасного дома

Стадия	Лист	Листов
КР	05	

Балки обвязки

Нижнее перекрытие на отм.
-0.200
1:50


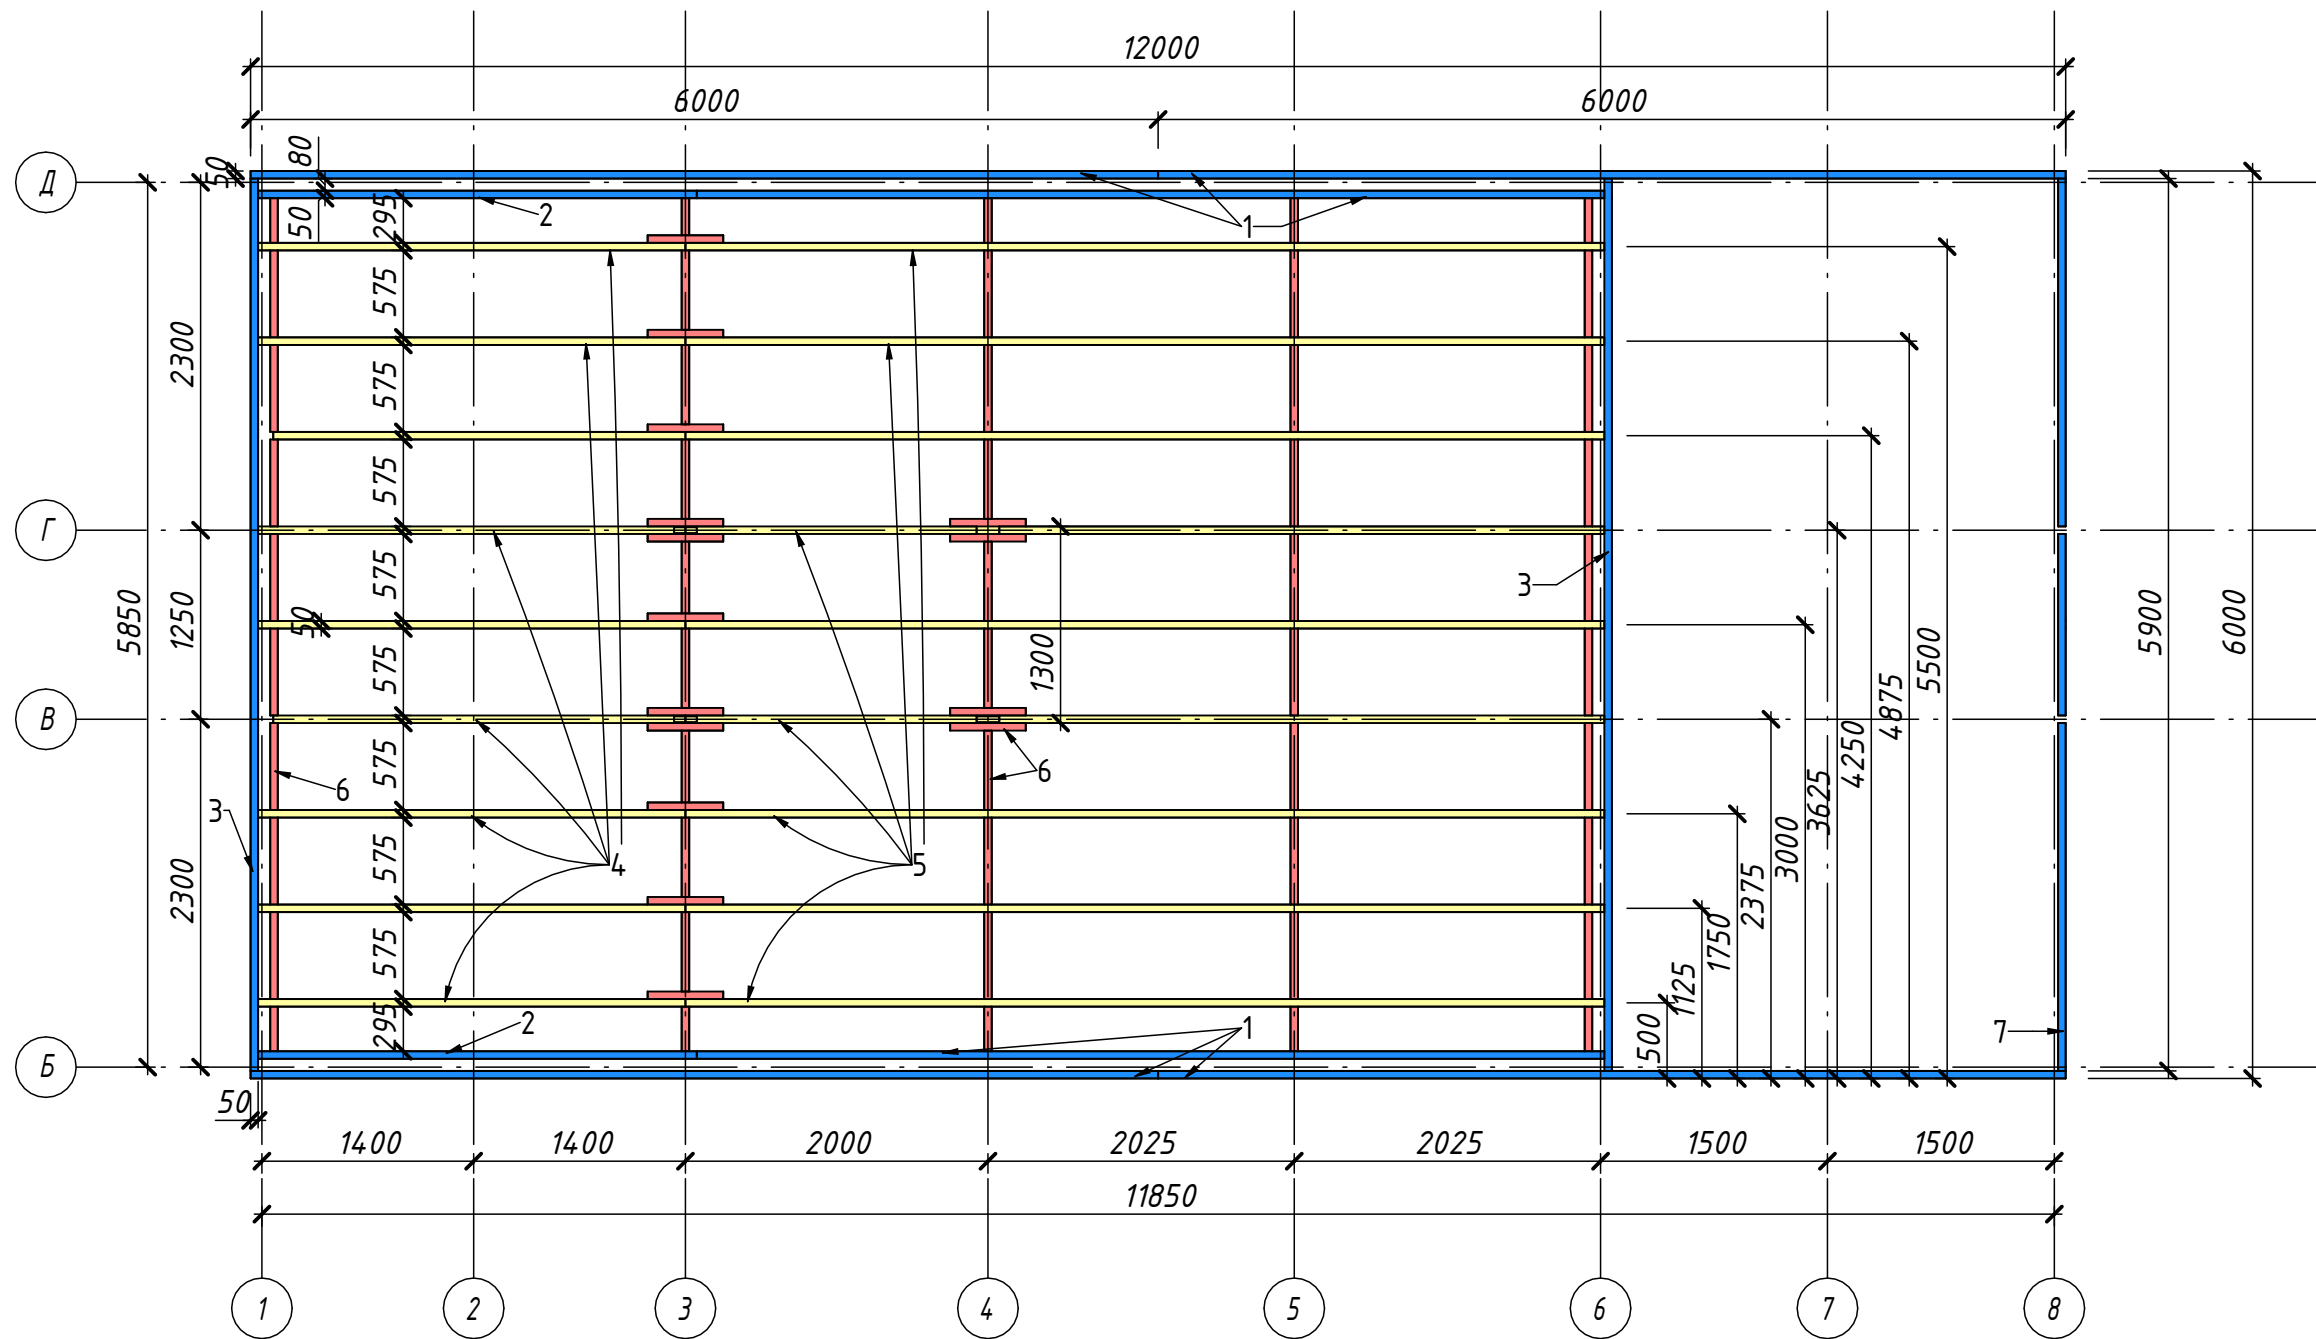


Согласовано				

Инв. № подл.	Подп. и дата	Взам. инв. №	

Раскрой. Нижнее перекрытие				Раскрой. Нижнее перекрытие			
Поз.	Наименование	Размер.мм	Колич.шт	Поз.	Наименование	Размер.мм	Колич.шт
1	Фасадная доска	6000x200x50	6	7	Мостик	475x200x50	2
2	Фасадная доска	2900x200x50	2	8	Мостик	500x200x50	15
3	Фасадная доска	5900x200x50	3	9	Мостик	525x200x50	10
4	Лага	2725x200x50	2	10	Мостик	575x200x50	28
4	Лага	2825x200x50	7	11	Мостик	295x200x50	9
5	Лага	6075x200x50	9				
6	Мостик	245x200x50	1				



						№ проекта -		
						Россия, г. Кемерово		
Изм.	Кол.уч.	Лист	№ док.	Подпись	Дата	Проект каркасного дома	Стадия	Лист
							КР	06
						Нижнее перекрытие		

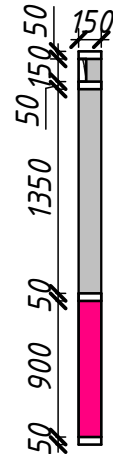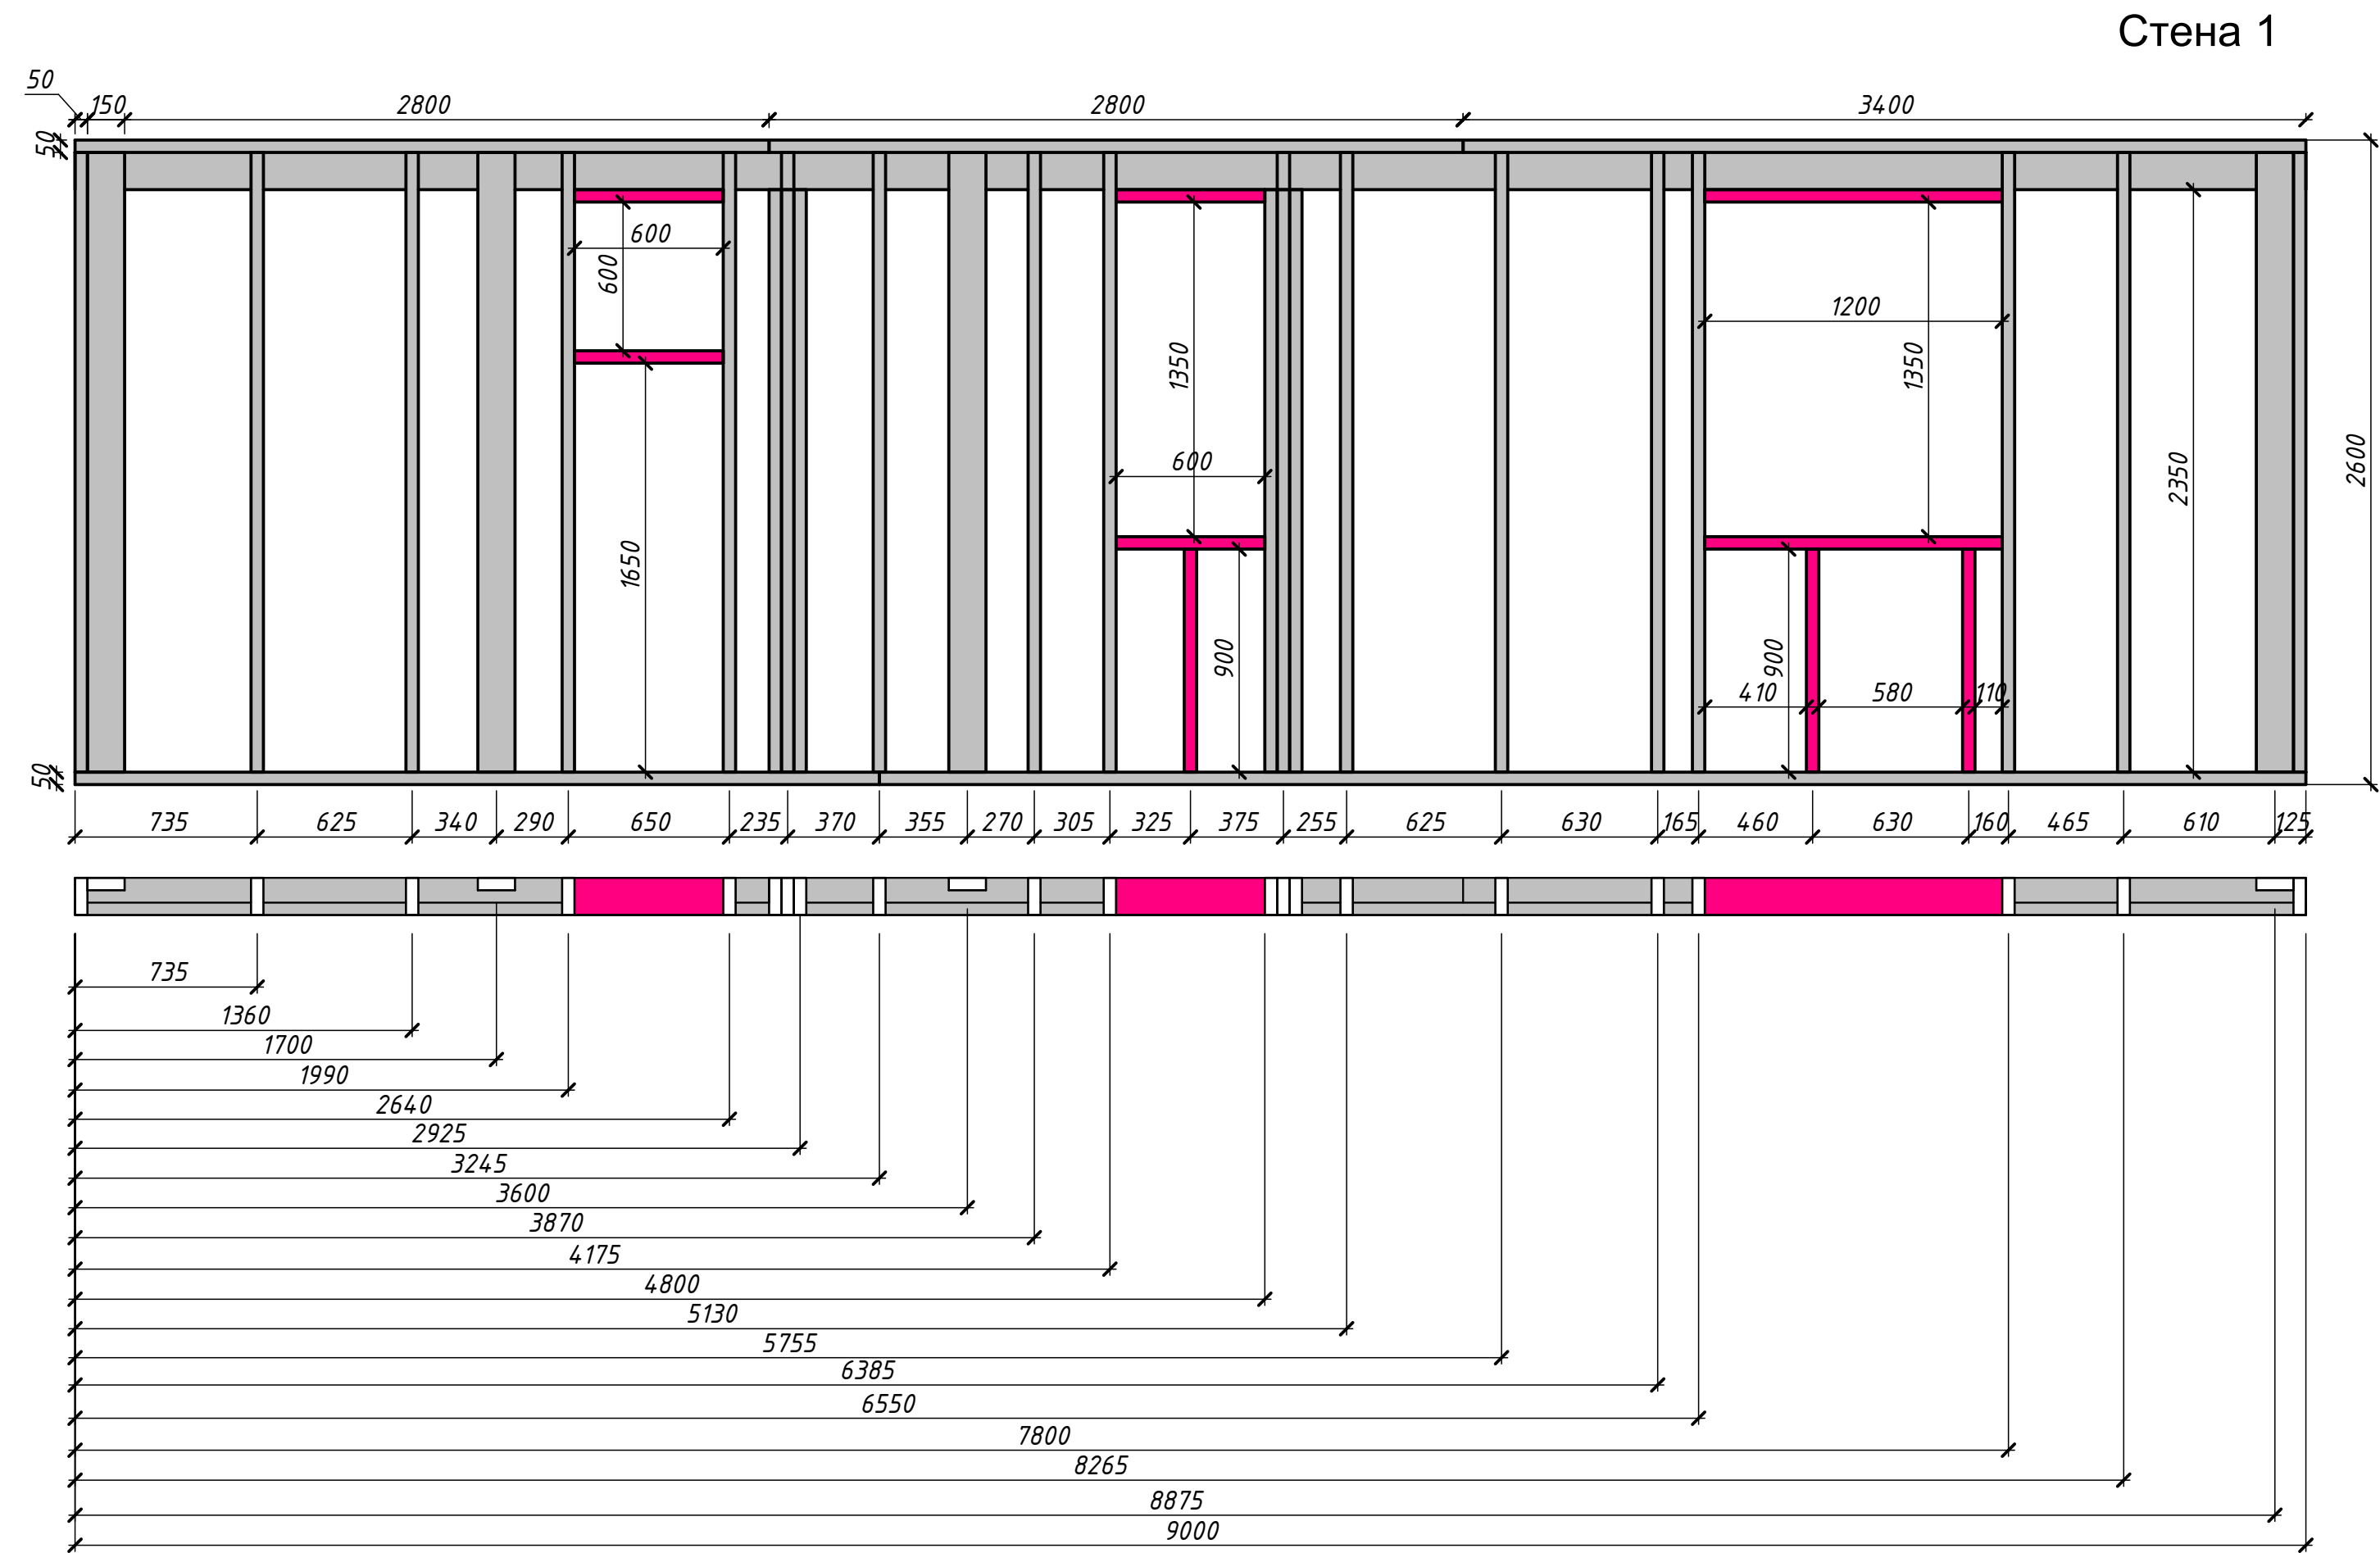

Раскрой. Стена-1			
Поз.	Наименование	Размер.мм	Колич .шт
1	Лежень	2800х150х50	2
1	Лежень	5755х150х50	2
2	Лежень	3245х150х50	3
3	Стойка	2500х150х50	21
4	Балка	1200х150х50	2
5	Стойка	900х150х50	3
6	Балка	600х150х50	4
7	Стойка	2350х150х50	4

№ проекта -						
Россия, г. Кемерово						
Изм.	Кол.уч.	Лист	№ док.	Подпись	Дата	
						Проект каркасного дома
						Стадия
						Лист
						Листов
						КР
						07
						Раскрой стена 1



Согласовано				
Инв. № подл.	Подп. и дата	Взам. инв. №		

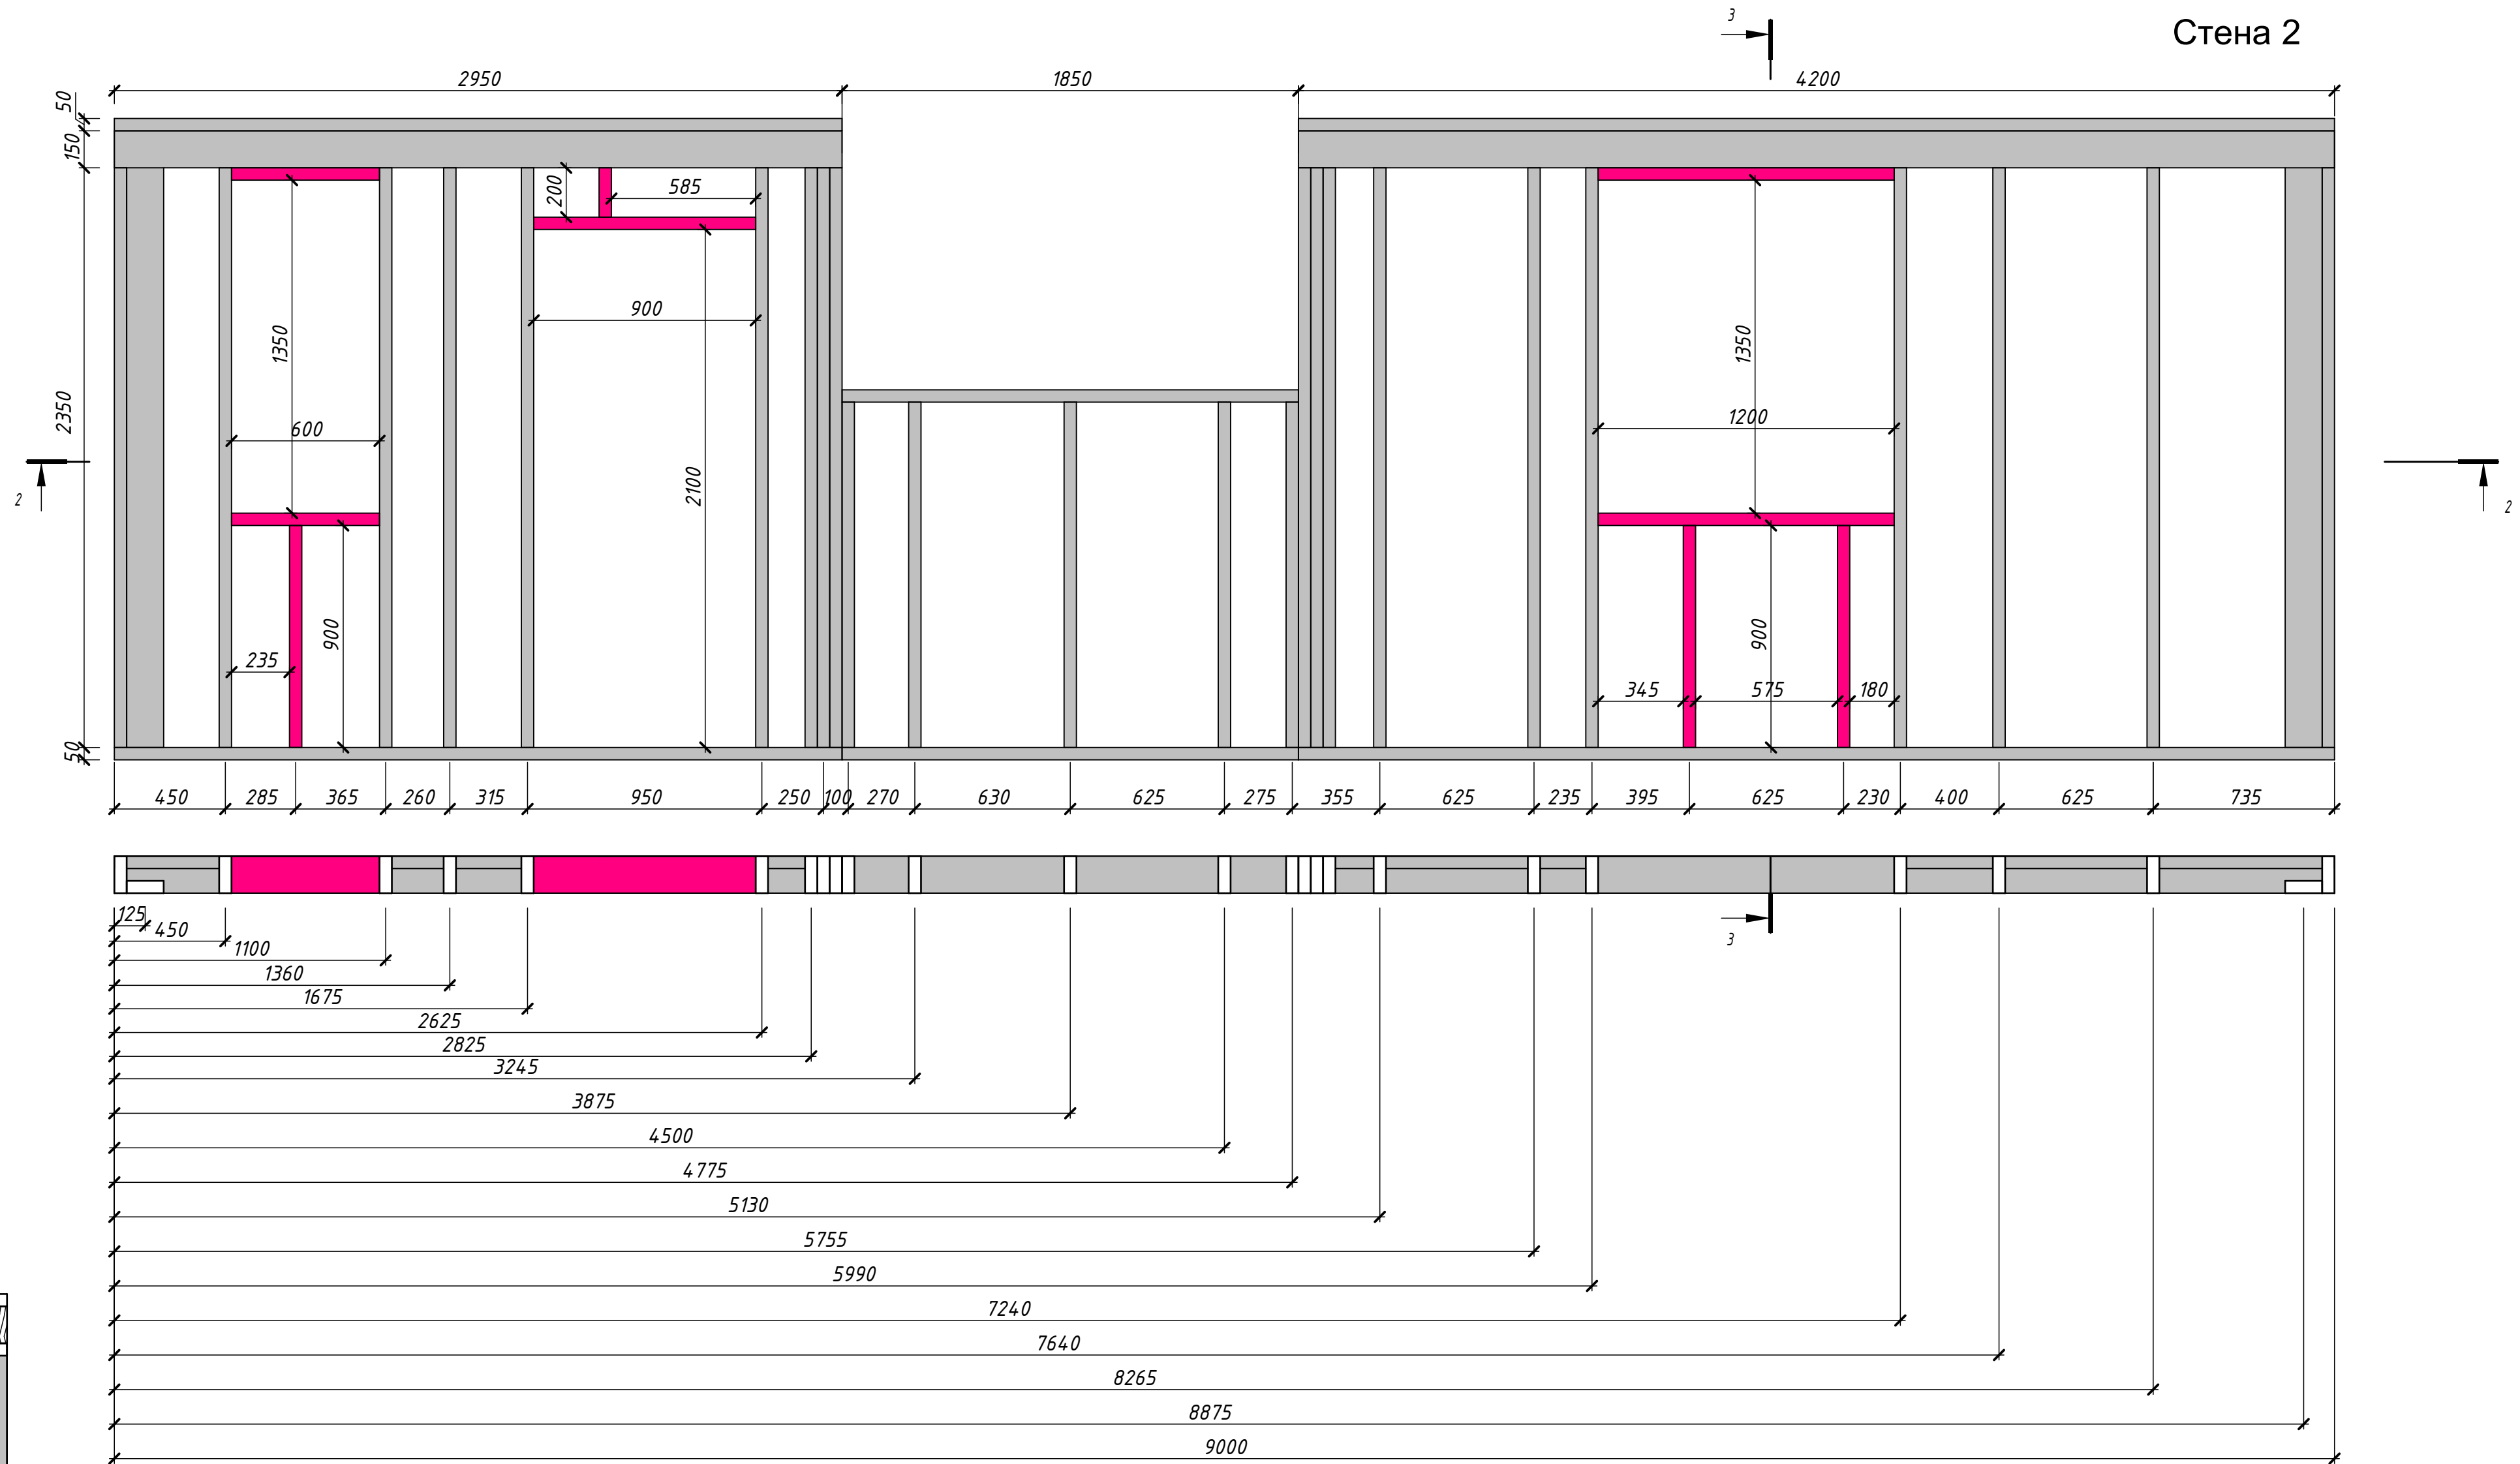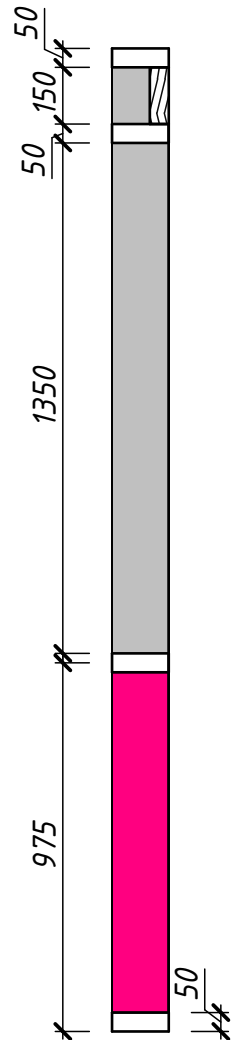

Раскрой. Стена-2			
Поз.	Наименование	Размер.мм	Колич. .шт
1	Лежень	2950x150x50	3
2	Лежень	4200x150x50	3
3	Лежень	1850x150x50	2
4	Стойка	2500x150x50	17
5	Стойка	1400x150x50	5
6	Стойка	900x150x50	4
7	Балка	1200x150x50	2
8	Стойка	350x150x50	1
9	Балка	600x150x50	2
10	Стойка	2350x150x50	4

№ проекта -						
Россия, г.Кемерово						
Изм.	Кол.уч.	Лист	№ док.	Подпись	Дата	
						Проект каркасного дома
						Стадия
						Лист
						Листов
						КР
						08
						Раскрой стена 2



Согласовано			
Взам. инв. №			
Подп. и дата			
Инв. № подл.			

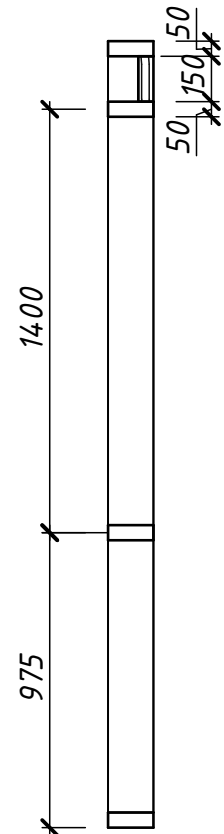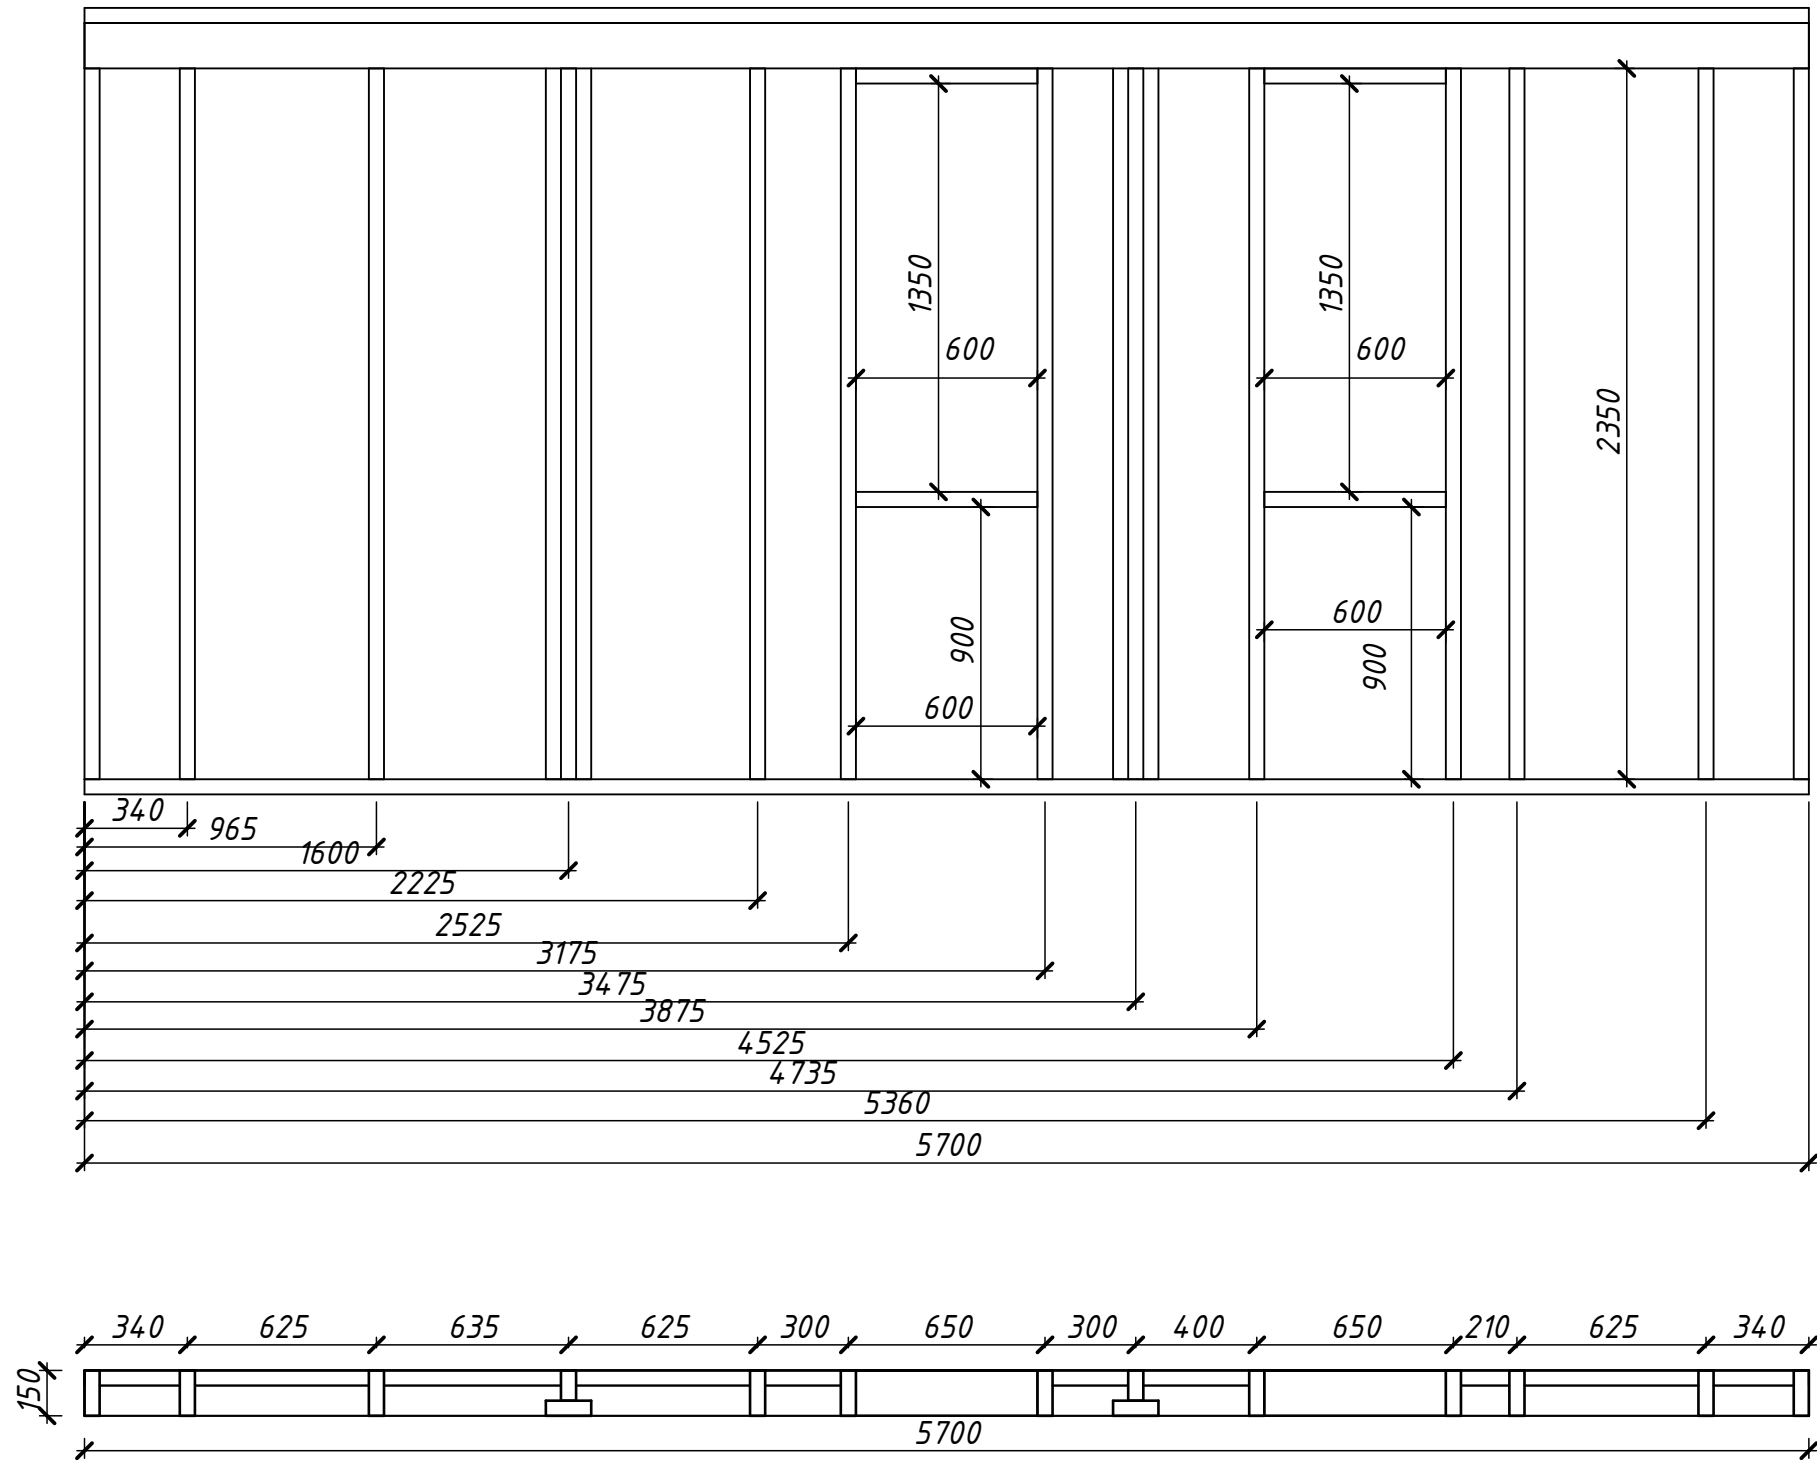

Раскрой. Стена-3			
Поз.	Наименование	Размер.мм	Колич .шт
1	Лежень	5700x150x50	3
2	Стойка	2500x100x50	2
3	Стойка	2500x150x50	13
4	Балка	600x150x50	4

						№ проекта -			
						Россия, г. Кемерово			
Изм.	Кол.уч.	Лист	№ док.	Подпись	Дата	Проект каркасного дома	Стадия	Лист	Листов
							КР	09	
						Раскрой стена 3			

Стена 4

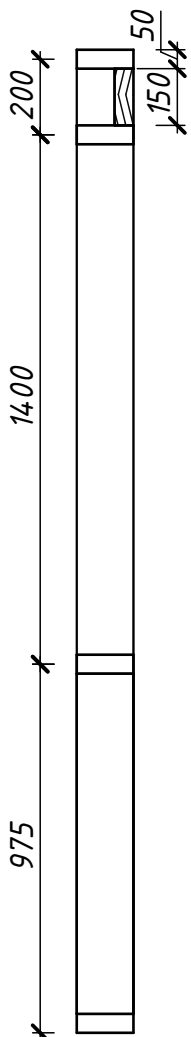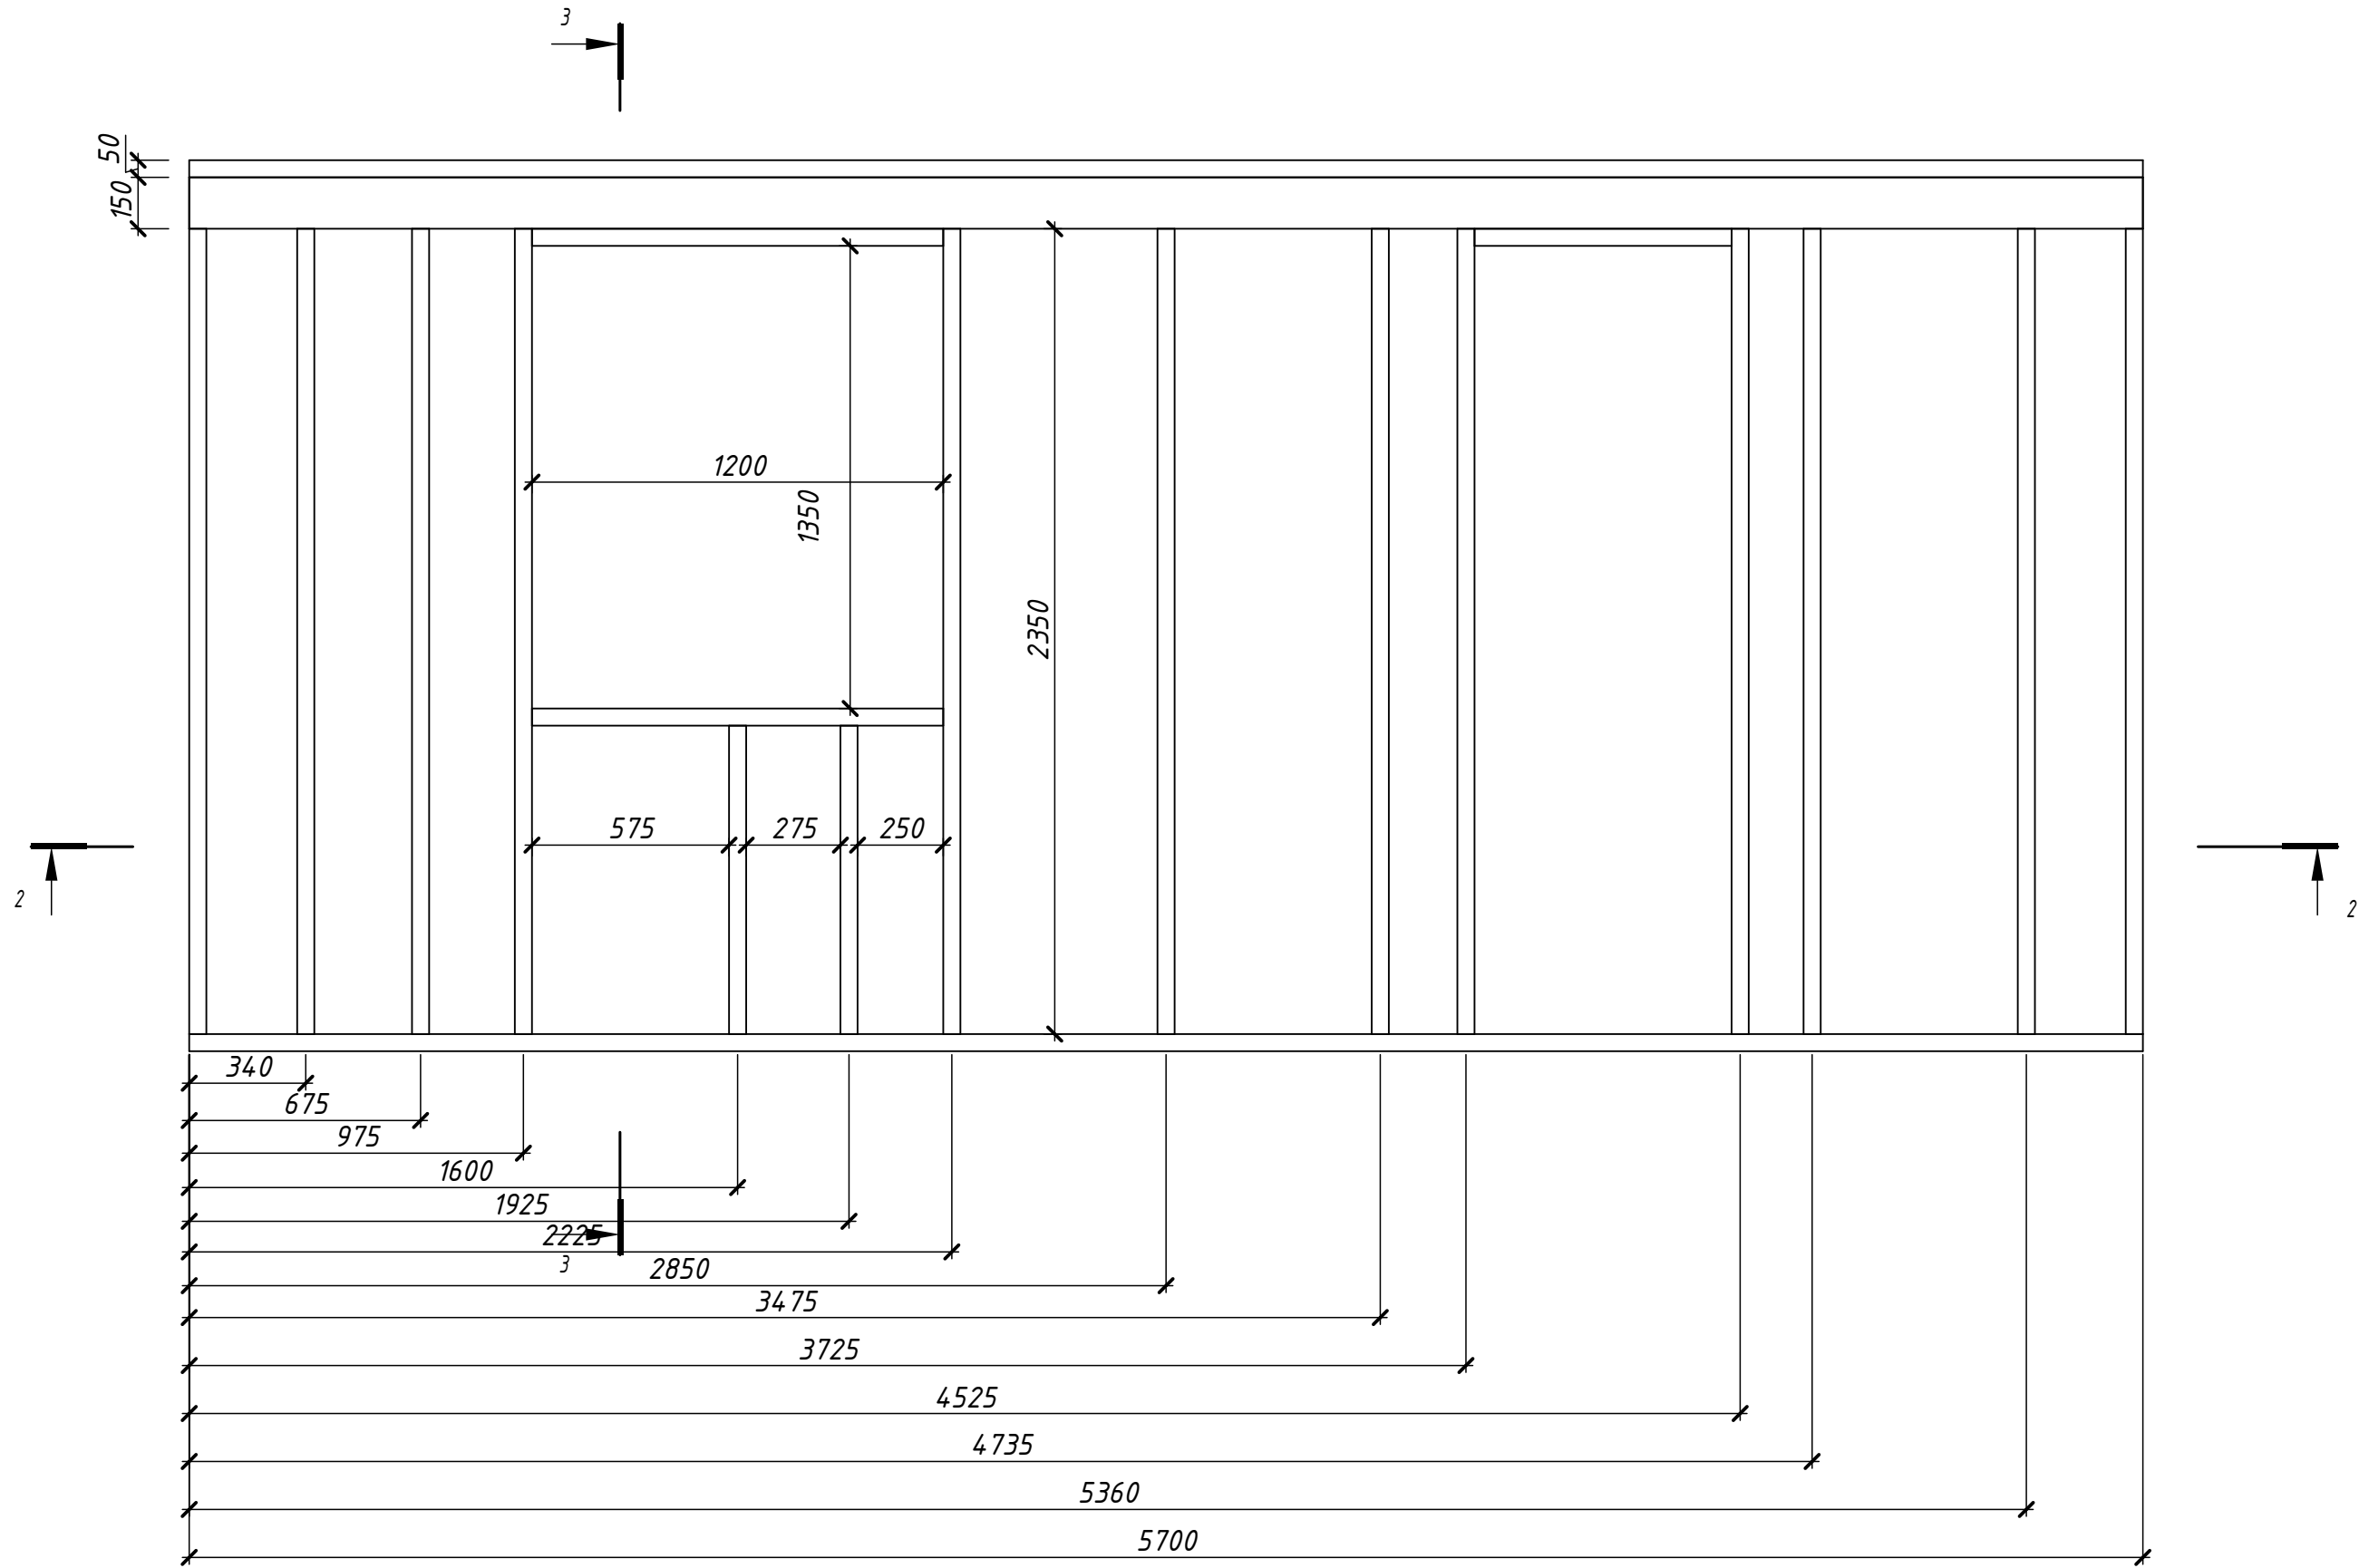


Раскрой. Стена-4			
Поз.	Наименование	Размер.мм	Колич .шт
1	Лежень	5700x150x50	3
2	Стойка	2500x150x50	12
3	Стойка	900x150x50	2
4	Балка	1200x150x50	2
5	Балка	750x150x50	1

20

Согласовано			
Инв. № подл.	Взам. инв. №	Подп. и дата	

№ проекта -						
Россия, г.Кемерово						
Изм.	Кол.уч.	Лист	№ док.	Подпись	Дата	
						Проект каркасного дома
						Стадия
						КР
						Лист
						10
						Листов
						Раскрой стена 4


Согласовано			
Инв. № подл.	Подп. и дата	Взам. инв. №	

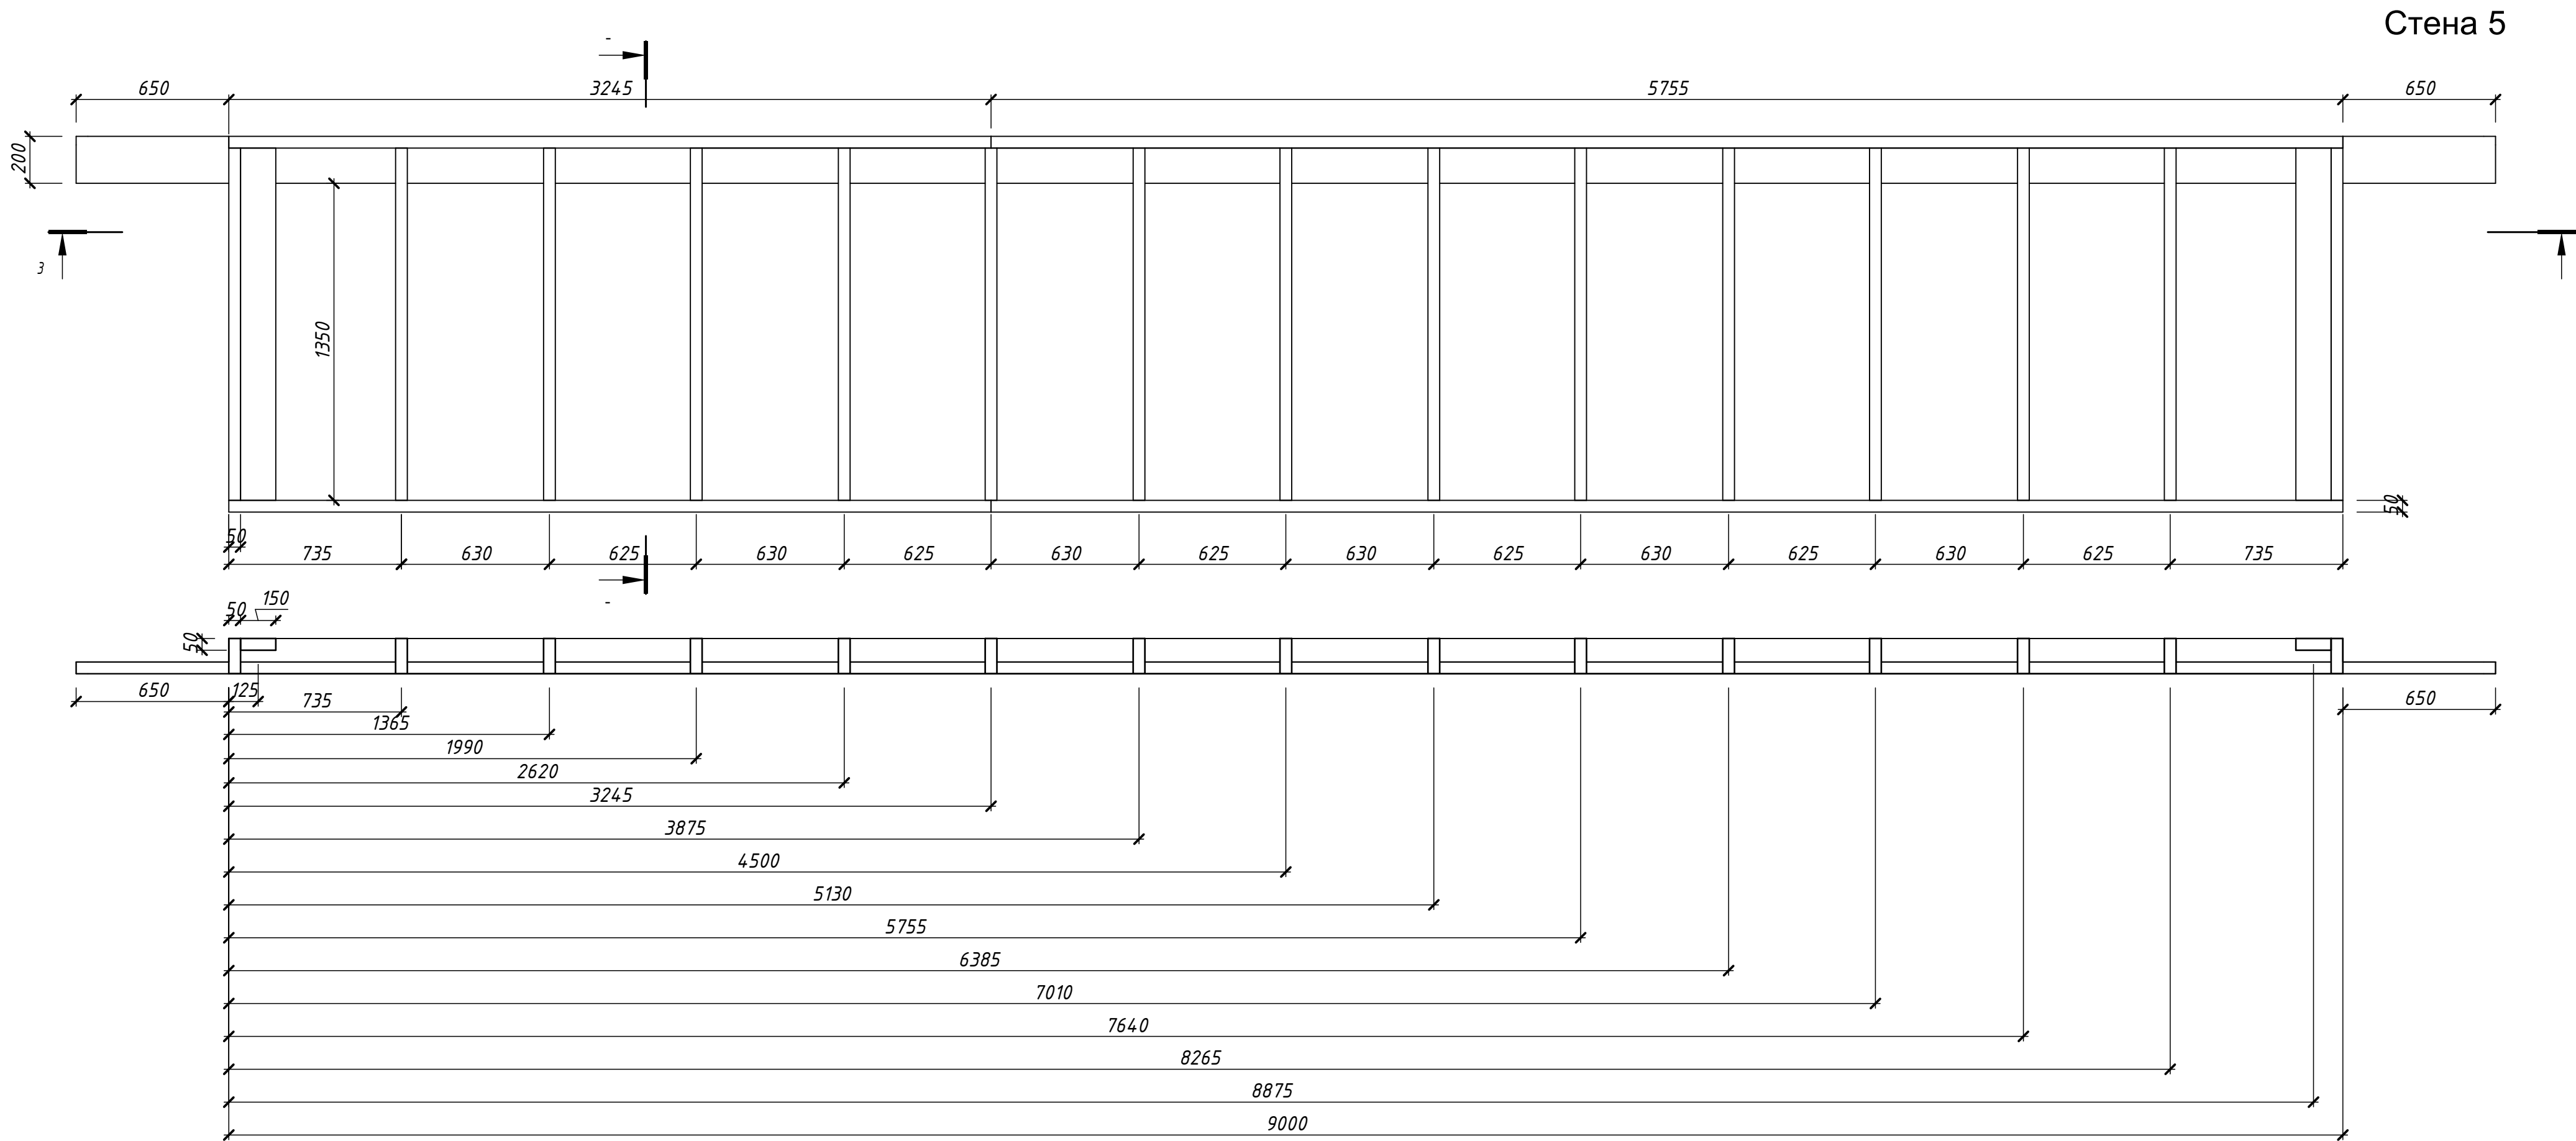


Раскрой. Стена -5			
Поз.	Наименование	Размер.мм	Колич.шт
1	Лежень	5755x150x50	2
2	Лежень	3245x150x50	2
3	Стойка	1500x150x50	17
4	Ригель	5020x200x50	1
5	Балка	2640x200x50	2

							№ проекта -			
							Россия, г.Кемерово			
Изм.	Кол.уч.	Лист	№ док.	Подпись	Дата		Проект каркасного дома	Стадия	Лист	Листов
								КР	12	
							Раскрой. Стена 5			

Стена 6.1

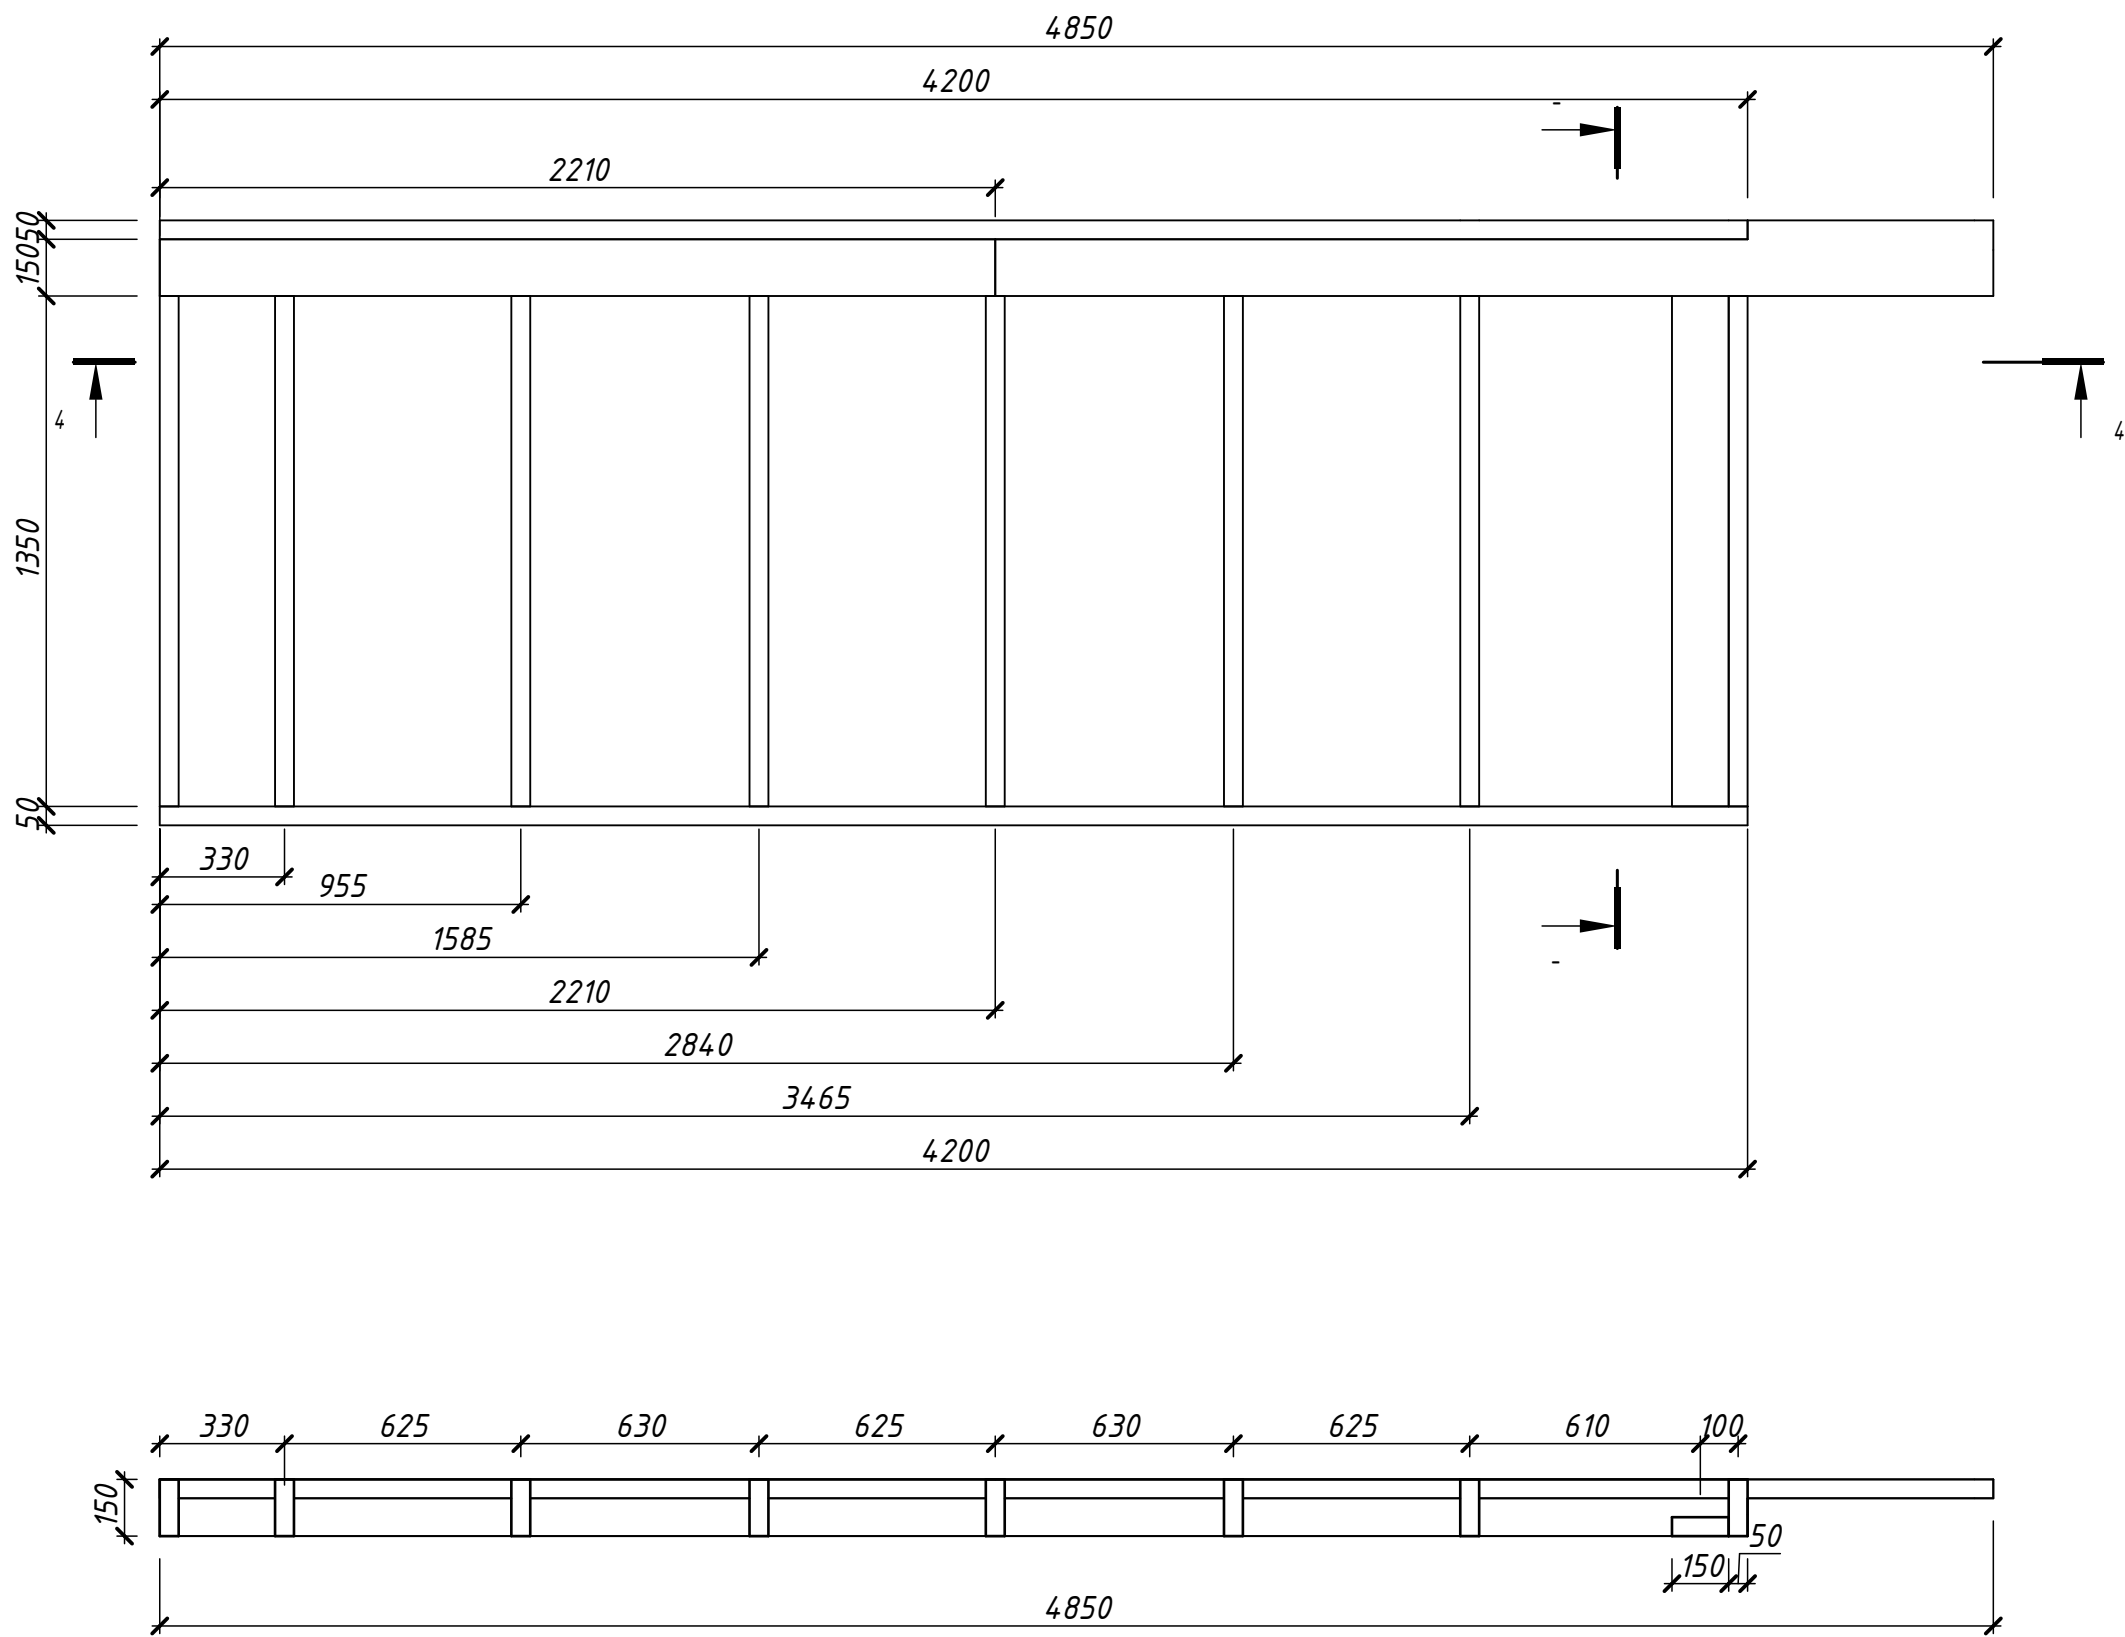

Стена 6.2

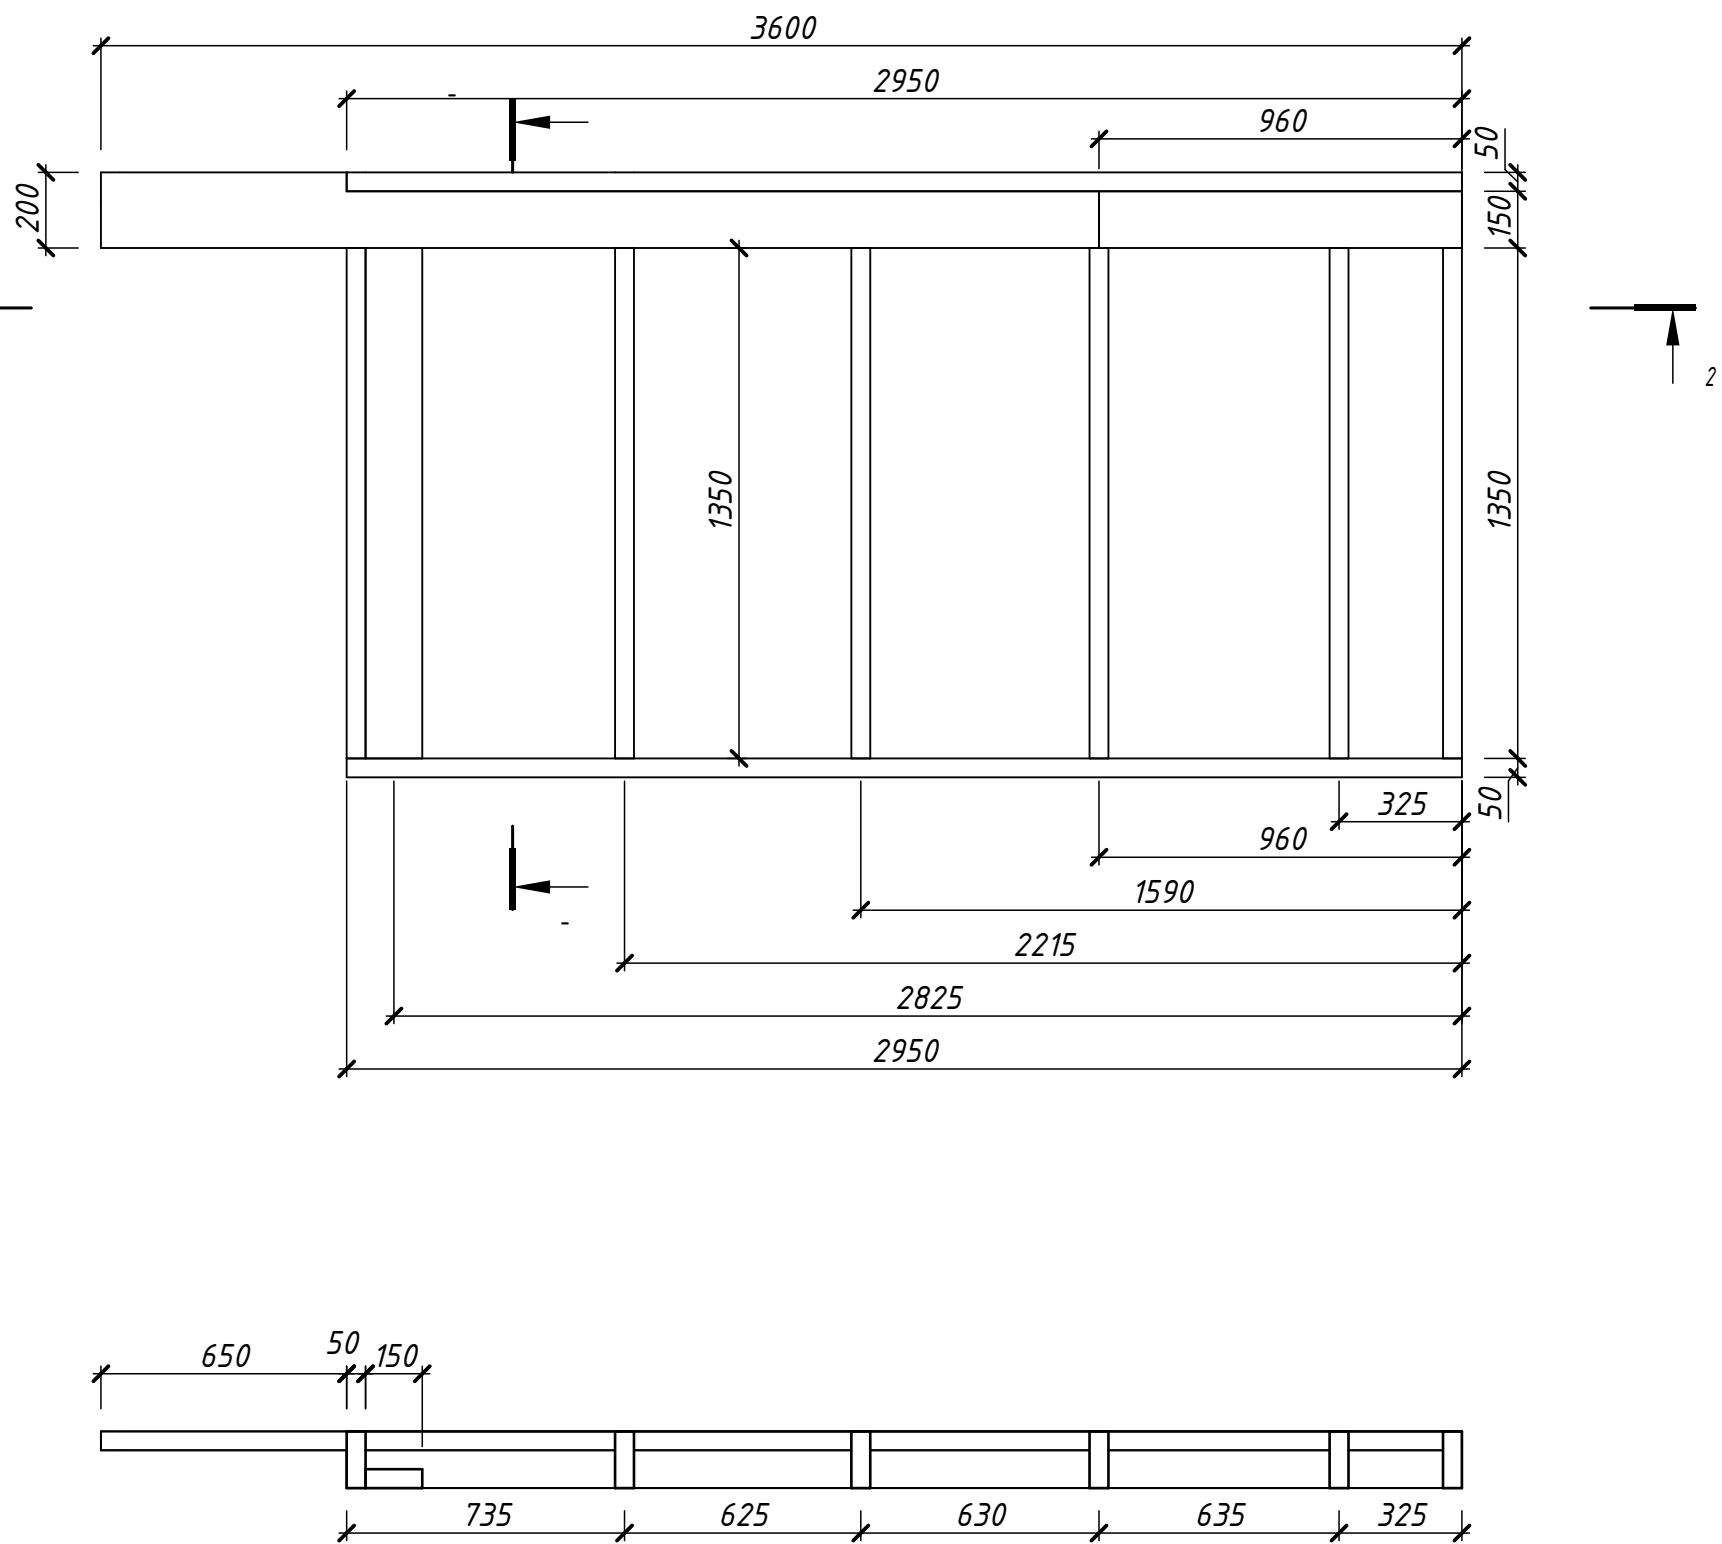

Раскрой. Стена-6.1

Поз.	Наименование	Размер.мм	Колич. .шт
1	Лежень	2950x150x50	2
2	Ригель	960x200x50	1
3	Стойка	1500x150x50	7
4	Балка	2640x200x50	1

Раскрой. Стена-6.2

Поз.	Наименование	Размер.мм	Колич. .шт
1	Лежень	4200x150x50	2
2	Ригель	2210x200x50	1
3	Стойка	1500x150x50	9
4	Балка	2640x200x50	1

№ проекта -

Россия, г.Кемерово

Проект каркасного дома

Раскрой. Стена 6.1-6.2

Стадия

КР

Лист

13

Листов



Согласовано

Инв. № подл.

Взам. инв. №



Подп. и дата

			Согласовано				

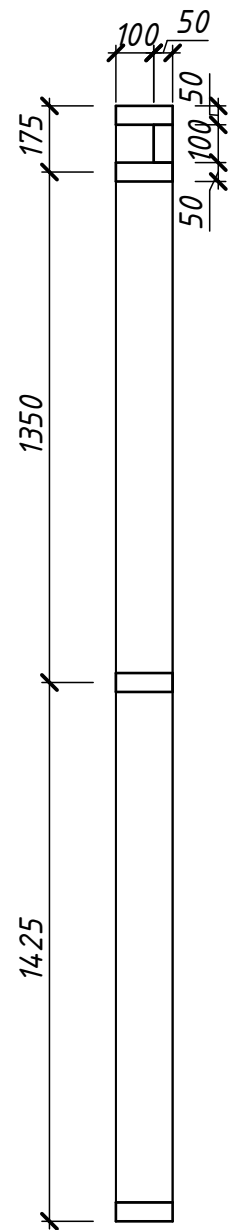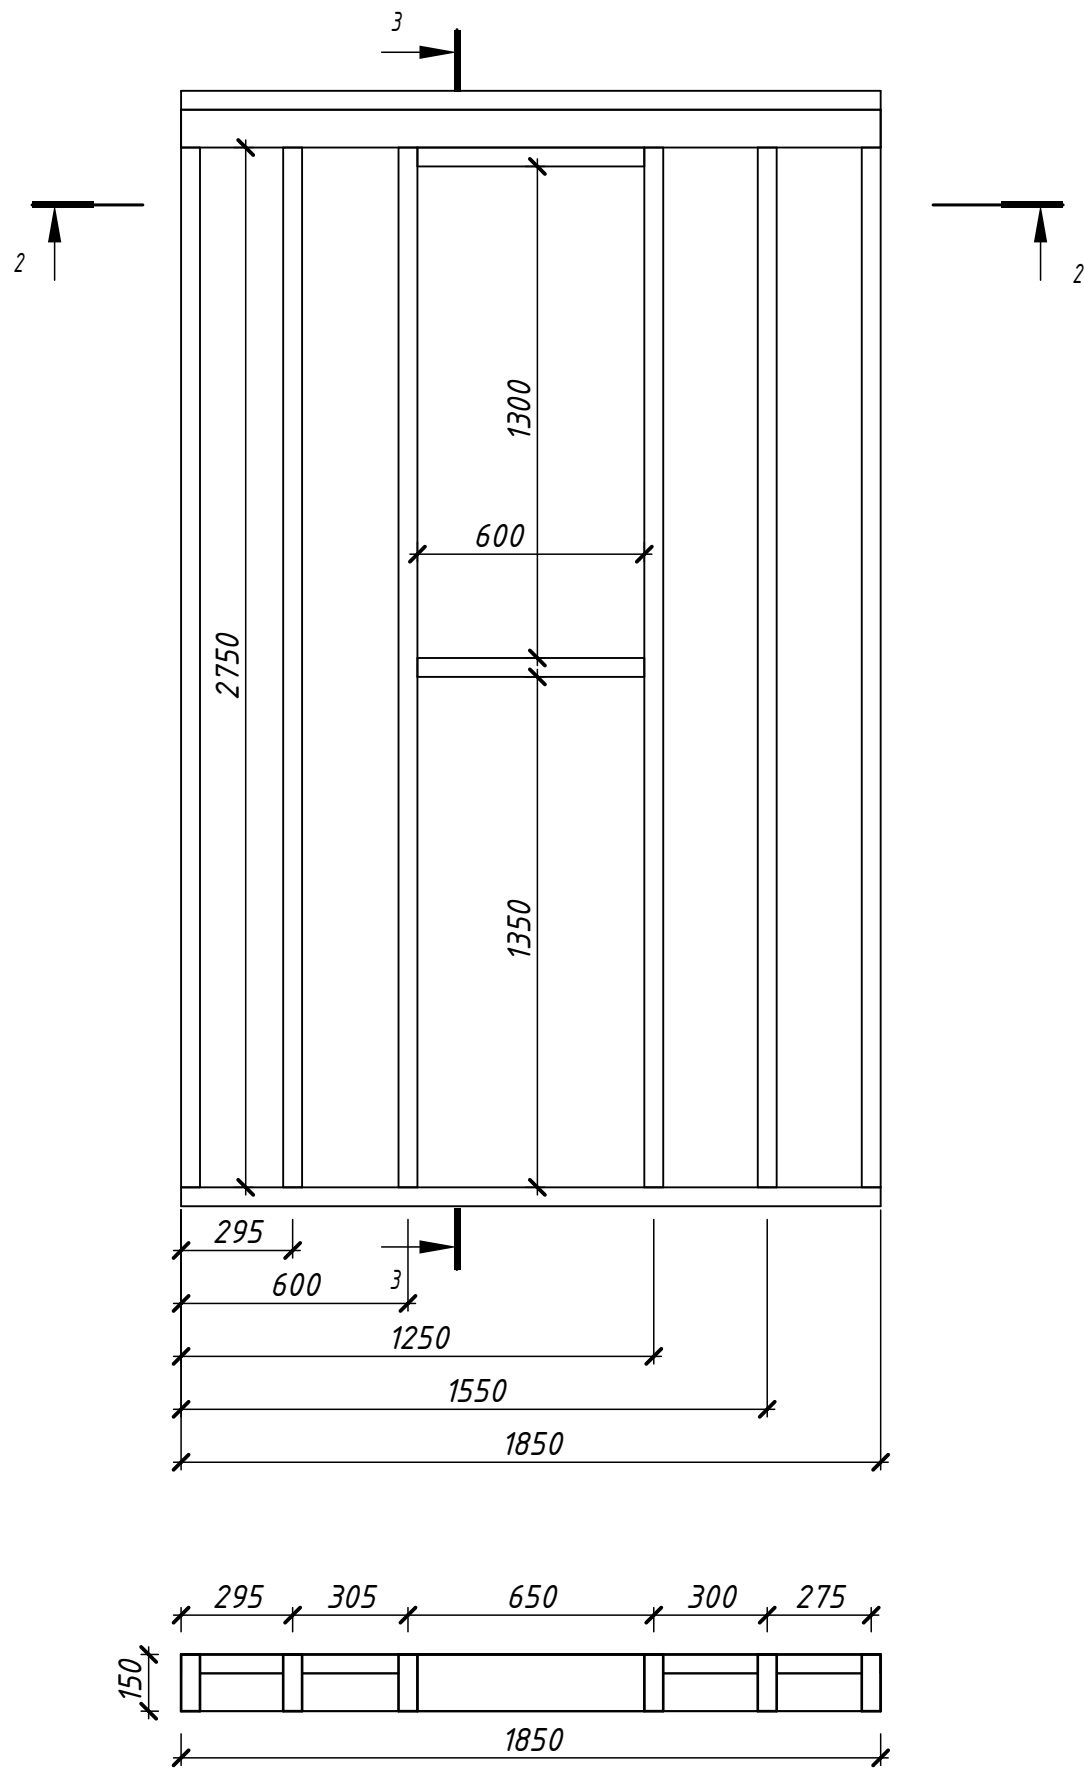

Раскрой. Стена-6.3			
Поз.	Наименование	Размер.мм	Колич. .шт
1	Лежень	1850x150x50	3
2	Стойка	2875x150x50	6
3	Балка	600x150x50	2



						№ проекта -			
						Россия, г. Кемерово			
Изм.	Кол.уч.	Лист	№ док.	Подпись	Дата	Проект каркасного дома	Стадия	Лист	Листов
							КР	14	
							Раскрой. Стена 6.3		

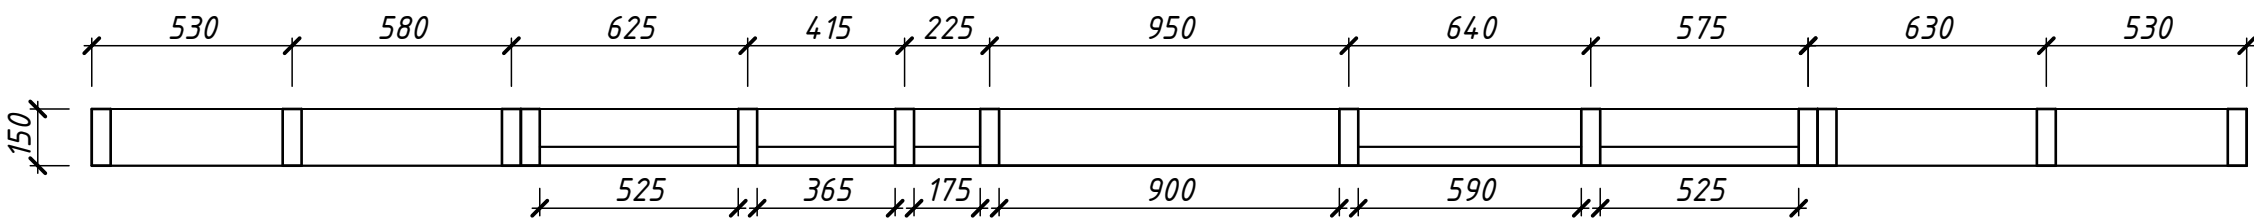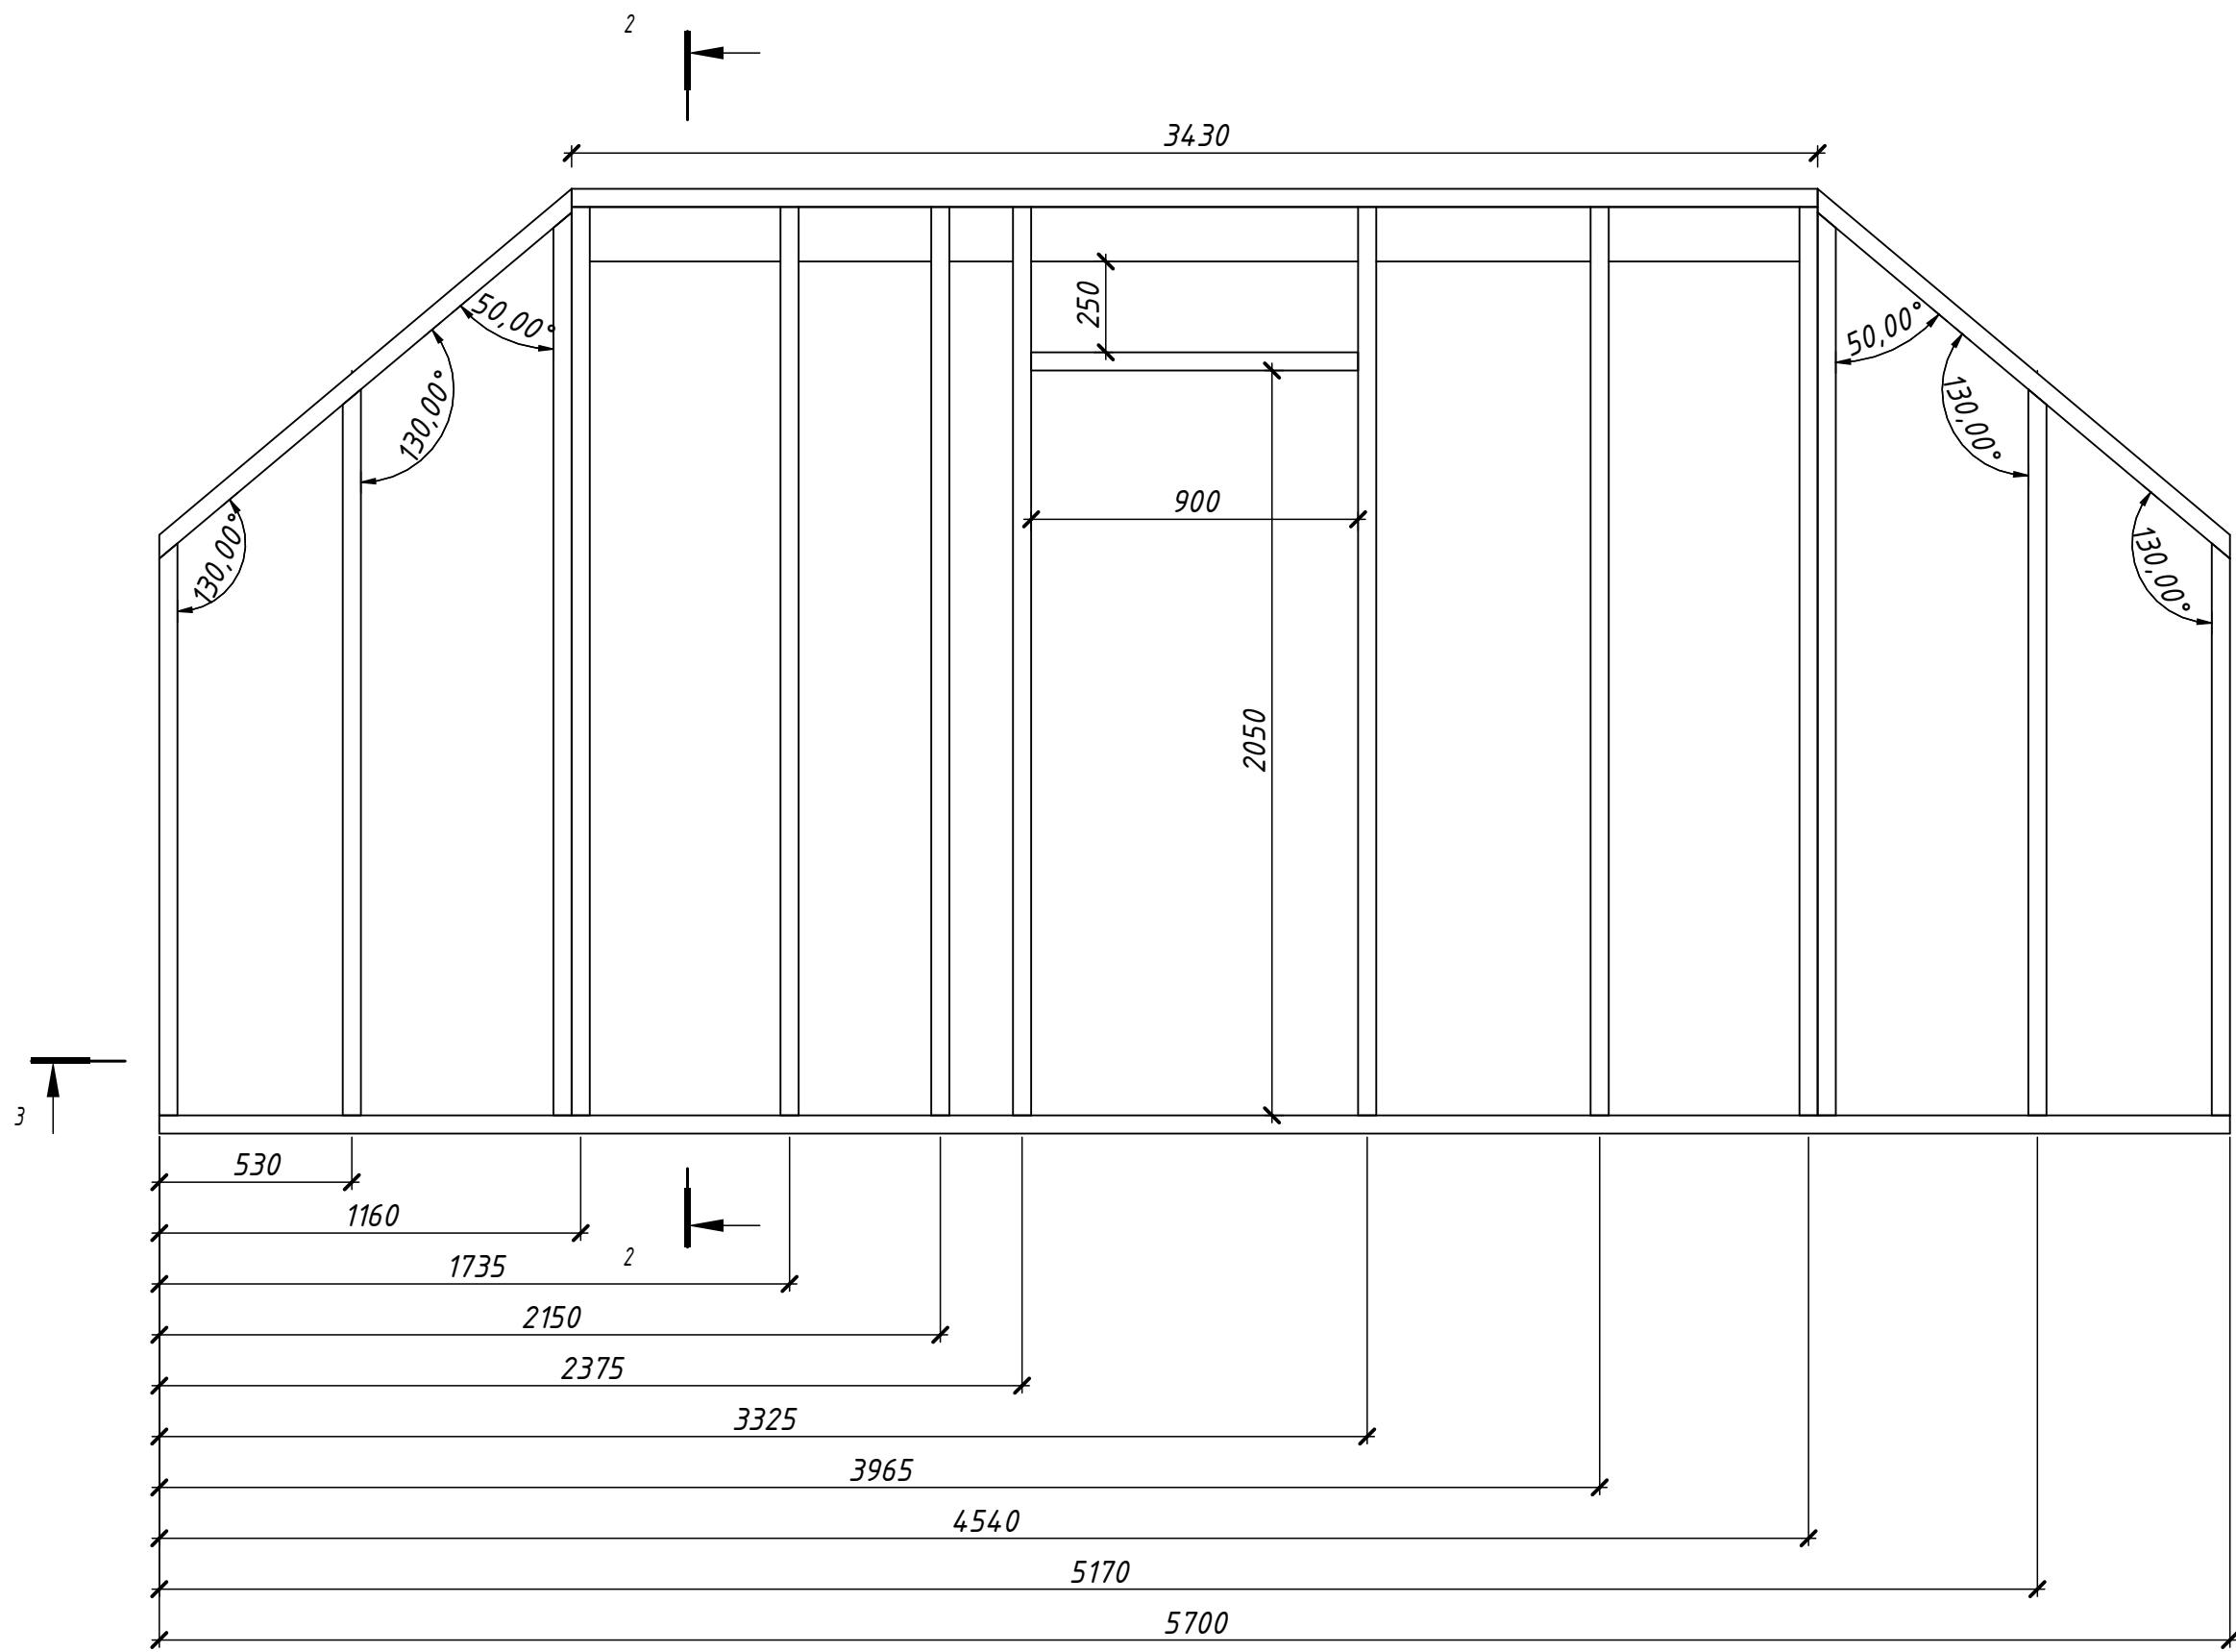

Раскрой. Перегородка 1			
Поз.	Наименование	Размер.мм	Колич. .шт
1	Лежень	5700x150x50	1
2	Лежень	3430x150x50	2
3	Стойка	2500x150x50	7
4	Балка	900x150x50	1
5	Стойка	2485x150x50	2
6	Стойка	2000x150x50	2
7	Стойка	1575x150x50	2
8	Балка	1525x150x50	2



						№ проекта -				
						Россия, г. Кемерово				
Изм.	Кол.уч	Лист	№ док.	Подпись	Дата	Проект каркасного дома		Стадия	Лист	Листов
								КР	15	
						Раскрой. Перегородка-1				

Согласовано			
Инв. № подл.	Подп. и дата	Взам. инв. №	

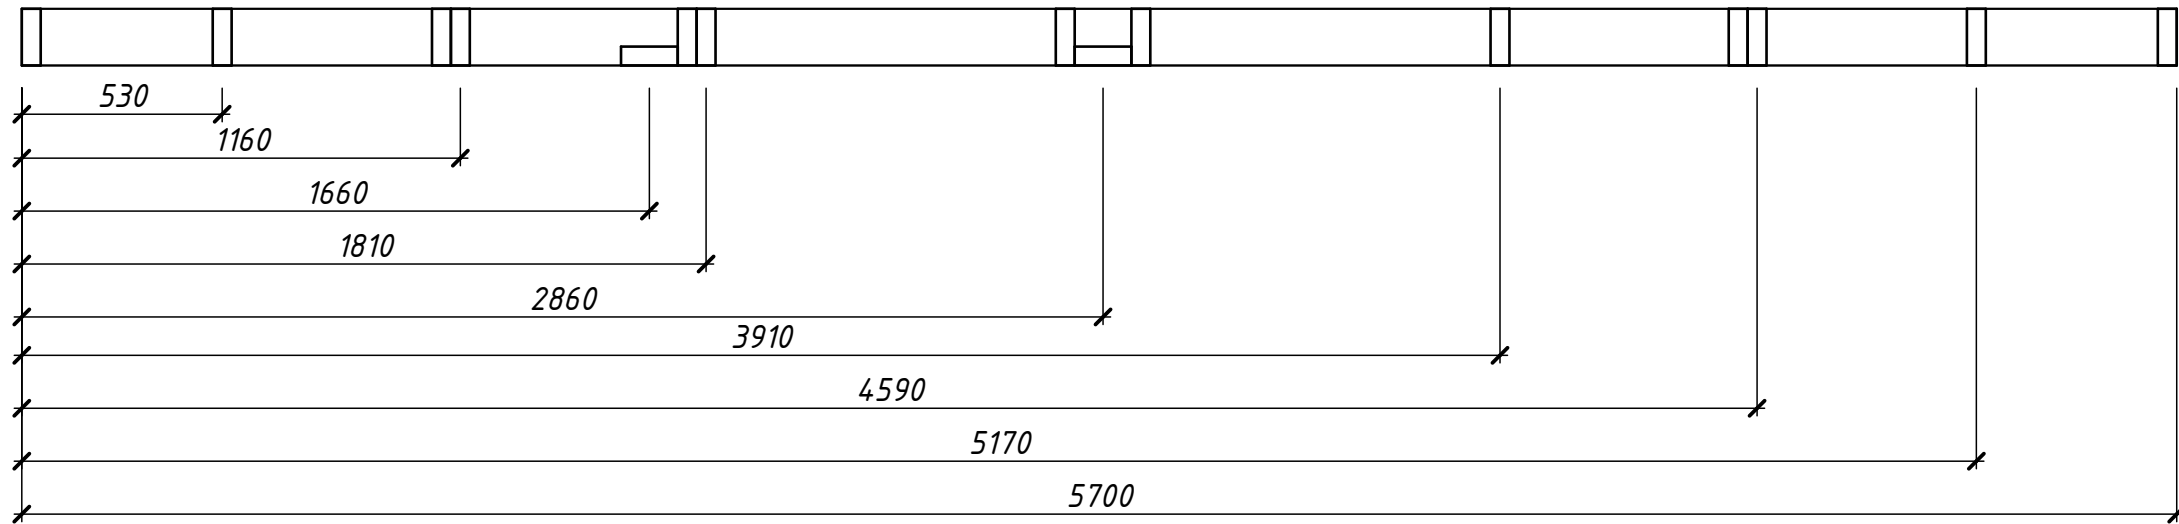
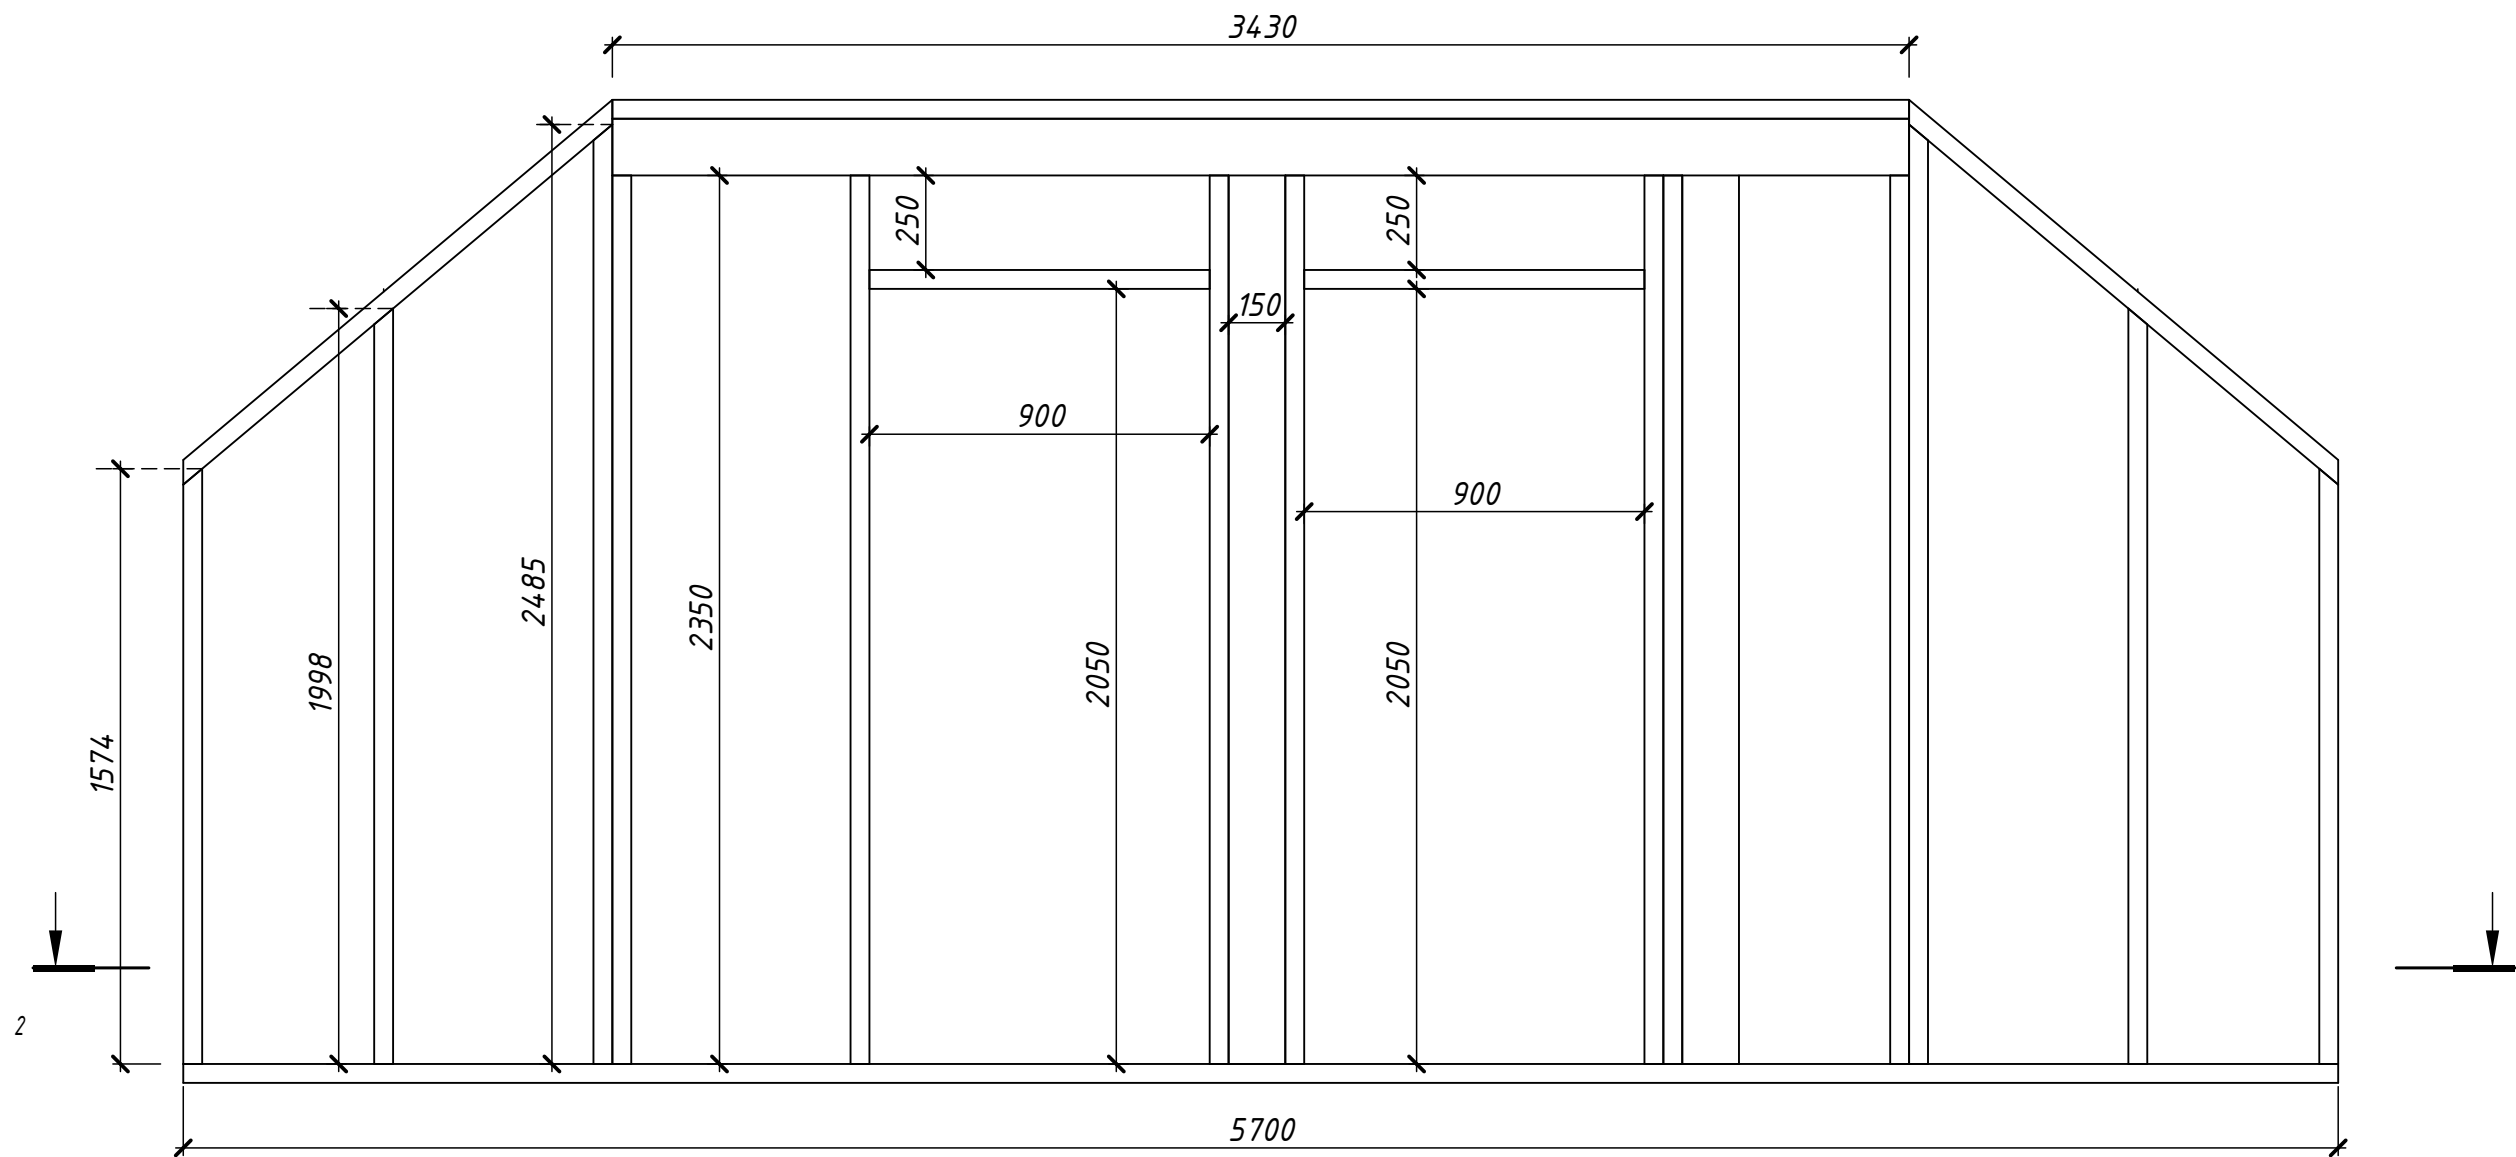


Раскрой. Перегородка 2			
Поз.	Наименование	Размер.мм	Колич. .шт
1	Лежень	5700x150x50	1
2	Лежень	3430x150x50	2
3	Стойка	2500x150x50	9
4	Балка	900x150x50	2
5	Стойка	2485x150x50	2
6	Стойка	2000x150x50	2
7	Стойка	1575x150x50	2
8	Балка	1525x150x50	2

№ проекта -							
Россия, г. Кемерово							
Изм.	Кол.уч.	Лист	№ док.	Подпись	Дата	Проект каркасного дома	Стадия КР
						16	Листов
Раскрой. Перегородка-2							

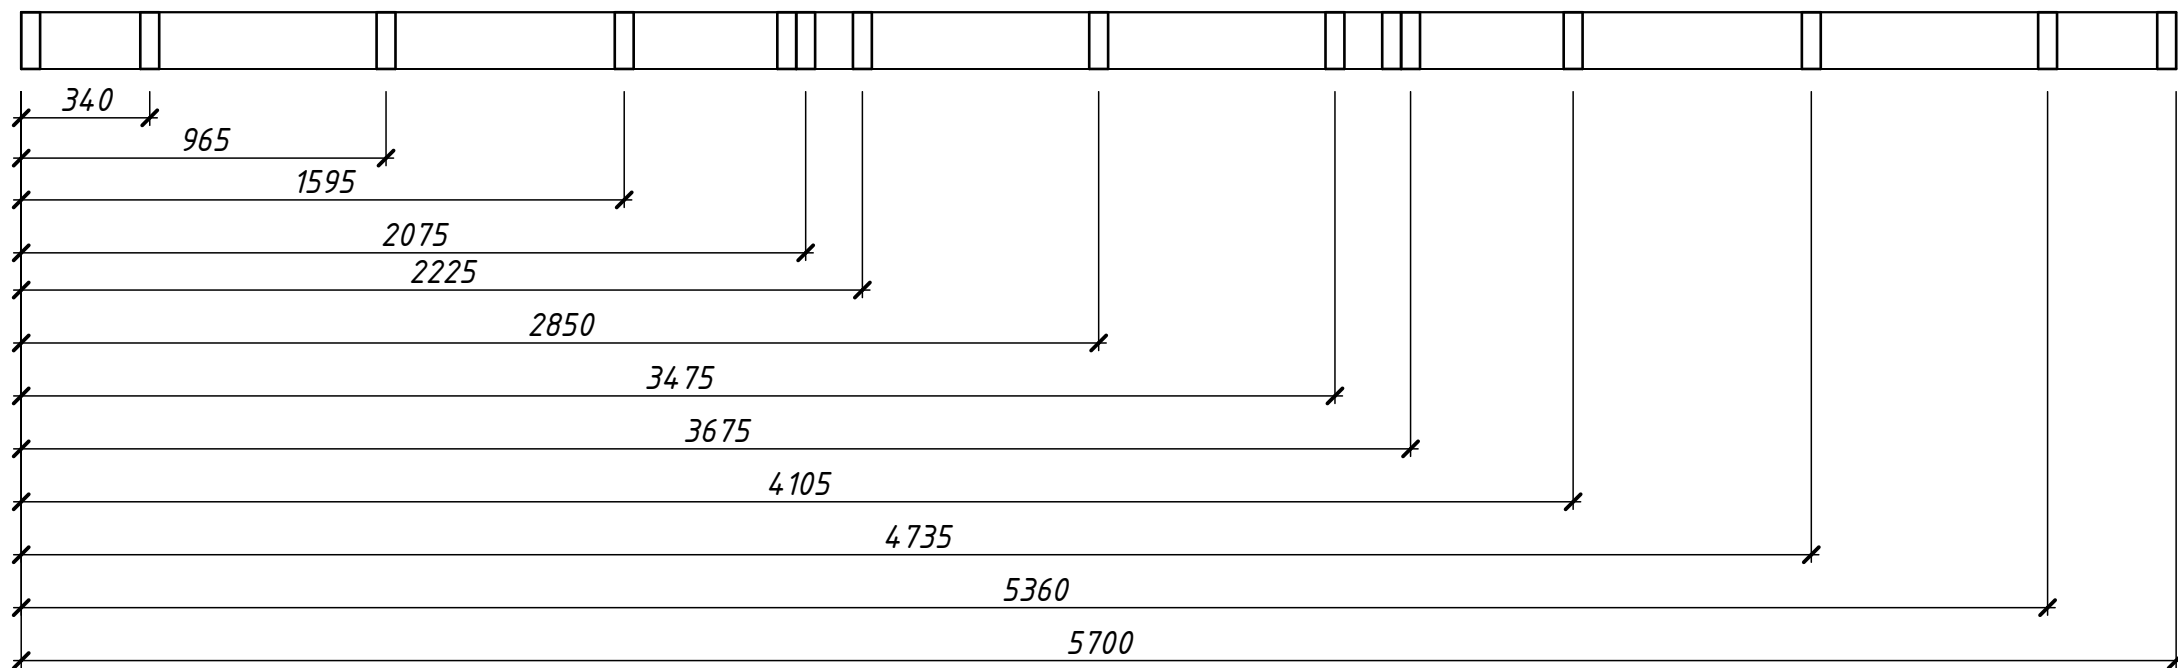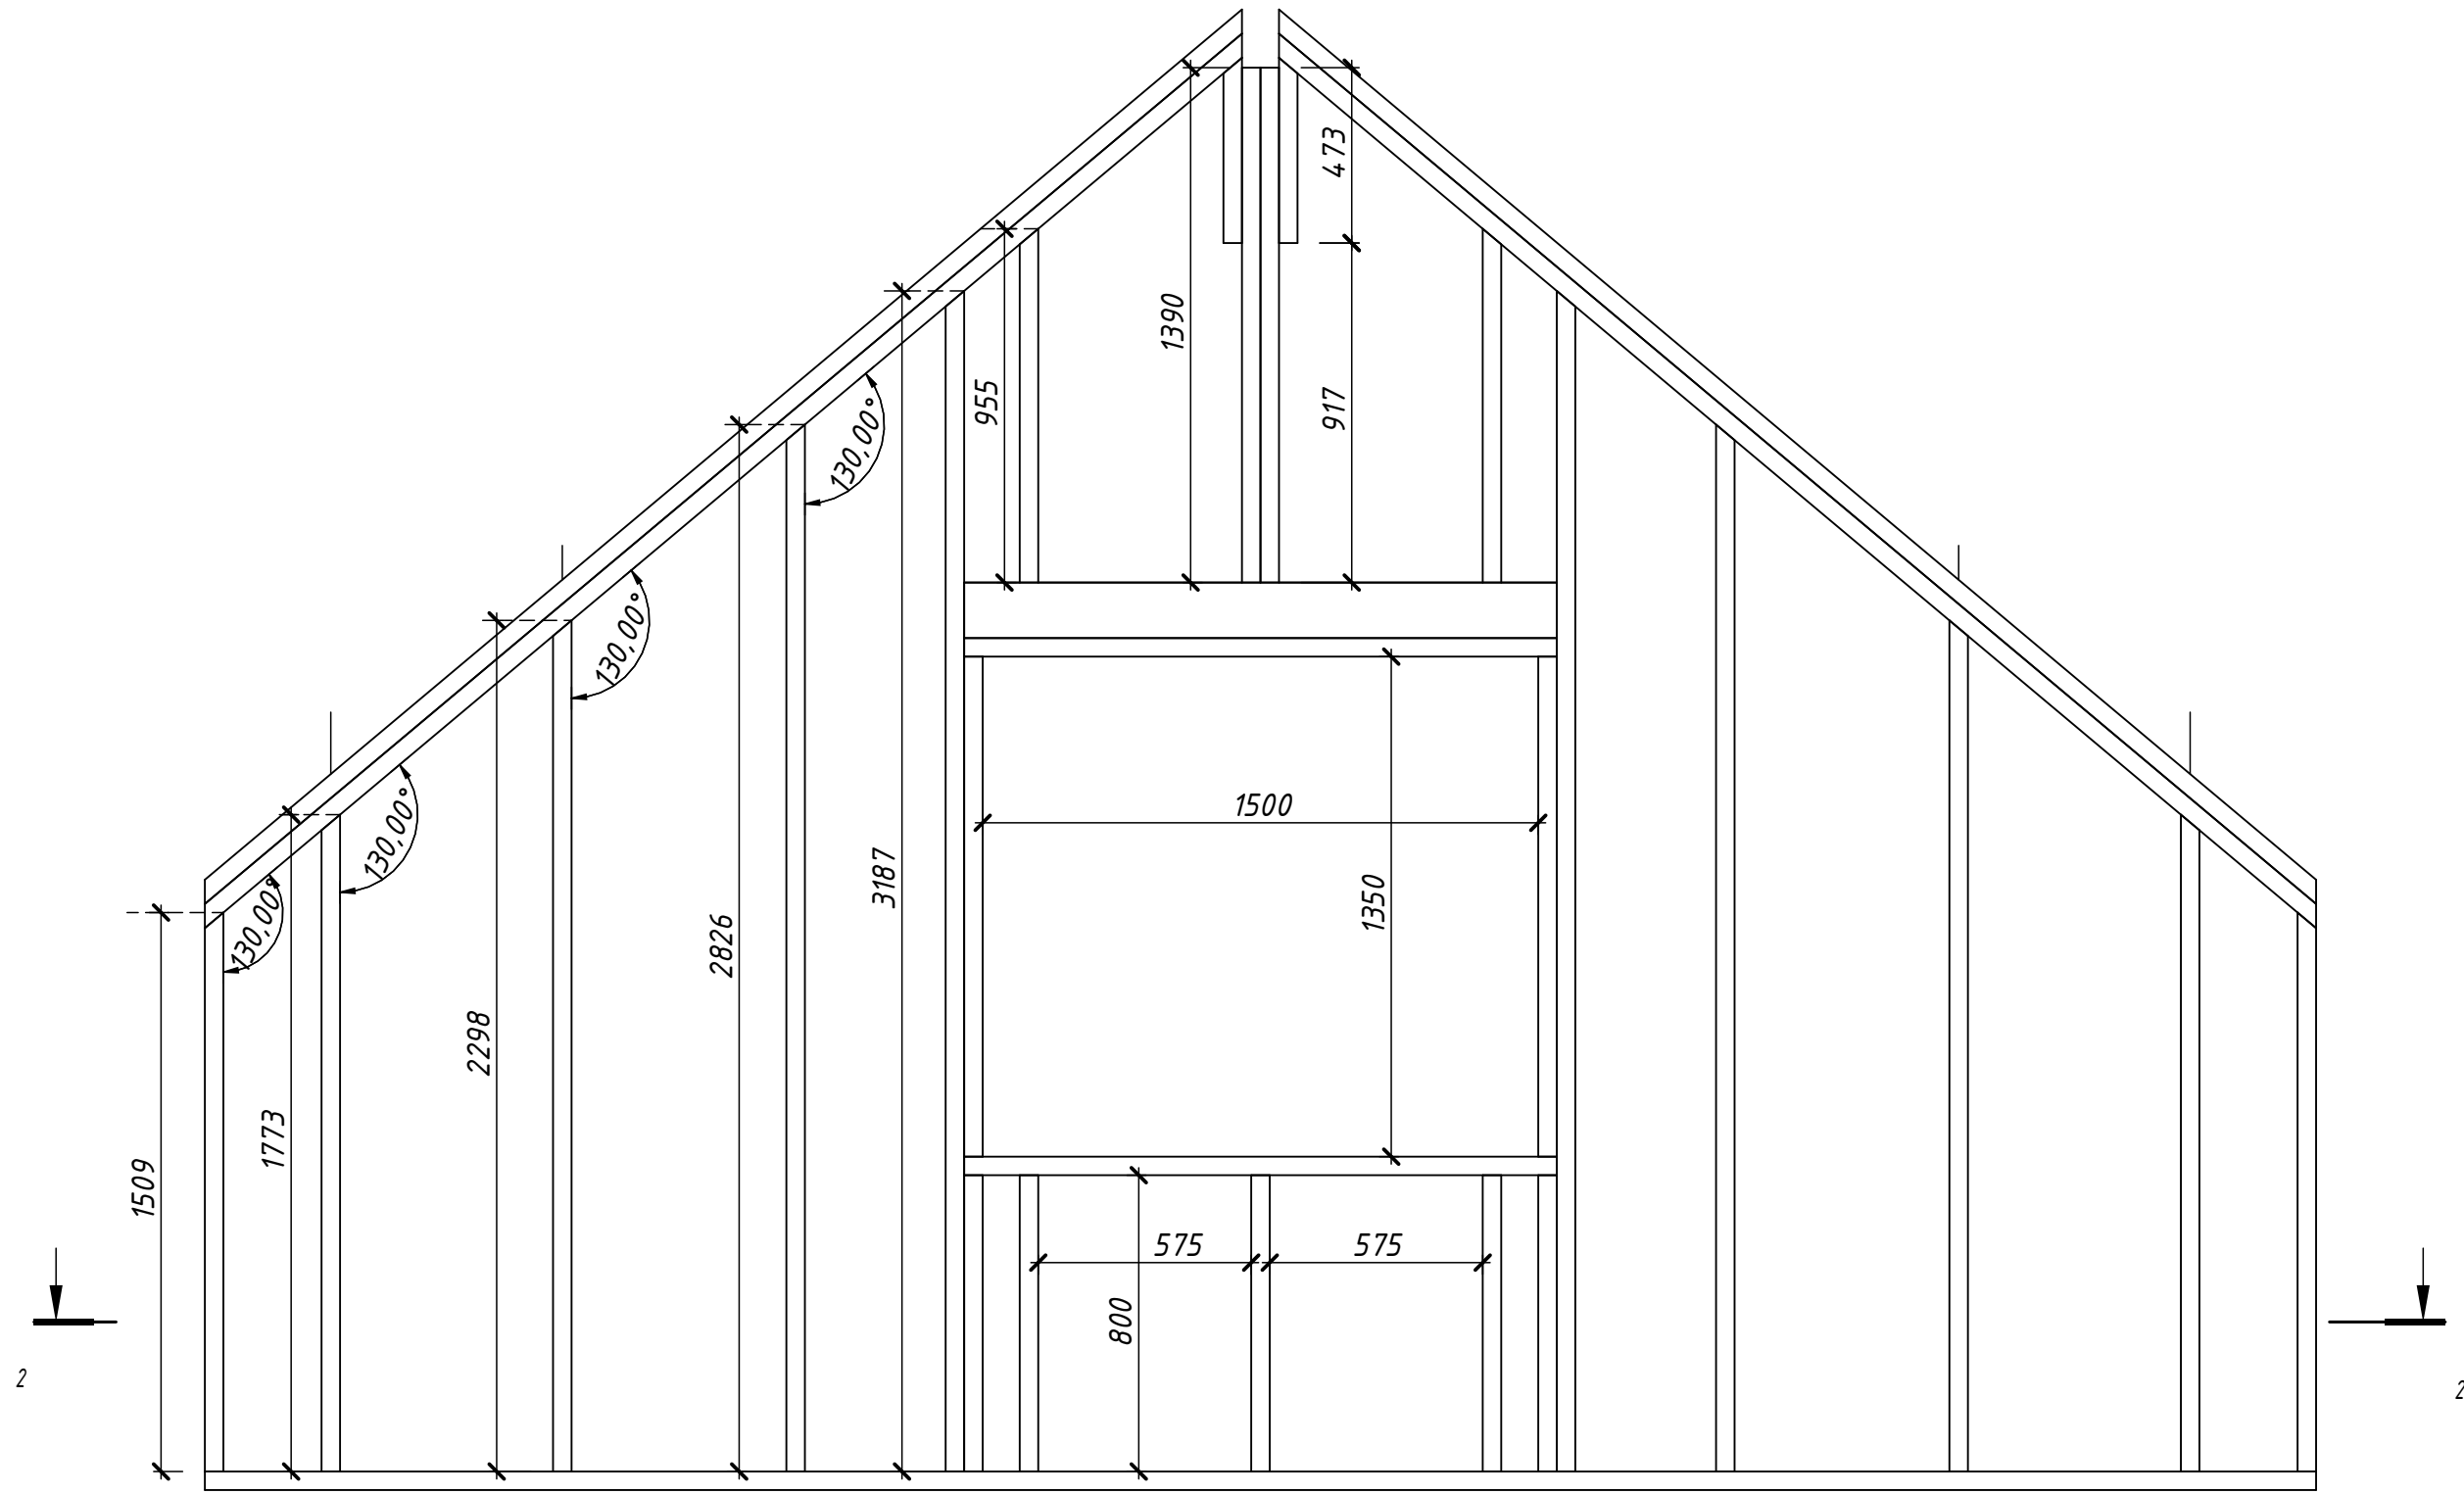

Раскрой. Фронтон 1			
Поз.	Наименование	Размер.мм	Колич.шт
1	Лежень	5700x150x50	1
2	Лежень	2825x200x50	5
2	Лежень	3695x150x50	4
2	Лежень	4860x200x50	34
3	Стойка	3185x150x50	2
4	Стойка	2825x150x50	2
5	Стойка	2300x150x50	2
6	Стойка	1775x150x50	2
7	Стойка	1510x150x50	2
8	Стойка	800x150x50	5
9	Балка	1600x150x50	4
10	Стойка	1350x150x50	2
11	Стойка	1390x150x50	2
12	Стойка	955x150x50	2
13	Проставка	500x150x50	2

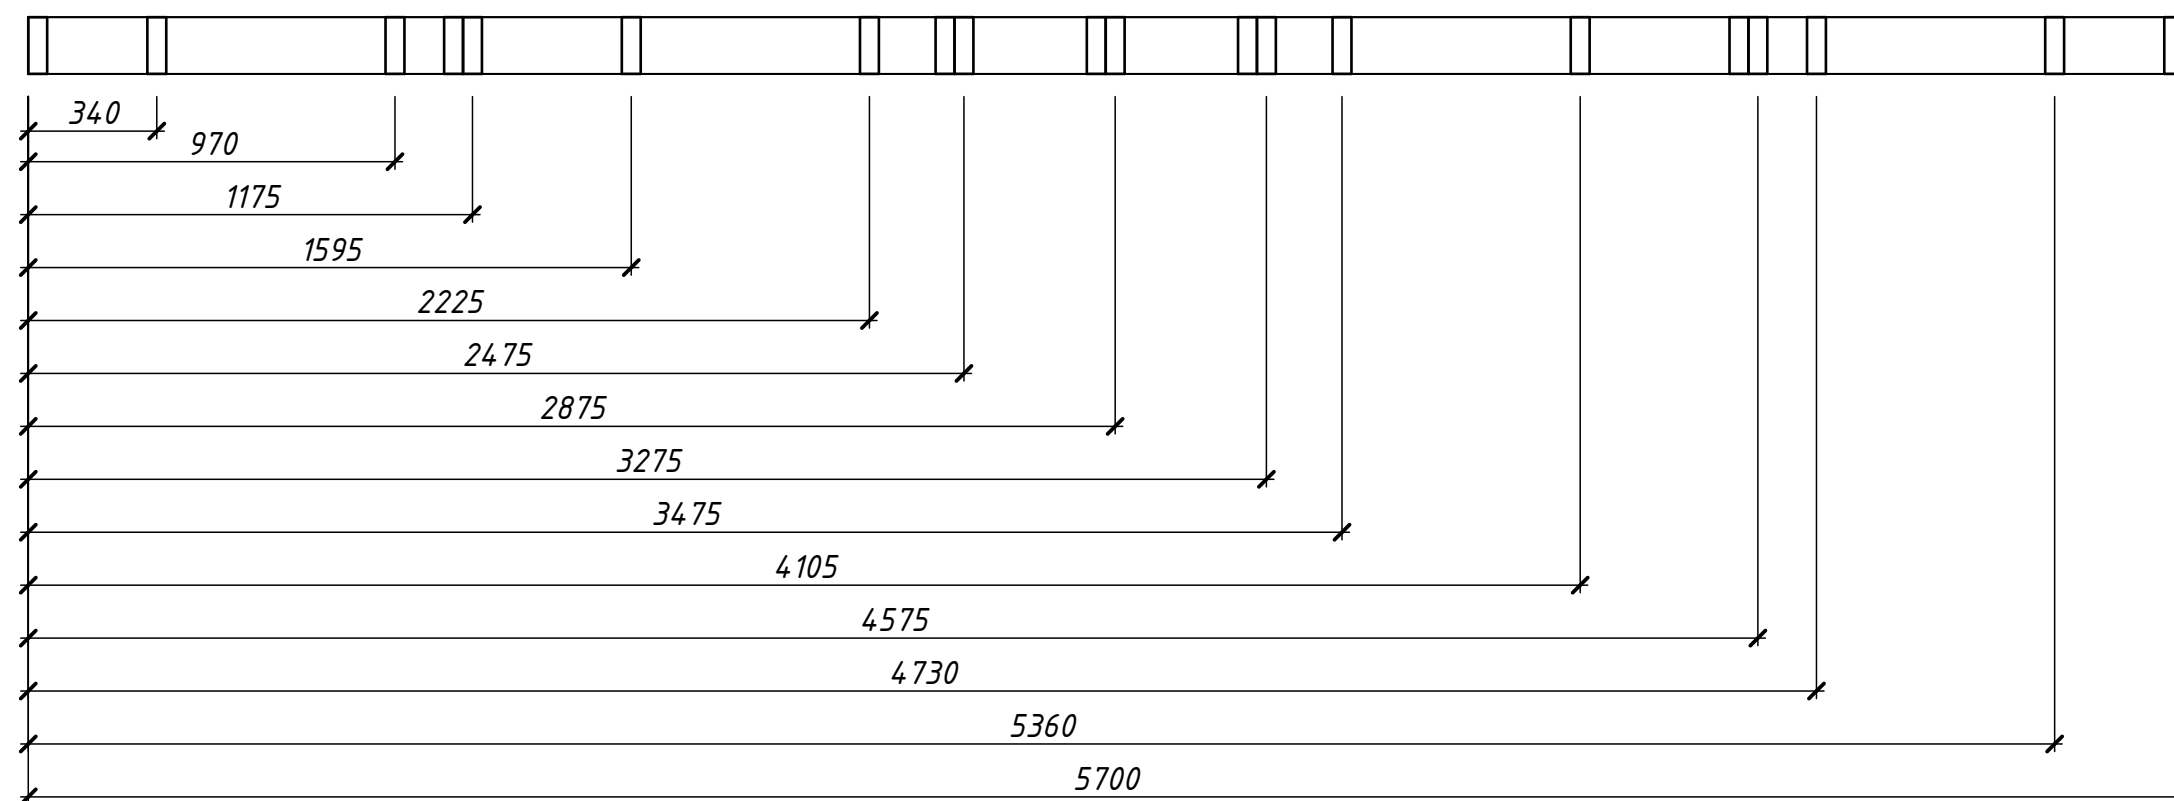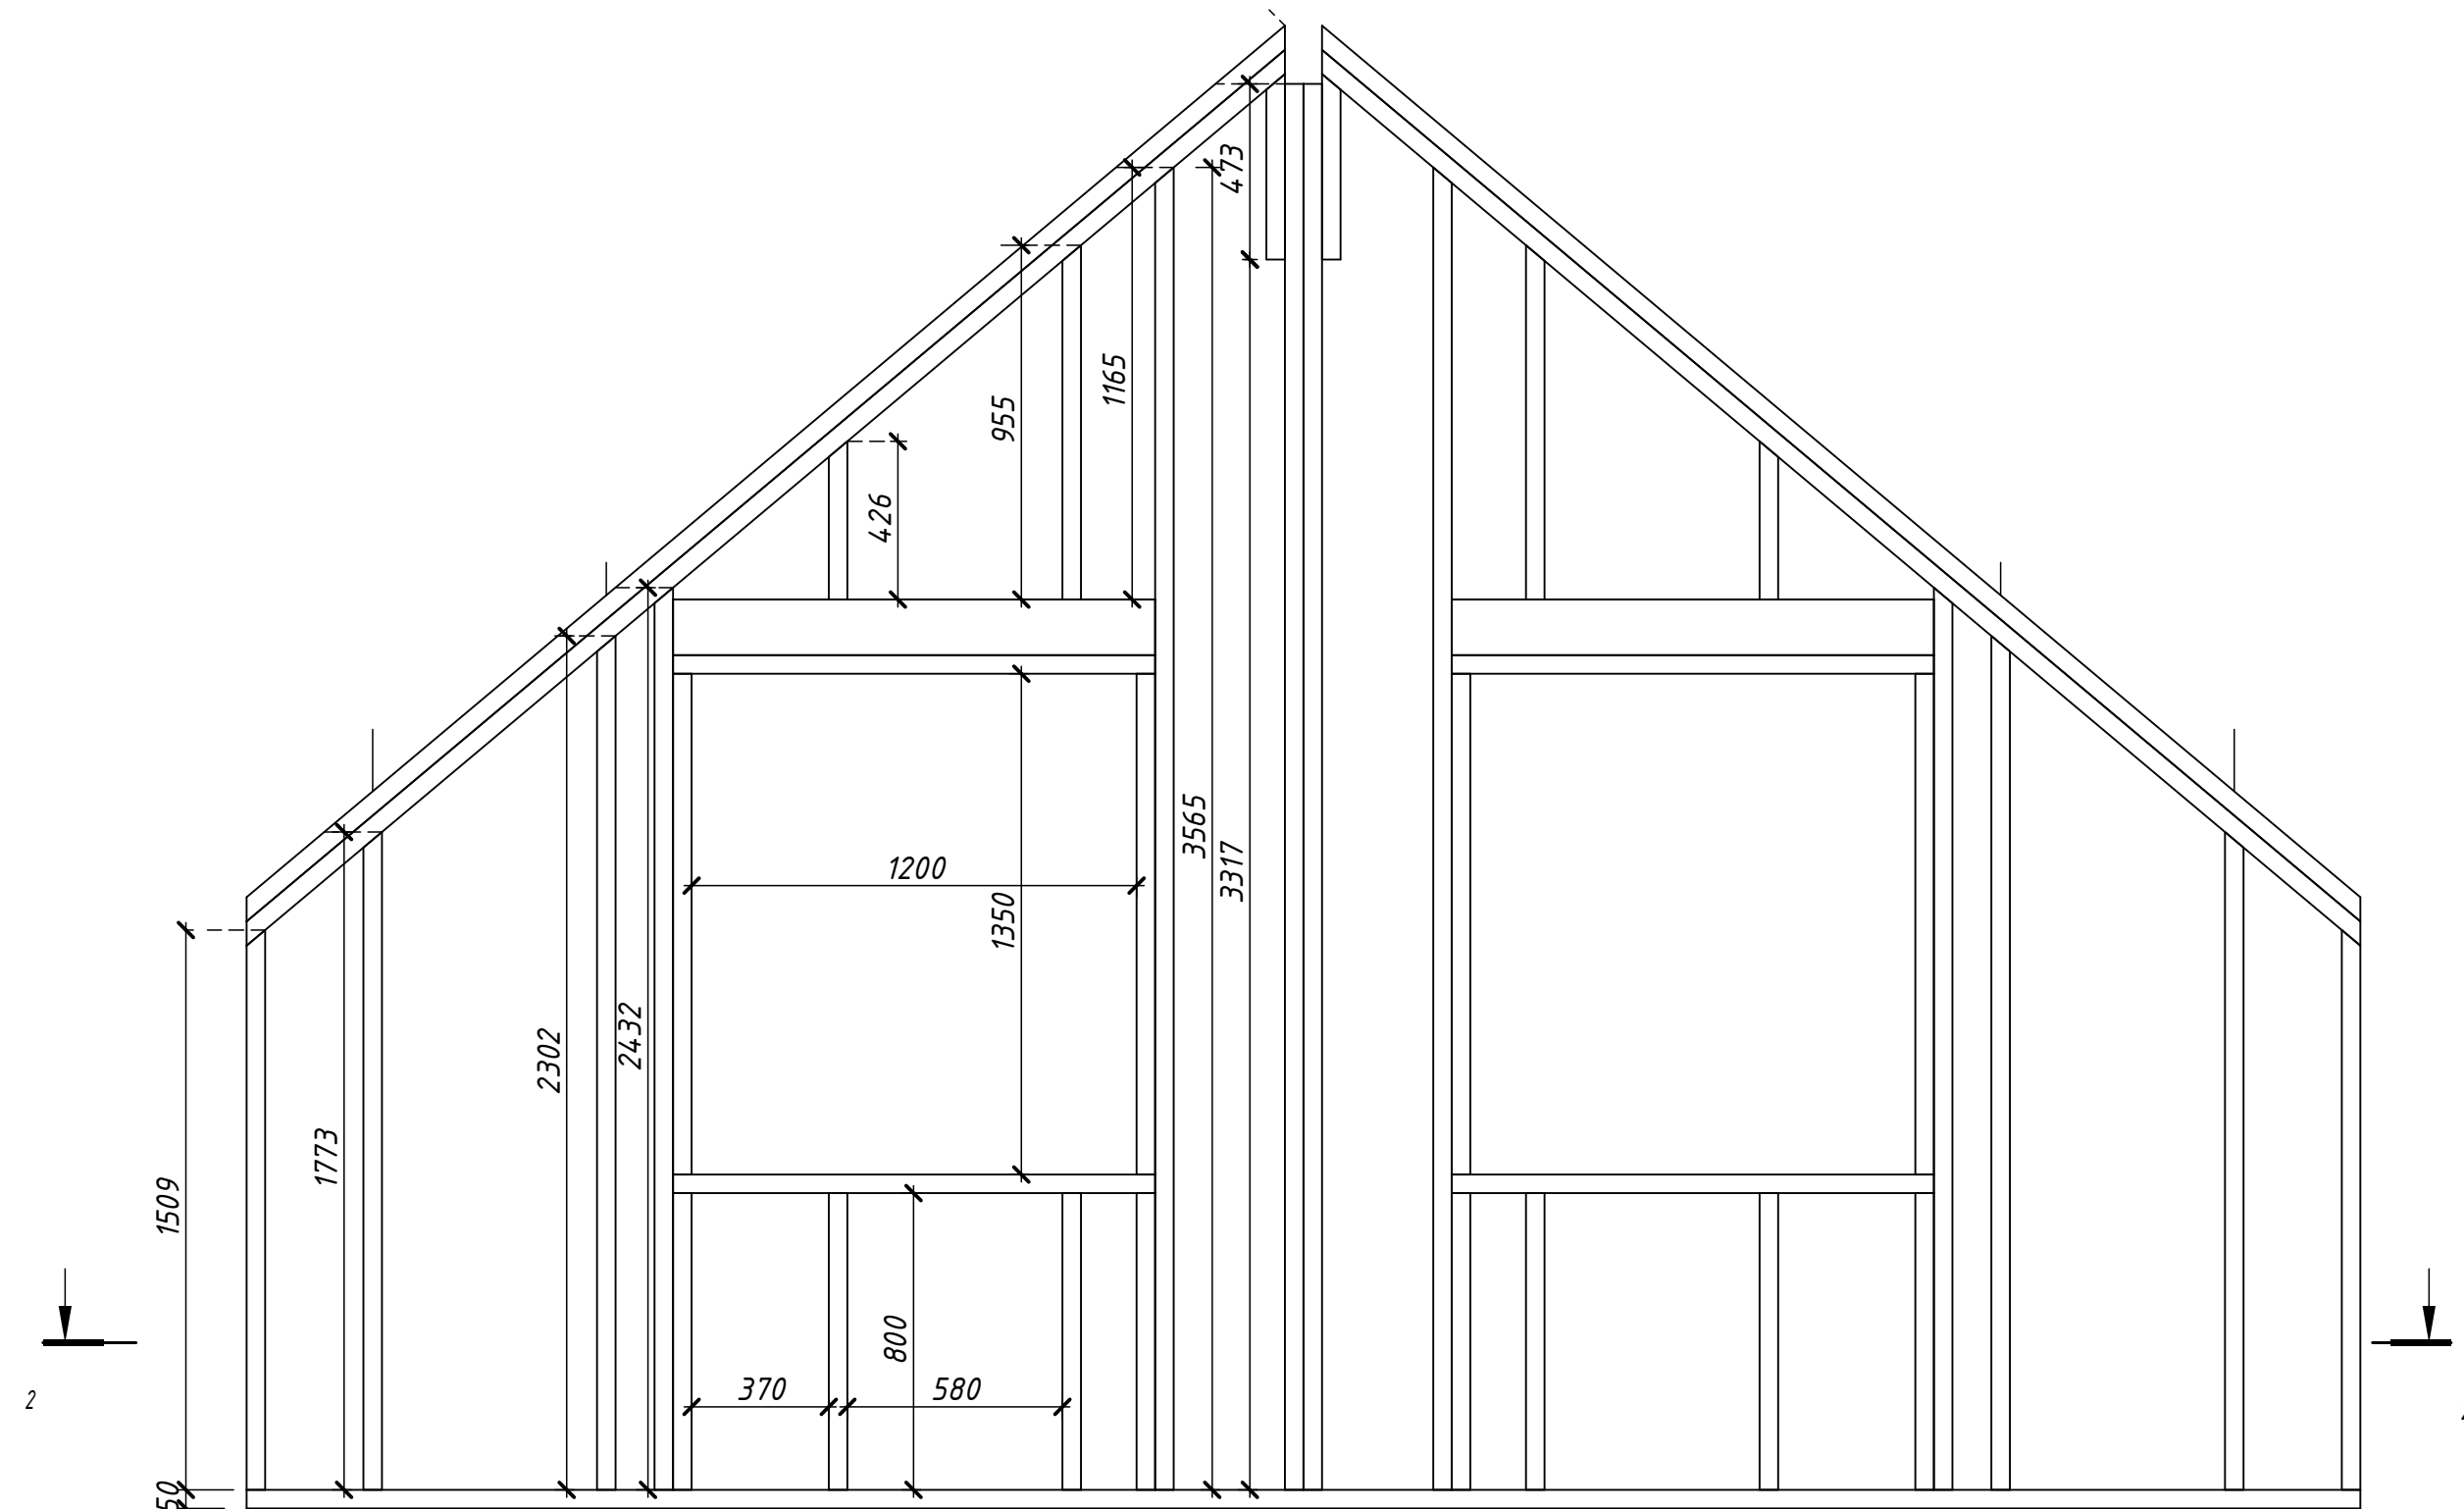[illegible]

Раскрой. Фронтон 2			
Поз.	Наименование	Размер.мм	Колич. шт
1	Лежень	5700x150x50	1
2	Лежень	3695x150x50	4
3	Стойка	3790x150x50	2
4	Стойка	3565x150x50	2
5	Стойка	2430x150x50	2
6	Стойка	2300x150x50	2
7	Стойка	1775x150x50	2
8	Стойка	1510x150x50	2
9	Стойка	800x150x50	8
10	Балка	1300x150x50	8
11	Стойка	1350x150x50	4
12	Стойка	955x150x50	2
13	Стойка	425x150x50	2
14	Проставка	500x150x50	2

						№ проекта -				
						Россия, г. Кемерово				
Изм.	Кол.уч	Лист	№ док.	Подпись	Дата	Проект каркасного дома		Стадия	Лист	Листов
								КР	18	
						Раскрой. Фронтон-2				

[illegible]

Раскрой. Верхнее перекрытие			
Поз.	Наименование	Размер.мм	Колич. .шт
1	Фасадная доска	5900x200x50	3
2	Фасадная доска	3100x200x50	1
3	Фасадная доска	4200x200x50	1
4	Фасадная доска	2950x200x50	1
5	Фасадная доска	1700x200x50	2
6	Балка	2150x200x50	2
7	Лага	2825x200x50	10
8	Лага	6075x200x50	10
9	Лага	2850x200x50	4
10	Лага	4100x200x50	4
11	Лага	4050x200x50	1
12	Мостик	400x200x50	69
12	Мостик	3500x200x50	2
12	Мостик	4052x200x50	13
13	Мостик	350x200x50	7
14	Мостик	320x200x50	11
15	Мостик	270x200x50	1
16	Мостик	175x200x50	6

[illegible]


						<i>№ проекта -</i>			
						<i>Россия, г. Кемерово</i>			
<i>Изм.</i>	<i>Кол.уч</i>	<i>Лист</i>	<i>№ док.</i>	<i>Подпись</i>	<i>Дата</i>				
						<i>Проект каркасного дома</i>	<i>Стадия</i>	<i>Лист</i>	<i>Листов</i>
							<i>КР</i>	<i>19</i>	
						<i>Раскрой.Верхнее перекрытие</i>			

Согласовано


Взам. инв. №

Подп. и дата

Инв. № подл.

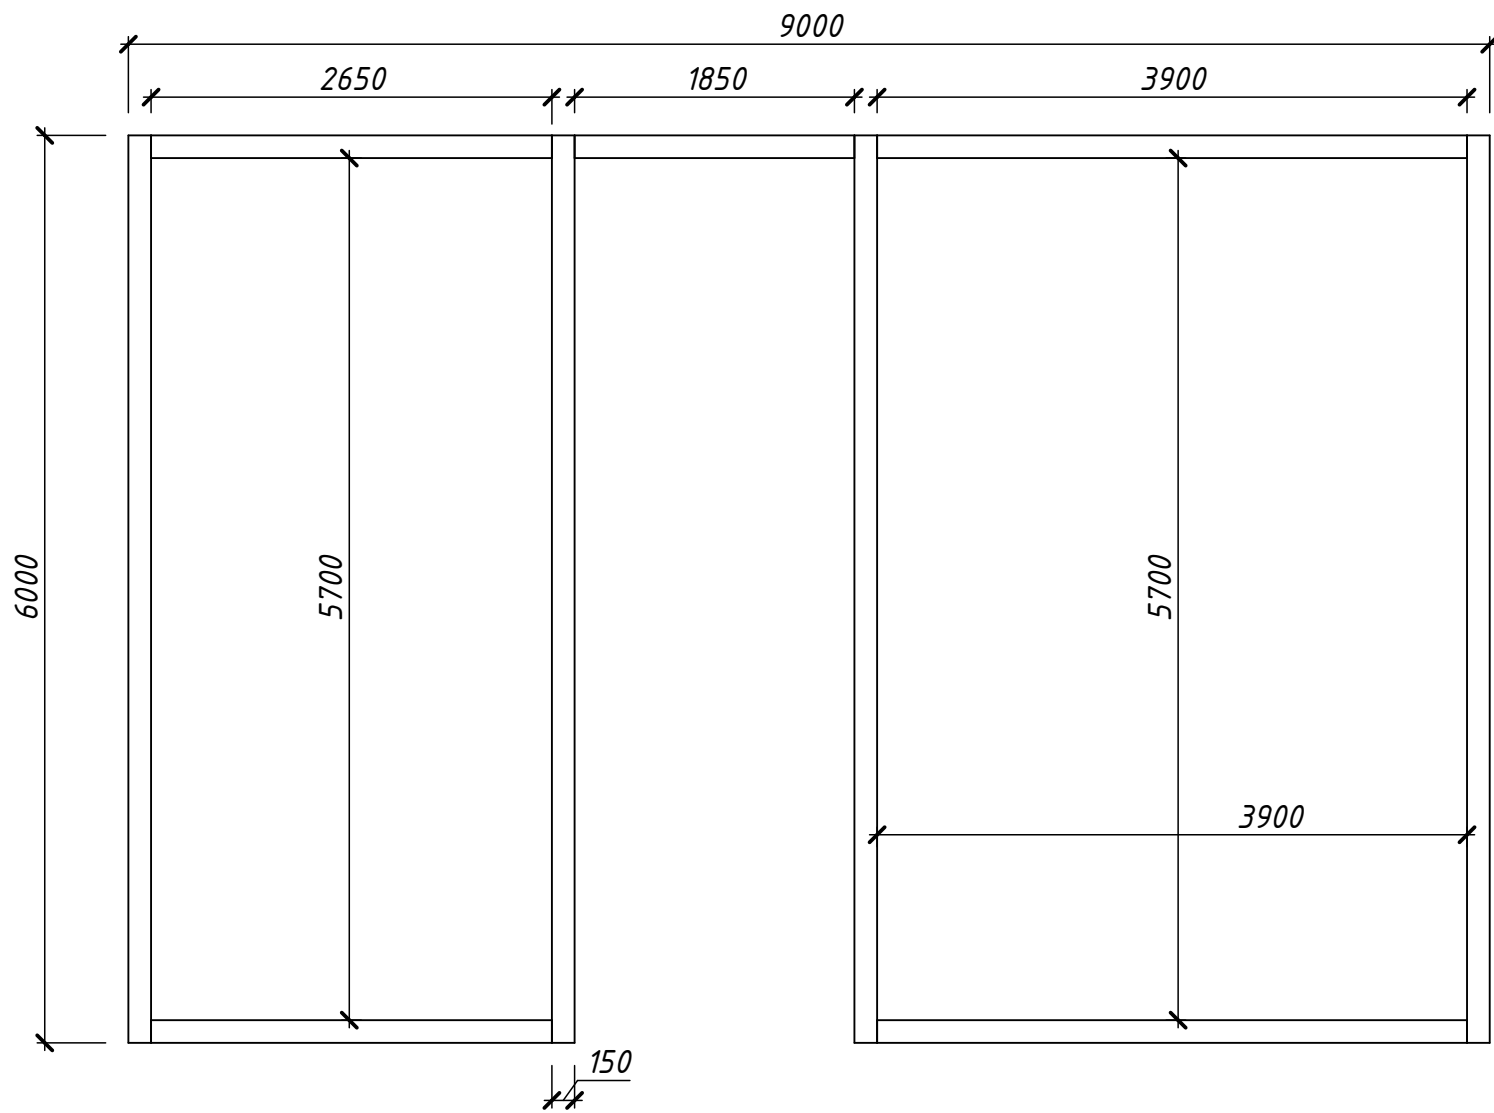

верхняя обвязка 3д

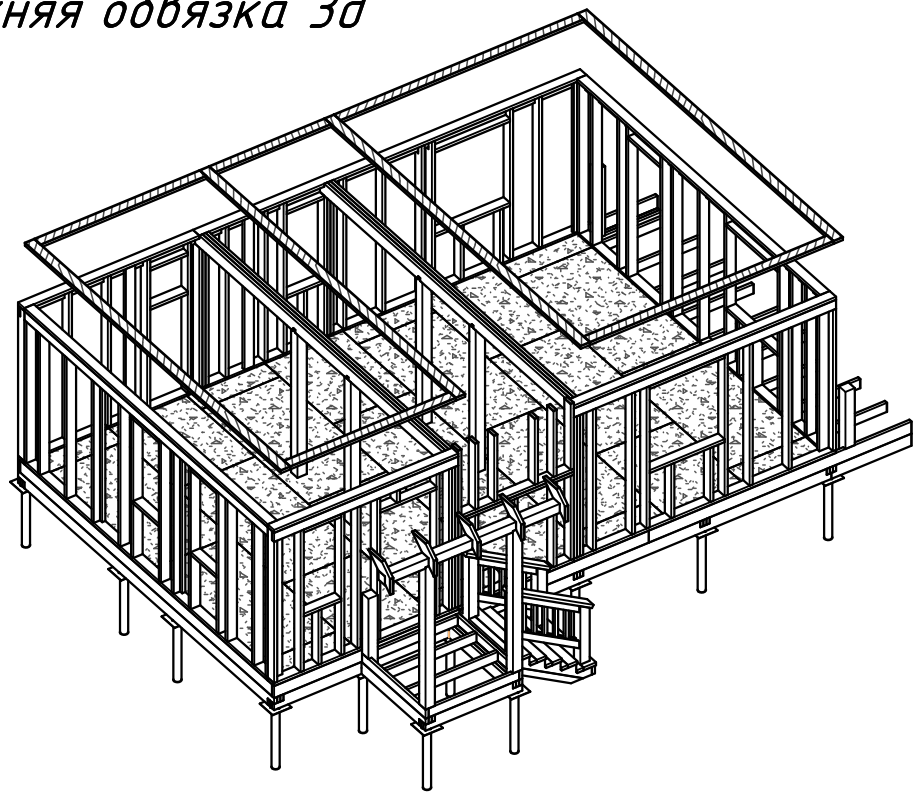

Раскрой. Верхняя обвязка			
Поз.	Наименование	Размер.мм	Колич. .шт
1	Лежень	6000х150х50	4
2	Лежень	3900х150х50	2
3	Лежень	2650х150х50	2
4	Лежень	1850х150х50	1

9

						№ проекта -		
						Россия, г. Кемерово		
Изм.	Кол.уч	Лист	№ док.	Подпись	Дата	Проект каркасного дома	Стадия	Лист
							КР	20
						Раскрой. Верхняя обвязка		