


Согласовано				

Инв. № подл.	Подп. и дата	Взам. инв. №

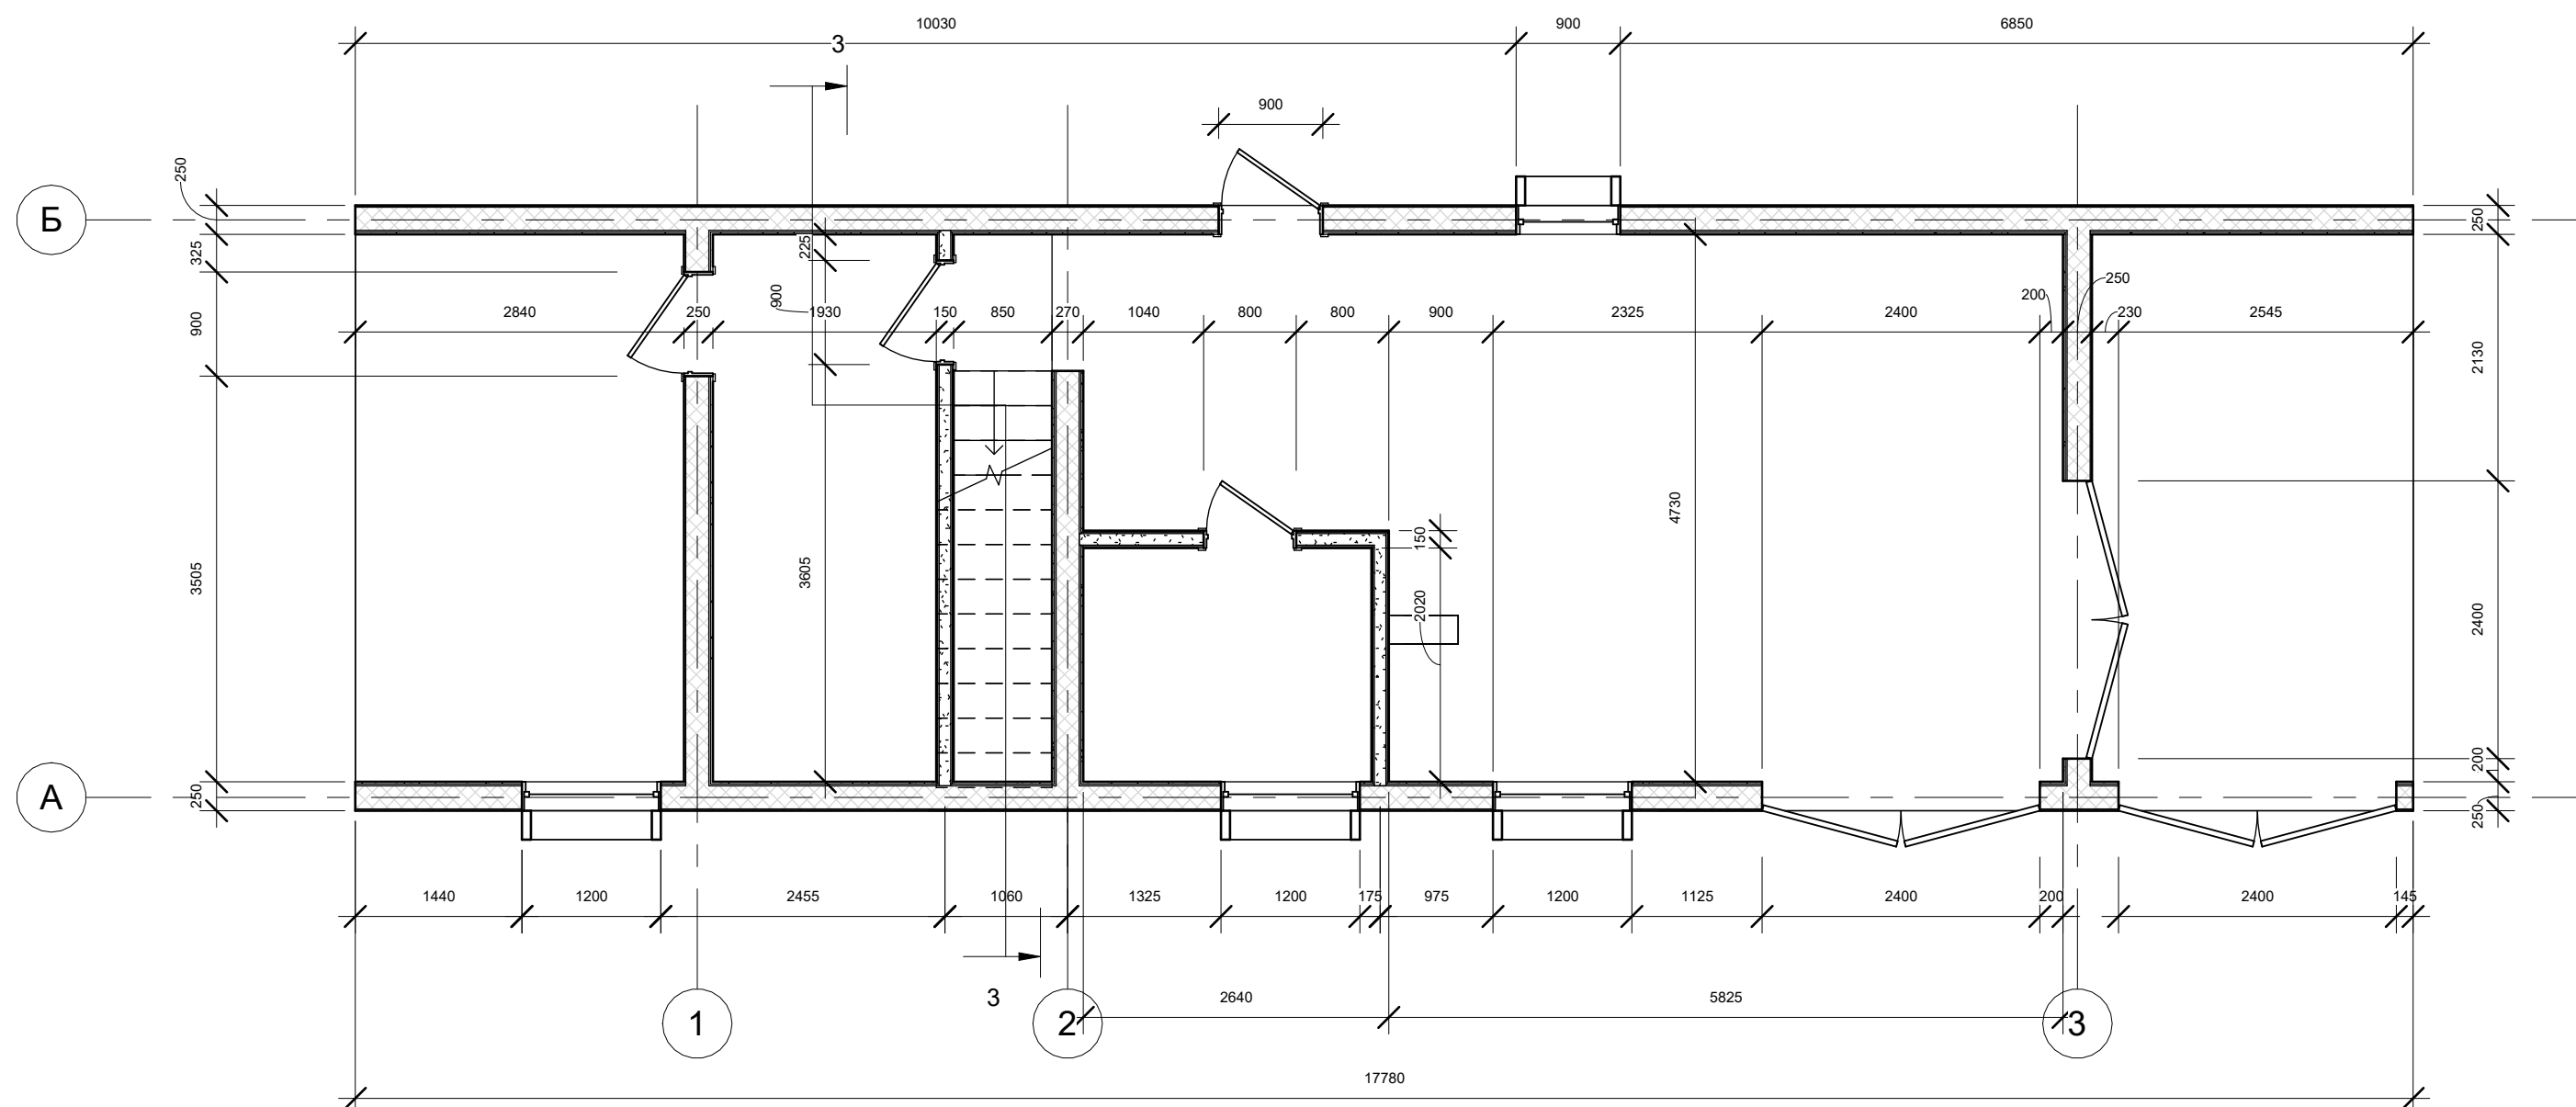

Изм.	Лист	№ док.	Подпись	Дата

0001 -

Лист
1

Согласовано

Взам. инв. №




Подп. и дата

Инв. № подл.

Условные обозначения

① -номер помещения

9,13 м² -площадь помещения

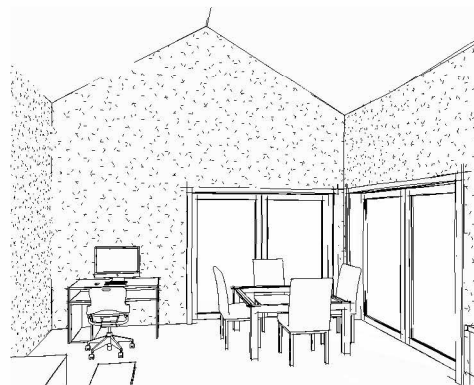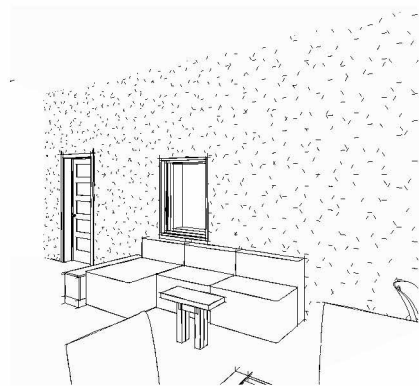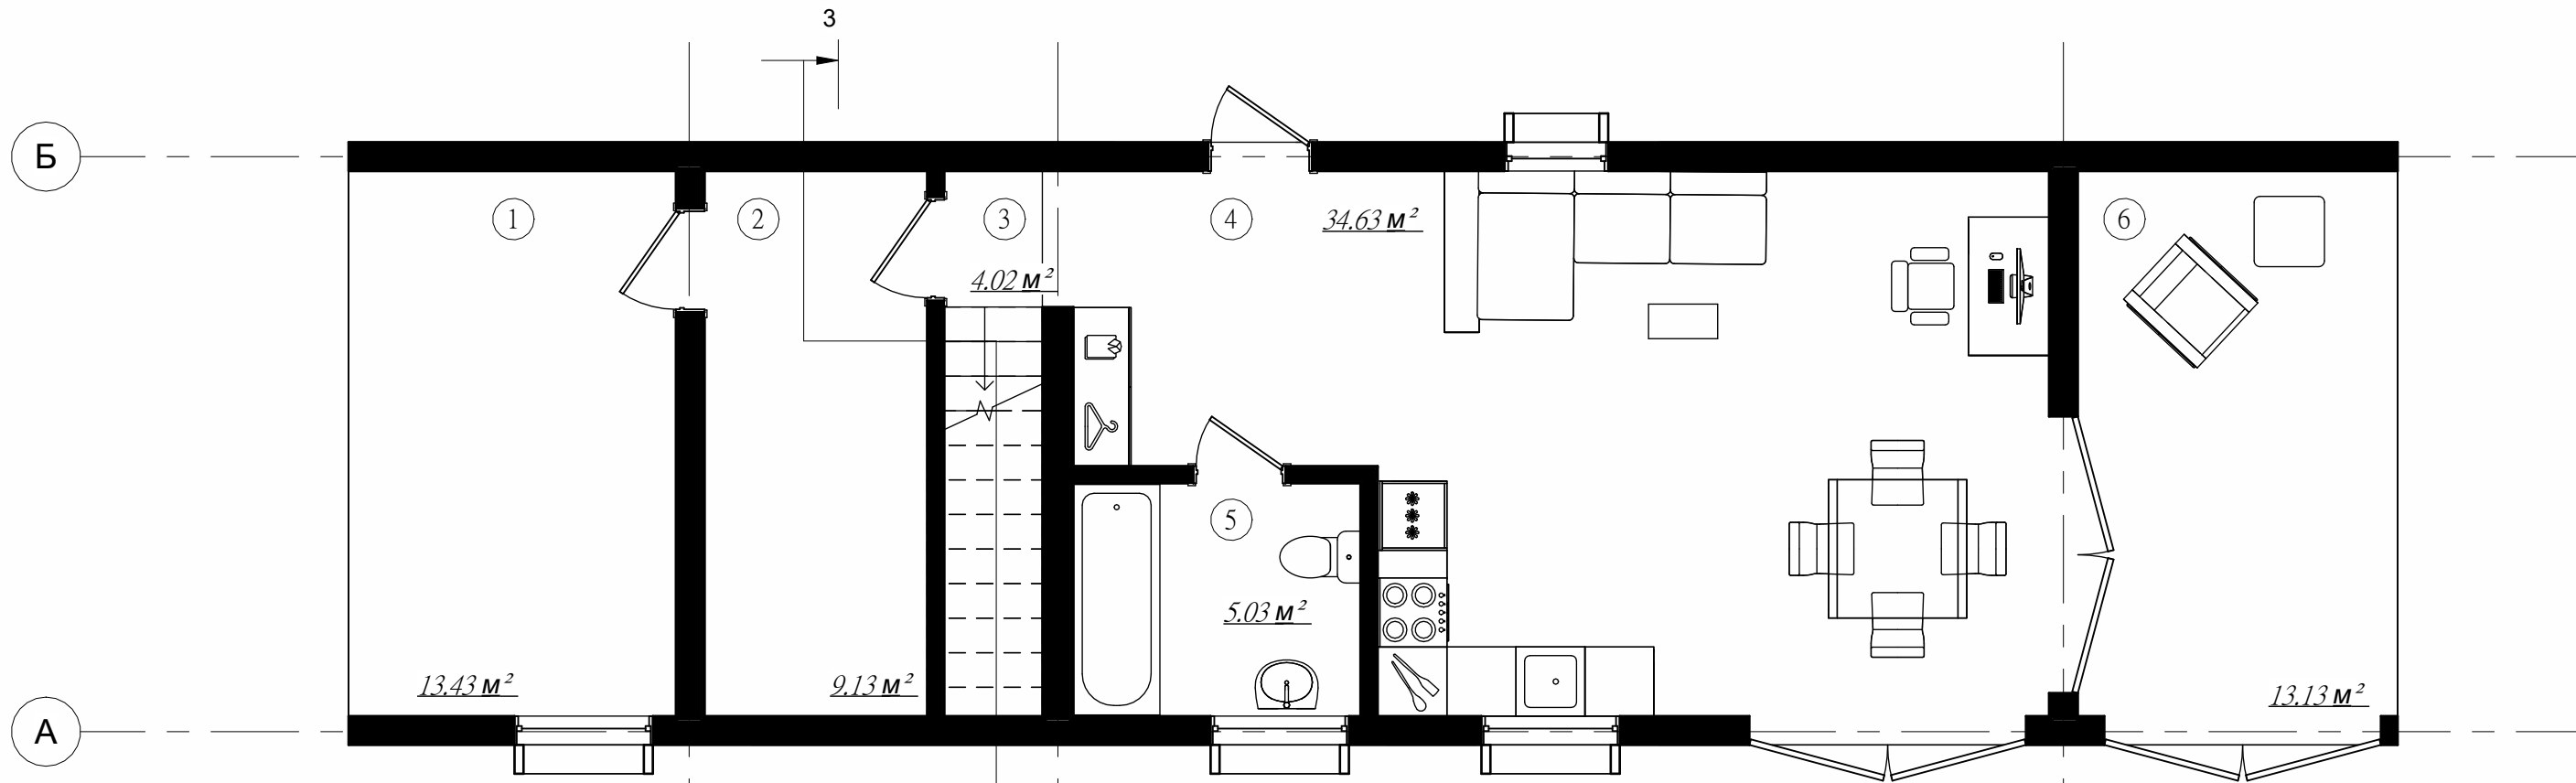


1.Экспликация помещений 1 эт			
№	Наимен.	Пл-дь	Прим.
1	терраса 1	13 м²	
2	Помещение	9 м²	
3	лестница	4 м²	
4	зал	35 м²	
5	уборная	5 м²	
6	терраса 2	13 м²	
Итого		79 м²	

Изм.	Лист	№ док.	Подпись	Дата

0001 -

Лист
2

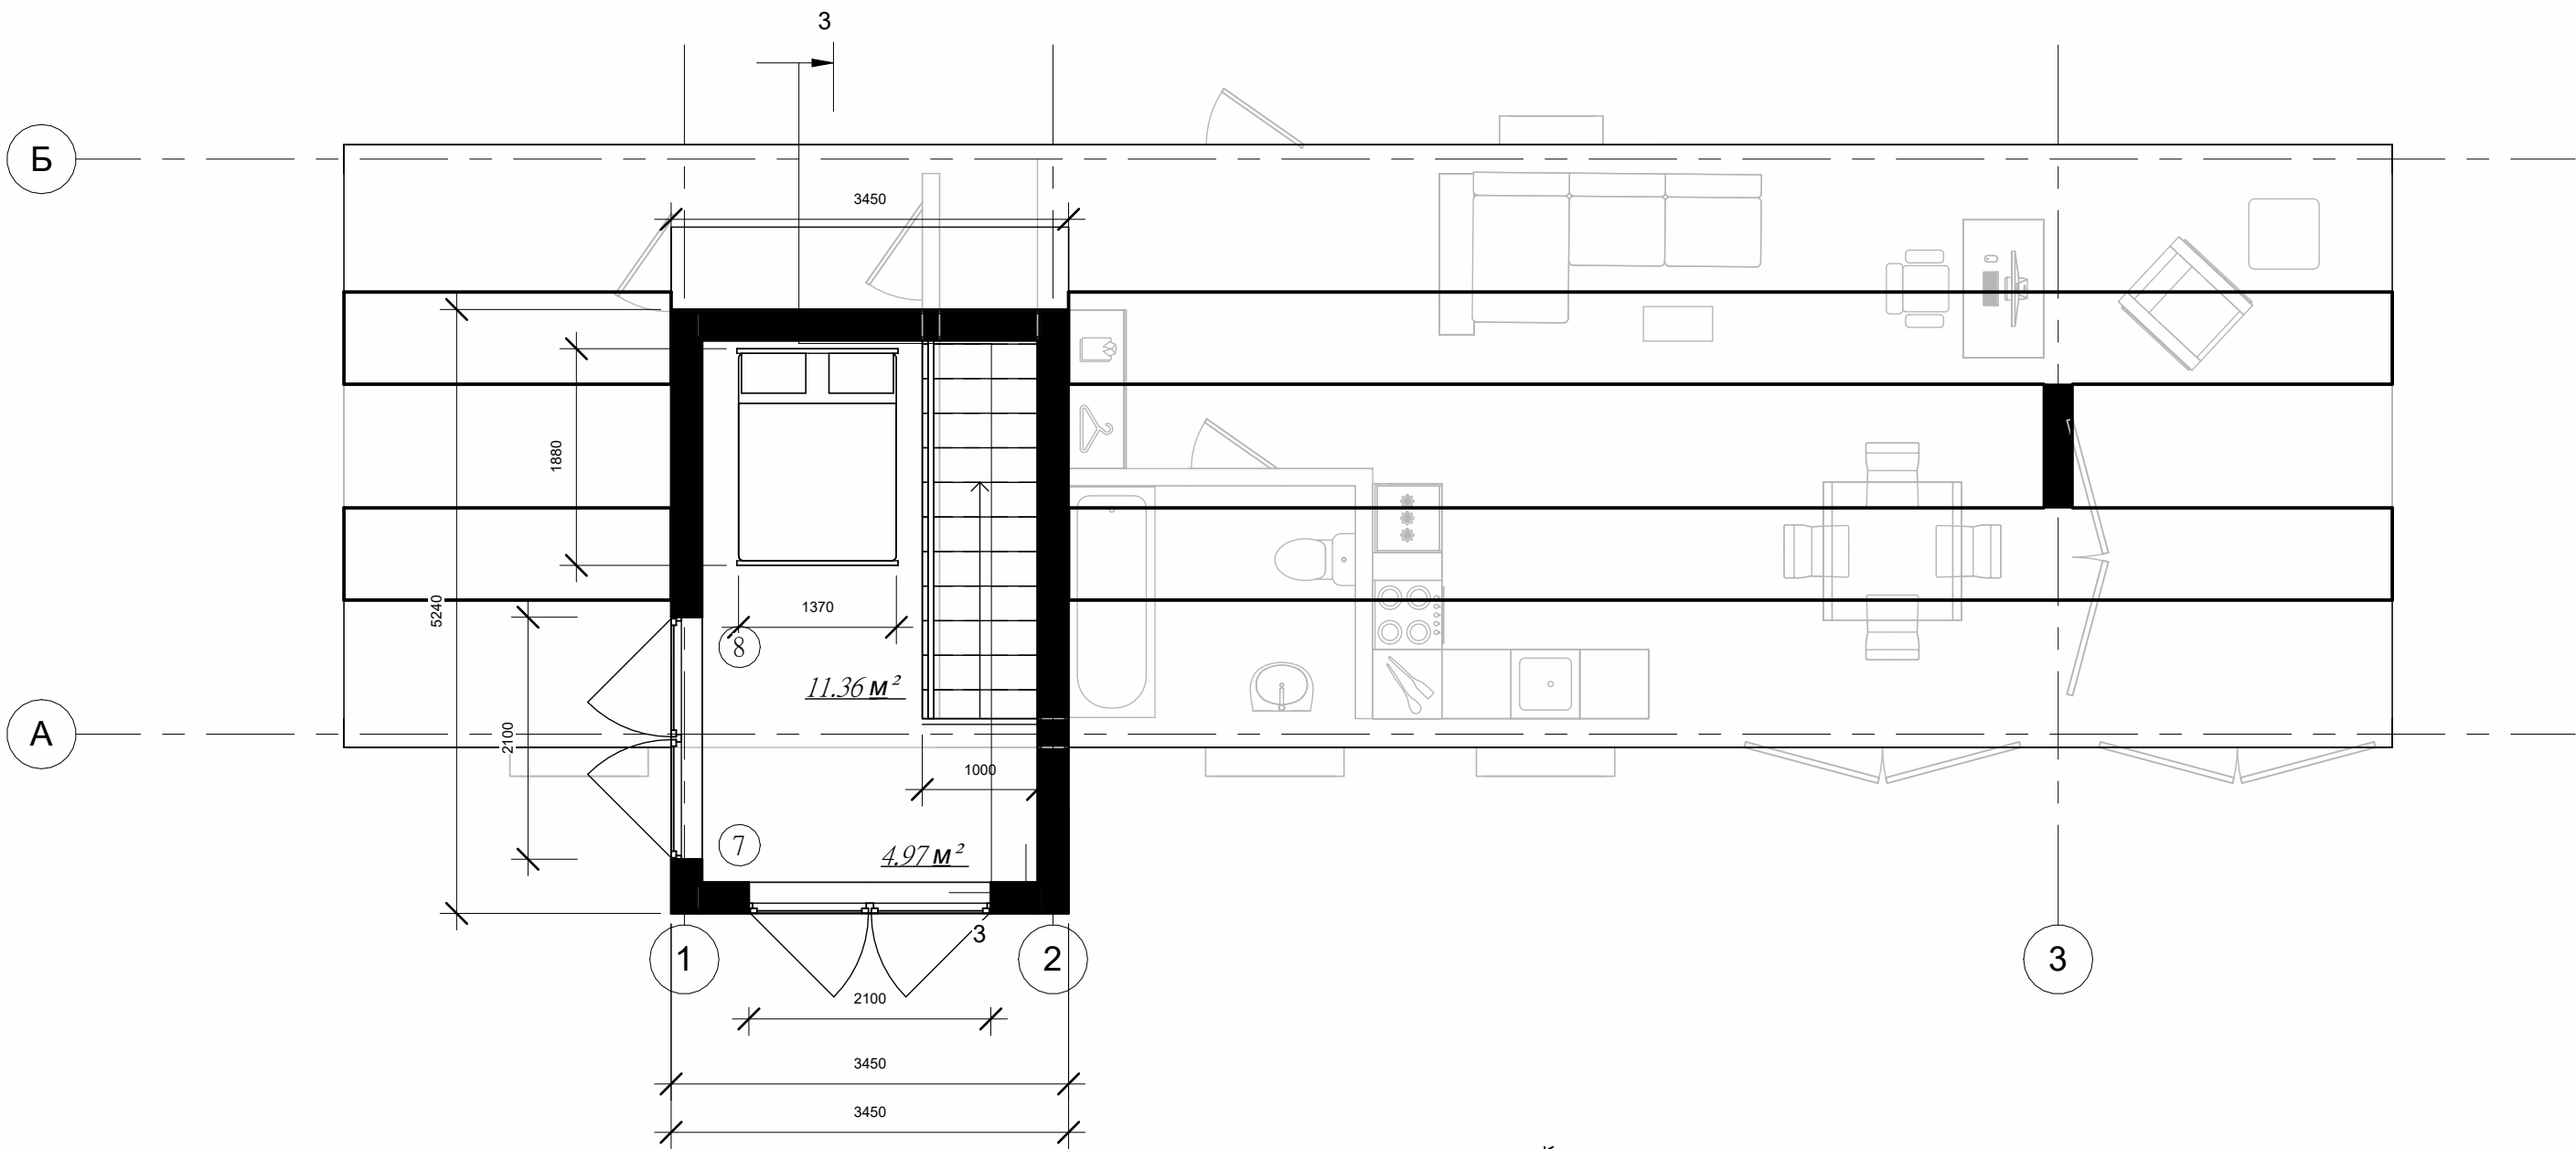


Экспликация помещений 2 эт

№	Наимен.	Пл-дь	Прим.
7	своб зона	5 м²	
8	спальное место	11 м²	
Итого		16 м²	

Спецификация оконных проемов 2эт

Марка	Описание	Высота	Ширина	Число	Примеч.
ОКЗ		800	2100	2	

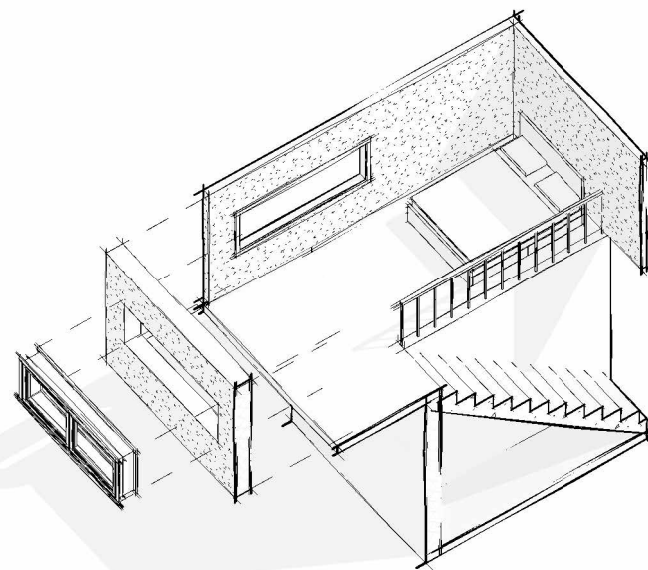






Спецификация оконных проемов 1эт					
Марка	Описание	Высота	Ширина	Число	Примеч.
Ок1		1200	900	1	
Ок2		1200	1200	3	
ОКЗ		800	2100	2	

Спецификация дверных проемов 1 эт.					
Марка	Описание	Высота	Ширина	Число	Примеч.
Д1		2100	750	1	
Д2		2075	850	3	
ДЗ		2100	2400	3	

Изм.	Лист	№ док.	Подпись	Дата

0001 -

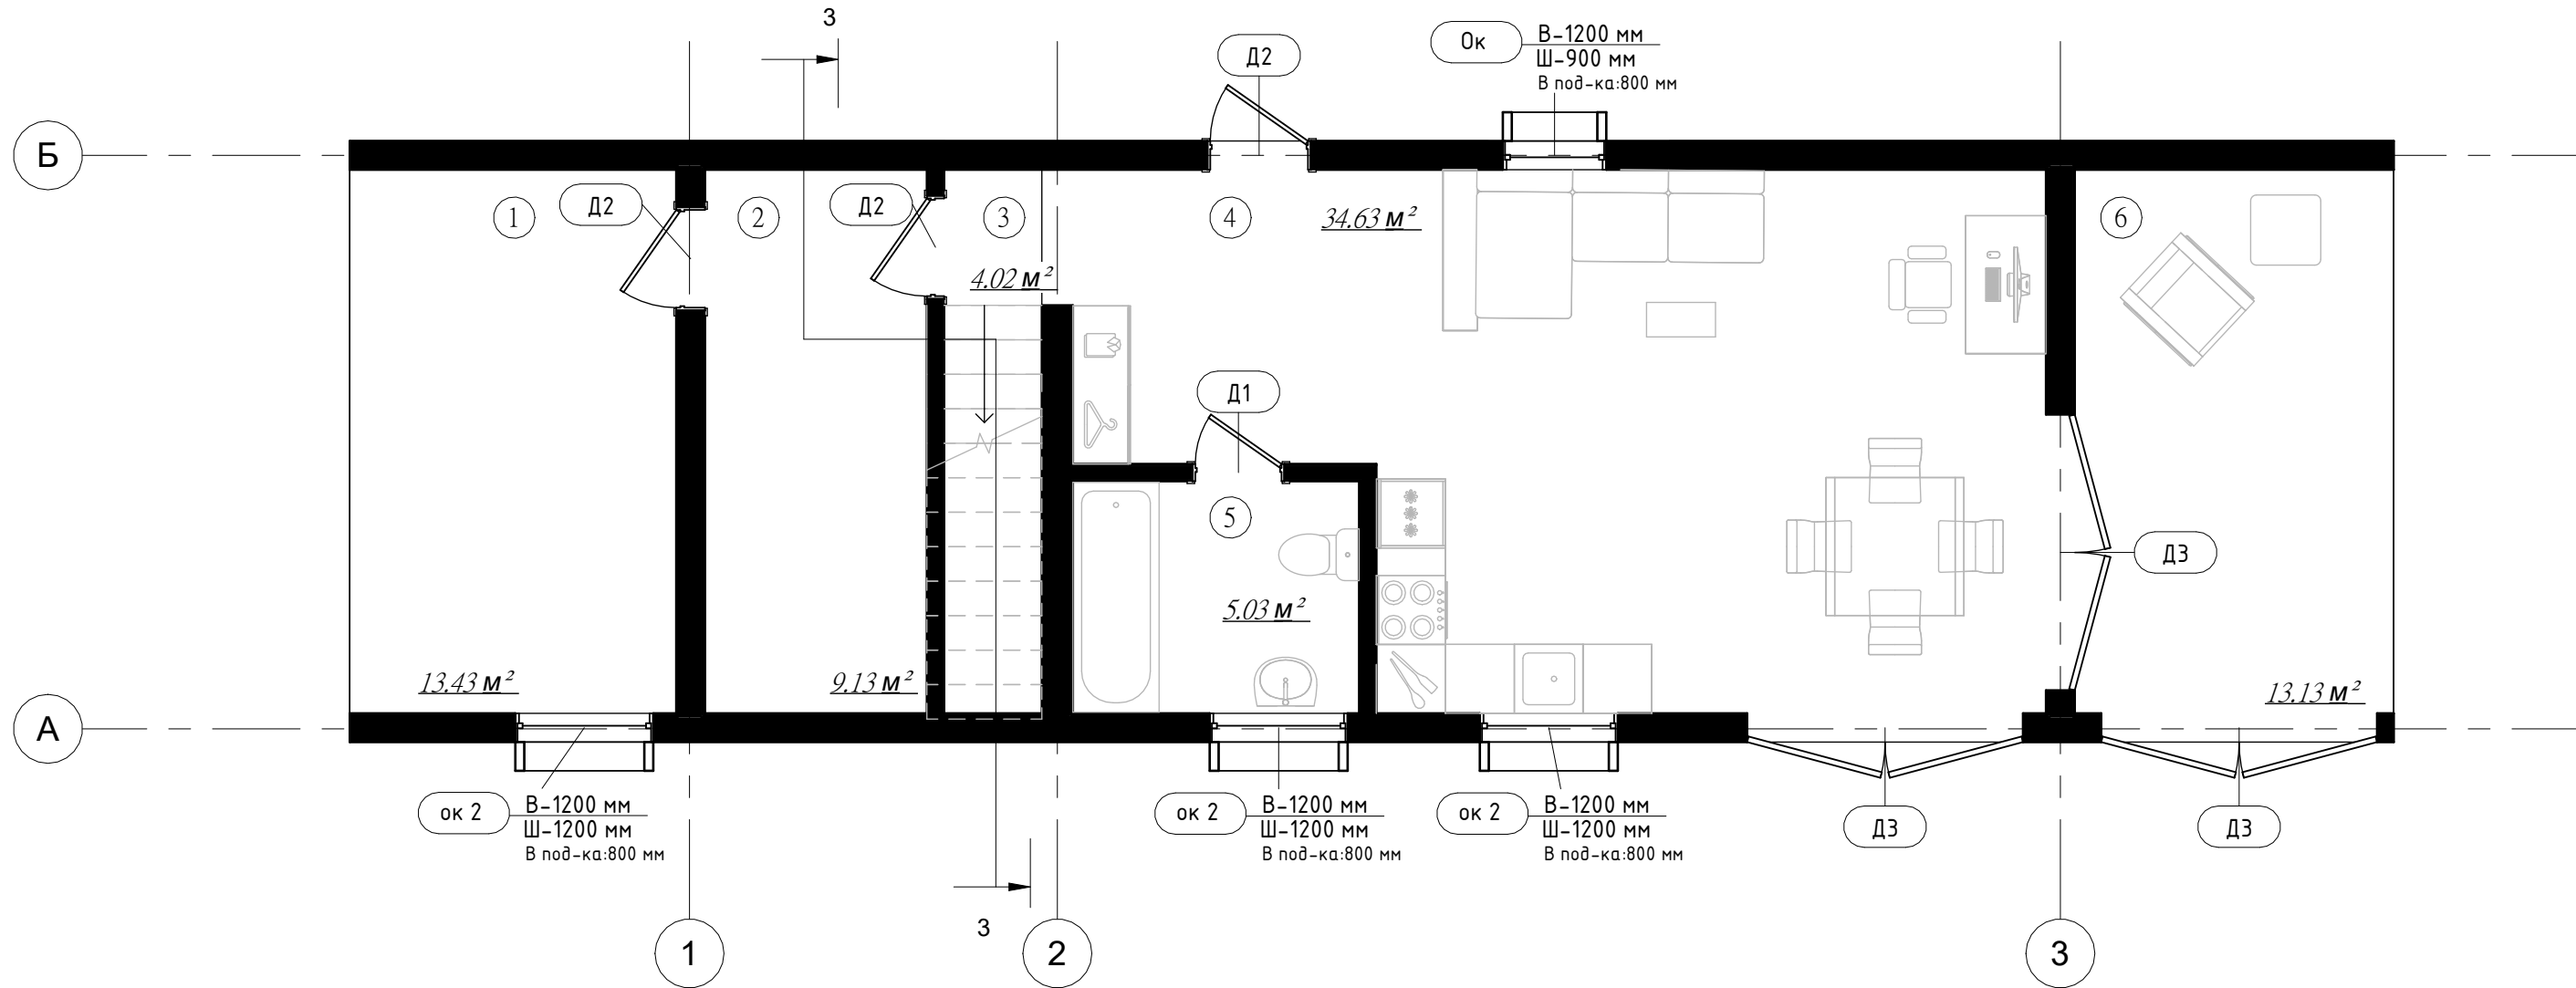

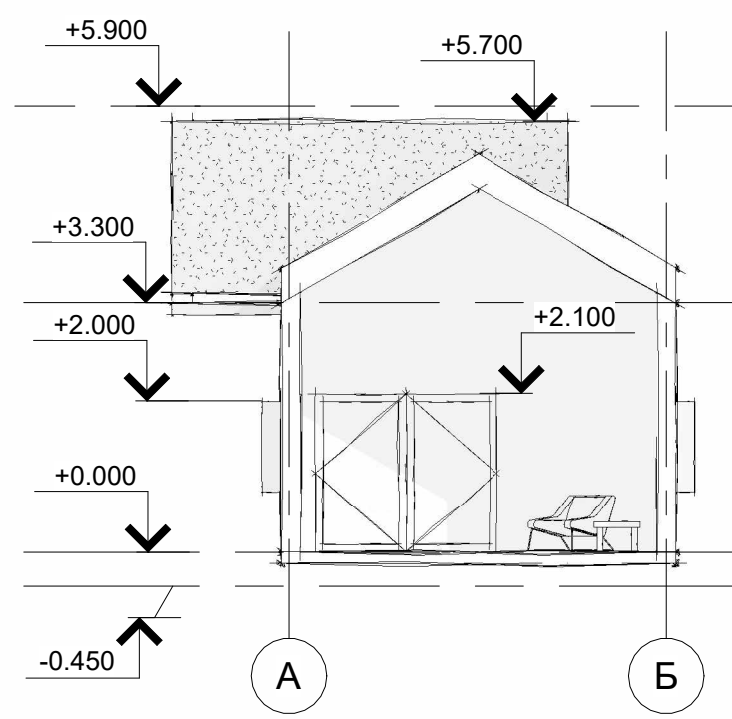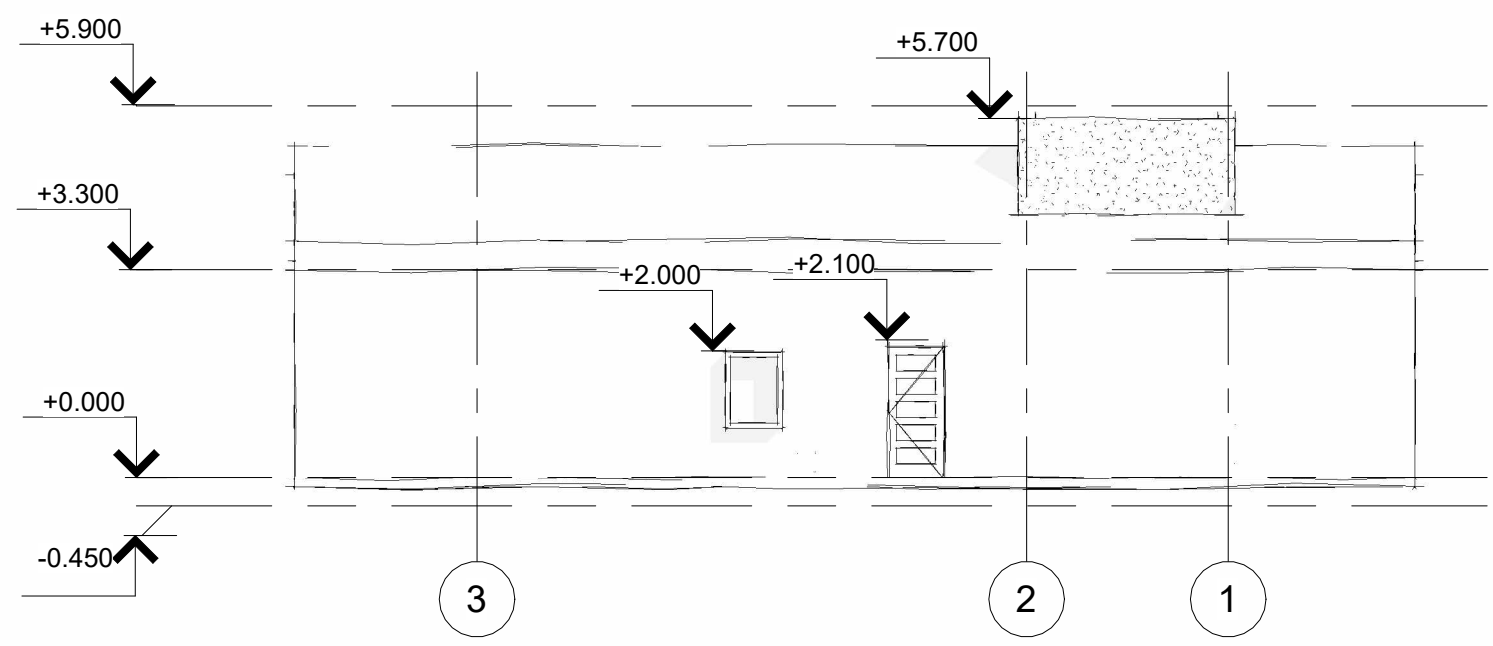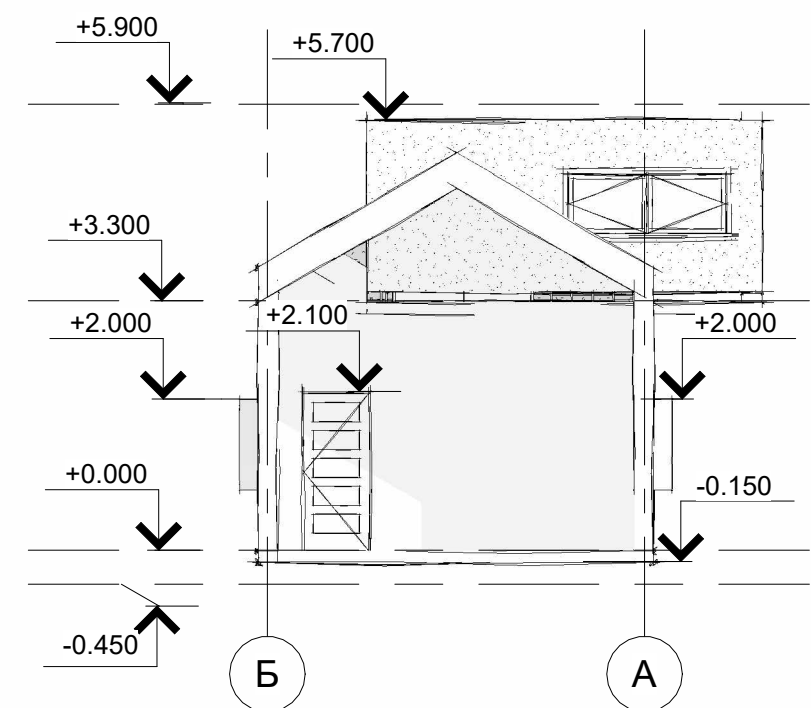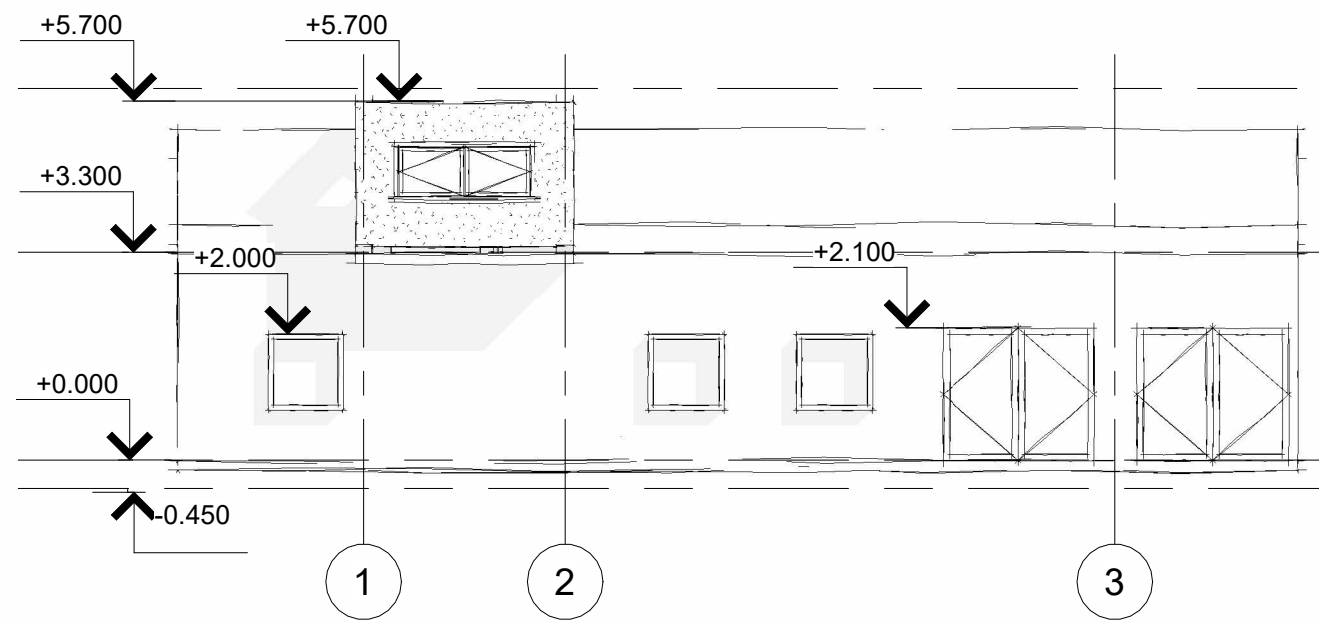

Согласовано		Взам. инв. №		Подп. и дата		Инв. № подл.	

Изм.	Лист	№ док.	Подпись	Дата


0001 -

Согласовано

Взам. инв. №


Подп. и дата

Инв. № подл.

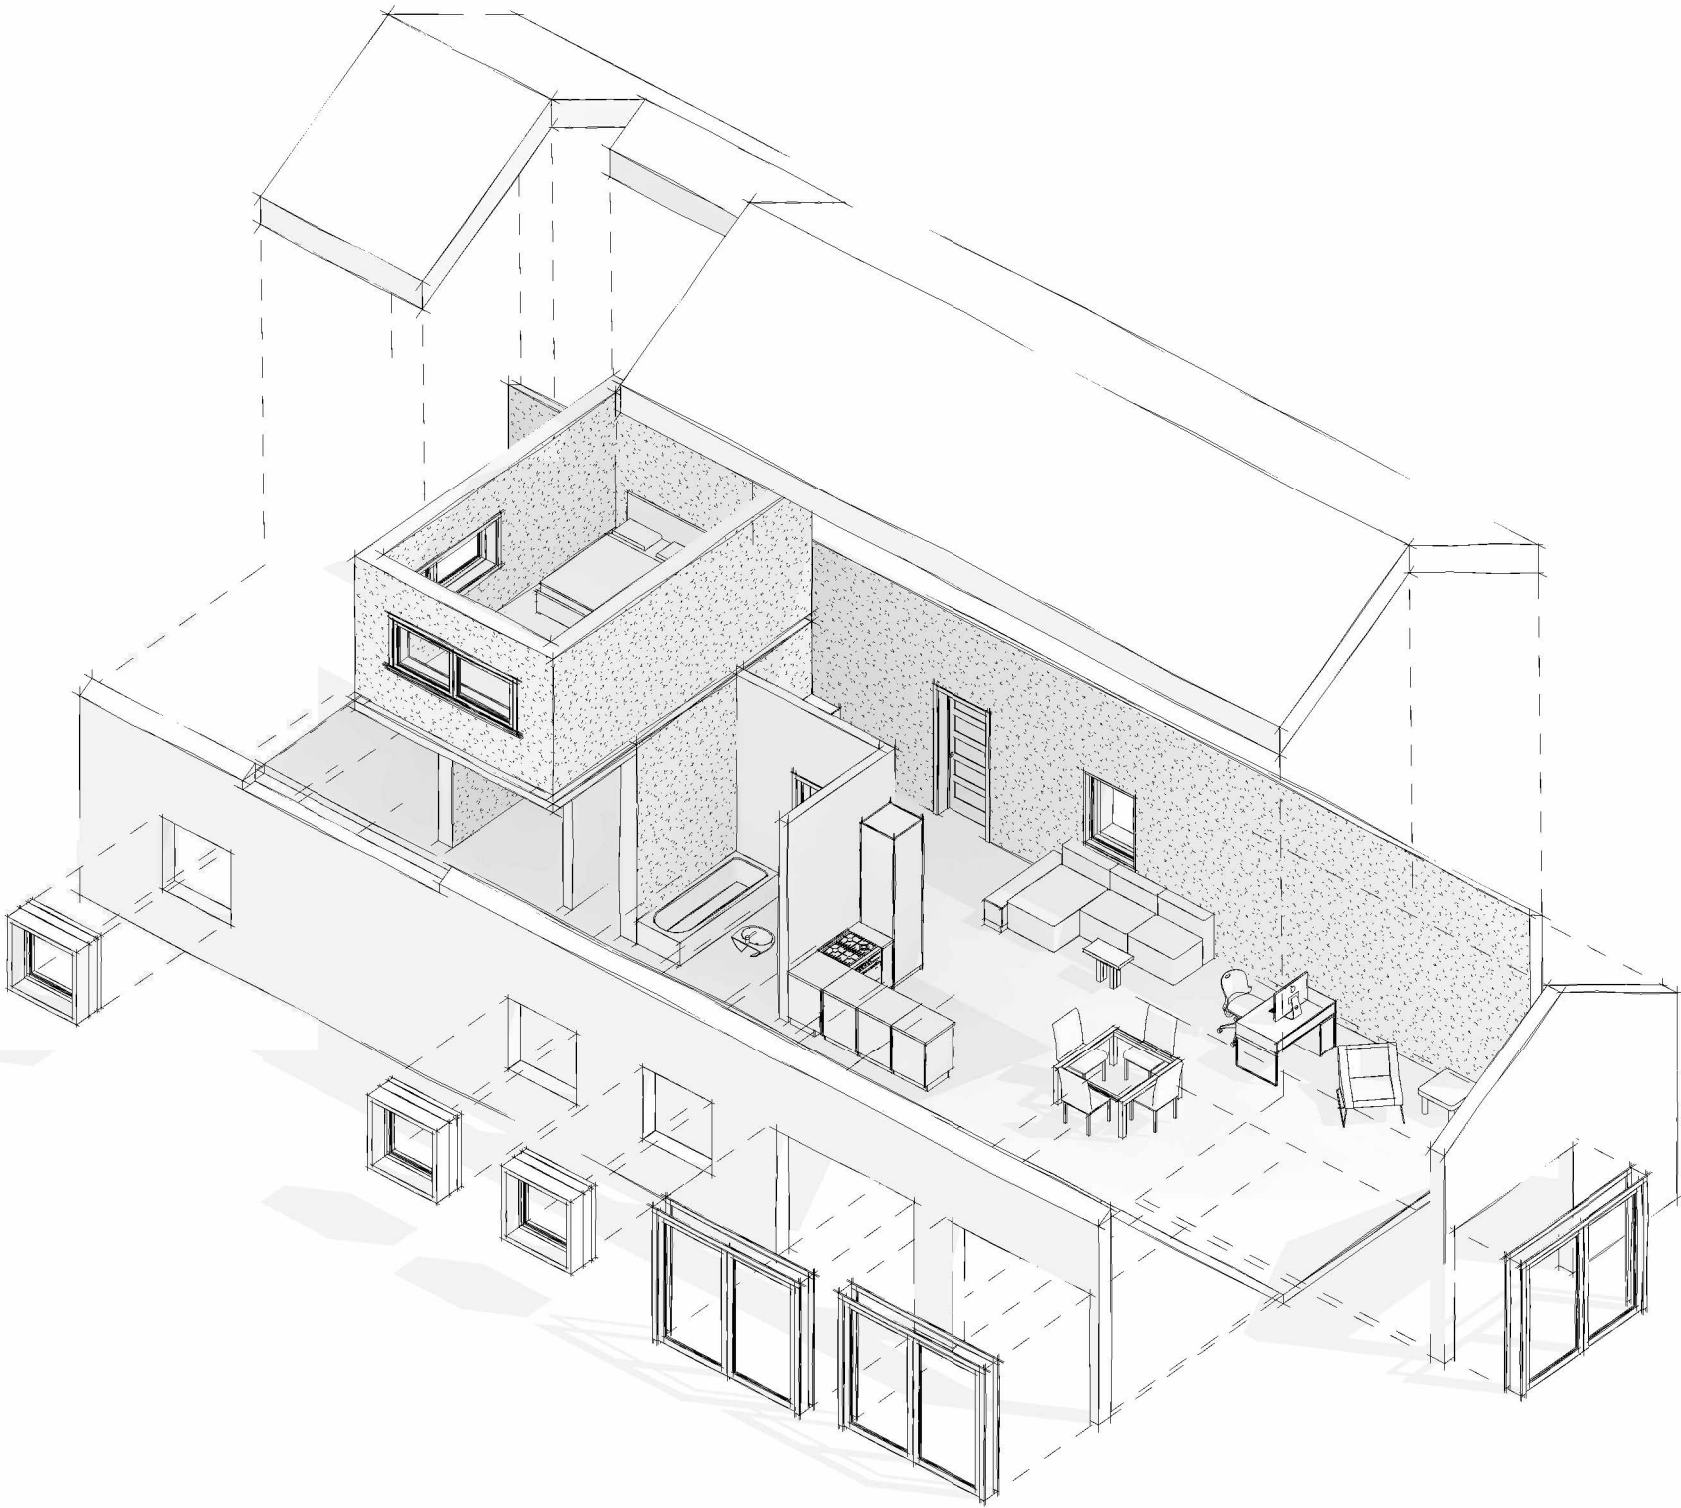


Ведомость материалов стен			
Материал: Имя	Материал: Площадь	Материал: Объем	Примеч.
1. Вагонка обшивка	351 м ²	5.26 м ³	
1. Деревянный каркас +изоляция	177 м ²	35.05 м ³	
2. Отделка штукатурка	223 м ²	4.46 м ³	
2. лист ГКЛ	110 м ²	1.37 м ³	
2.Гипсокартонная перегородка на металлическом каркасе	27 м ²	2.74 м ³	

Разрез 3Д вида
1:100

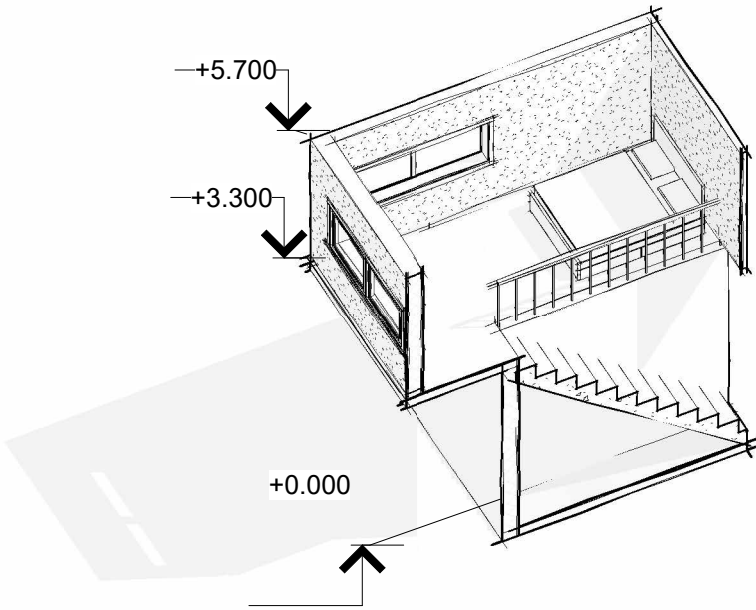

Сечение 3-3
1:100

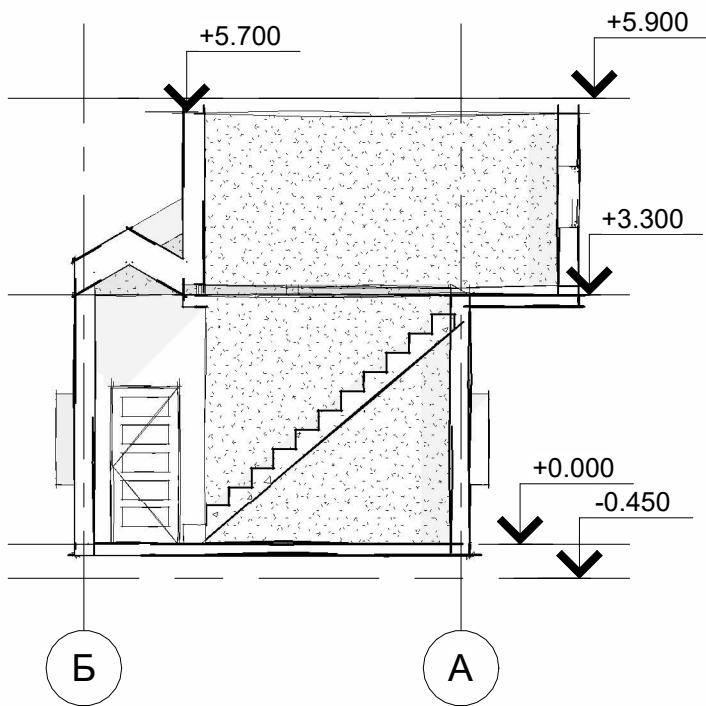

Изм.	Лист	№ док.	Подпись	Дата

0001 -