


План 1-го этажа

Экспликация помещений 1-го этажа

Номер пом.	Наименование	Площадь, м2
1	Входная группа	7.76
2	Прихожая	10.13
3	С/У	6.05
4	Гостинная	37.73
5	Кухня	18.50
6	Гараж	20.66
7	Складское помещение	9.12
8	Терраса	36.95
Итого		146.91

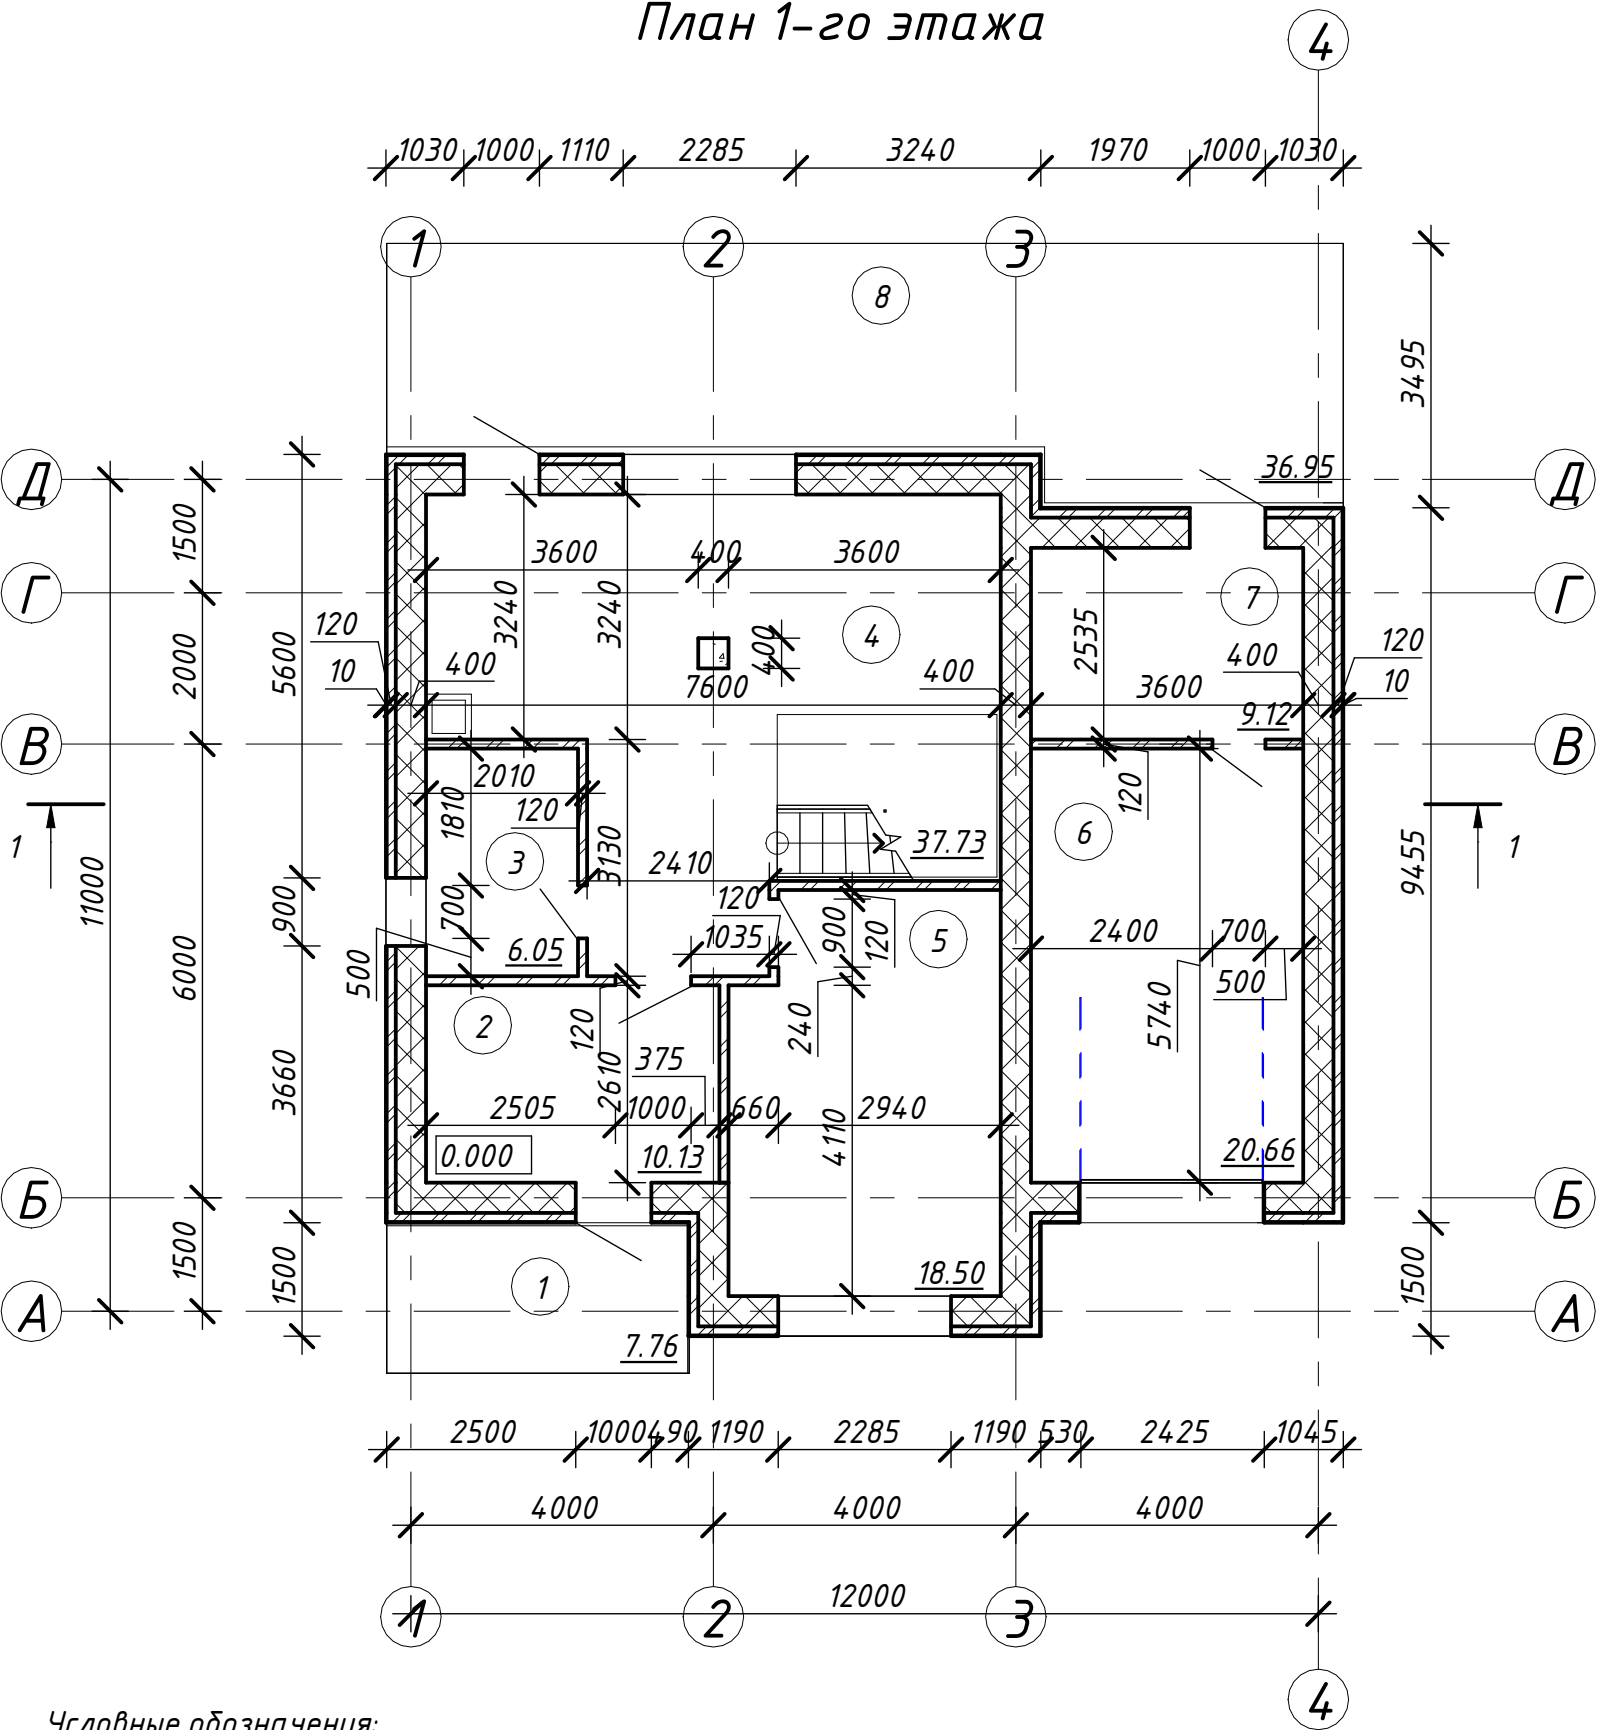


Условные обозначения:

- наружная стена из газобетона , 400 мм с облицовкой из кирпича 120 мм и штукатуркой 10 мм
- внутренняя стена из газобетона, 400 мм
- перегородка , 120 мм

						01-АР		
Изм.	Кол.	Лист	№	Подпись	Дата			
						Стадия	Лист	Листов
						У	1	
Разработал								
Проверил								

План 2-го этажа

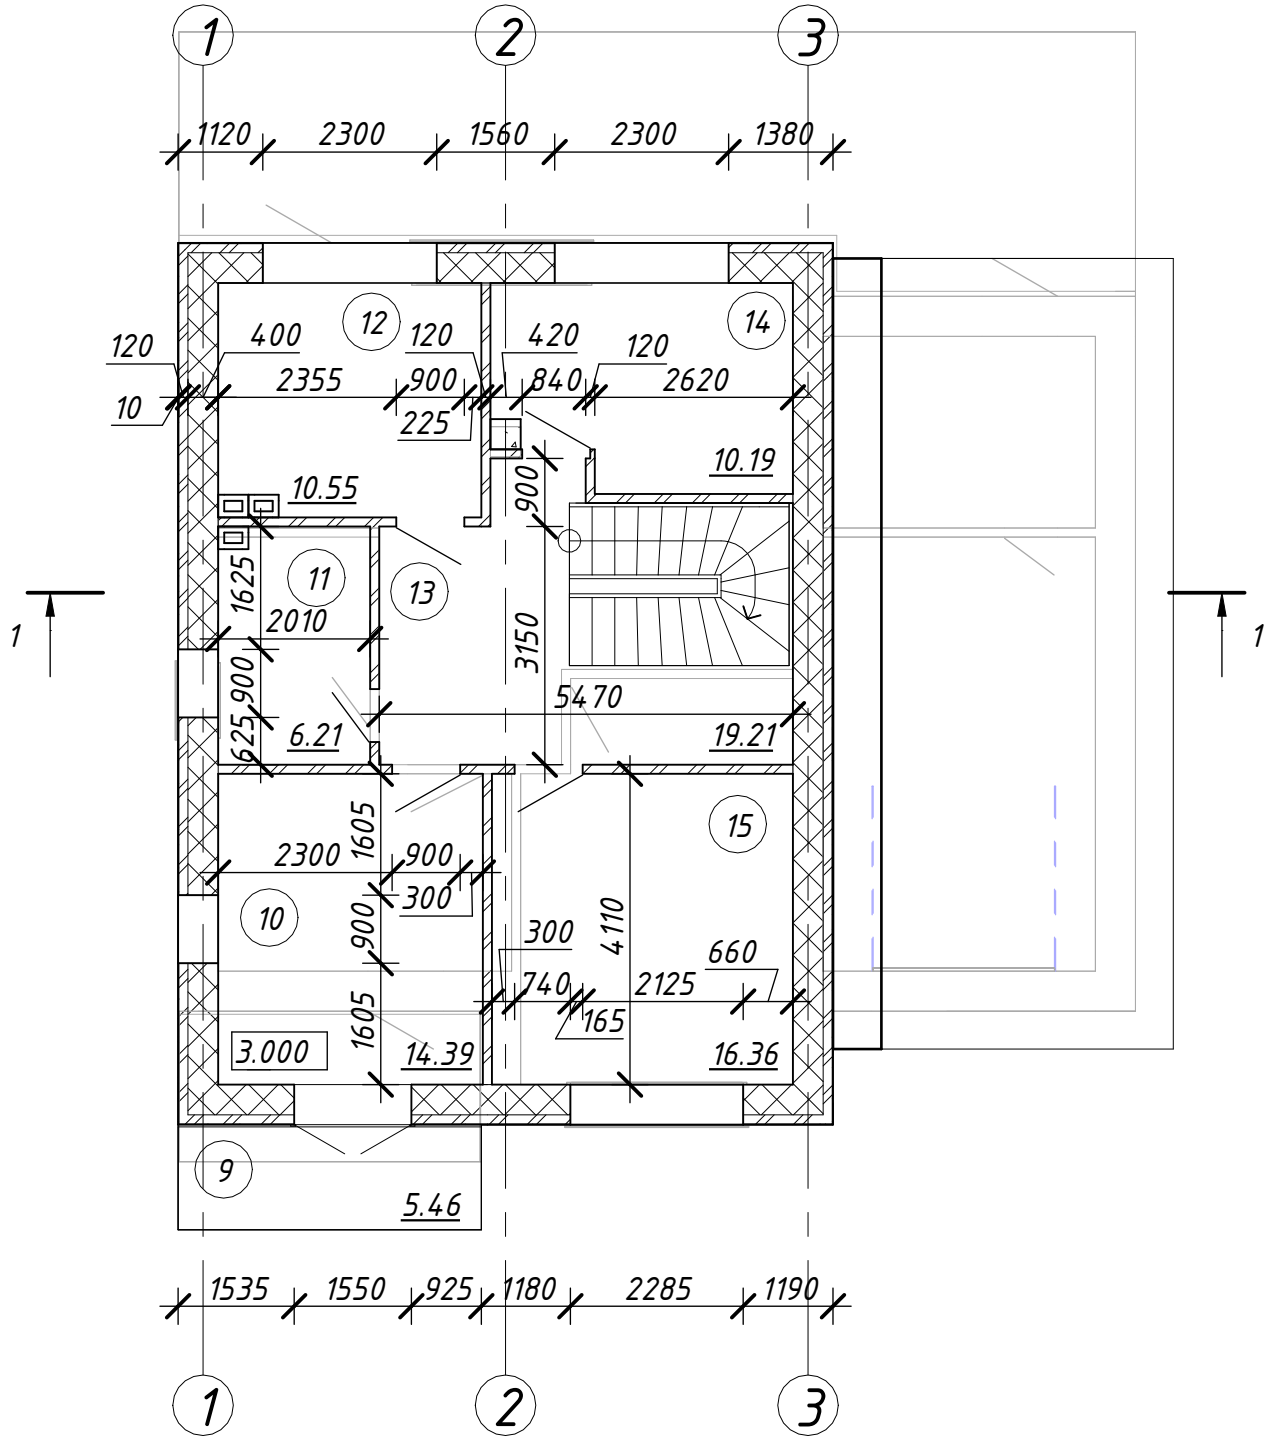

Экспликация 2-го этажа





Номер пом.	Наименование	Площадь, м2
9	Балкон	5.46
10	Спальня_1	14.39
11	С/У_2	6.21
12	Спальня_3	10.55
13	Холл	19.21
14	Спальня_4	10.19
15	Спальня_2	16.36
Итого		82.36

Условные обозначения:

-
- наружная стена из газобетона , 400 мм с облицовкой из кирпича 120 мм и штукатуркой 10 мм
-
- внутренняя стена из газобетона, 400 мм
-
- перегородка , 120 мм

						01-АР			
Изм.	Кол.	Лист	№	Подпись	Дата		Стадия	Лист	Листов
							У	2	
Разработал									
Проверил									

Согласовано					
	Взам. инв. №				
	Подп. и дата				
	Инв. № подл.				

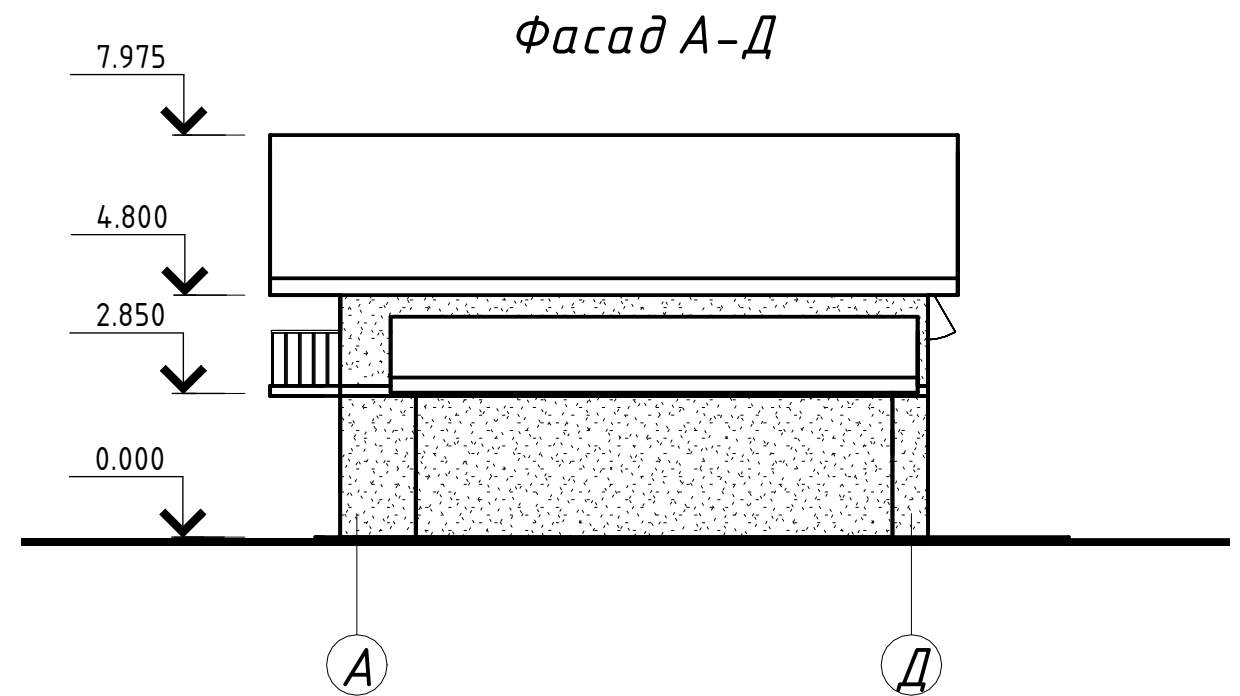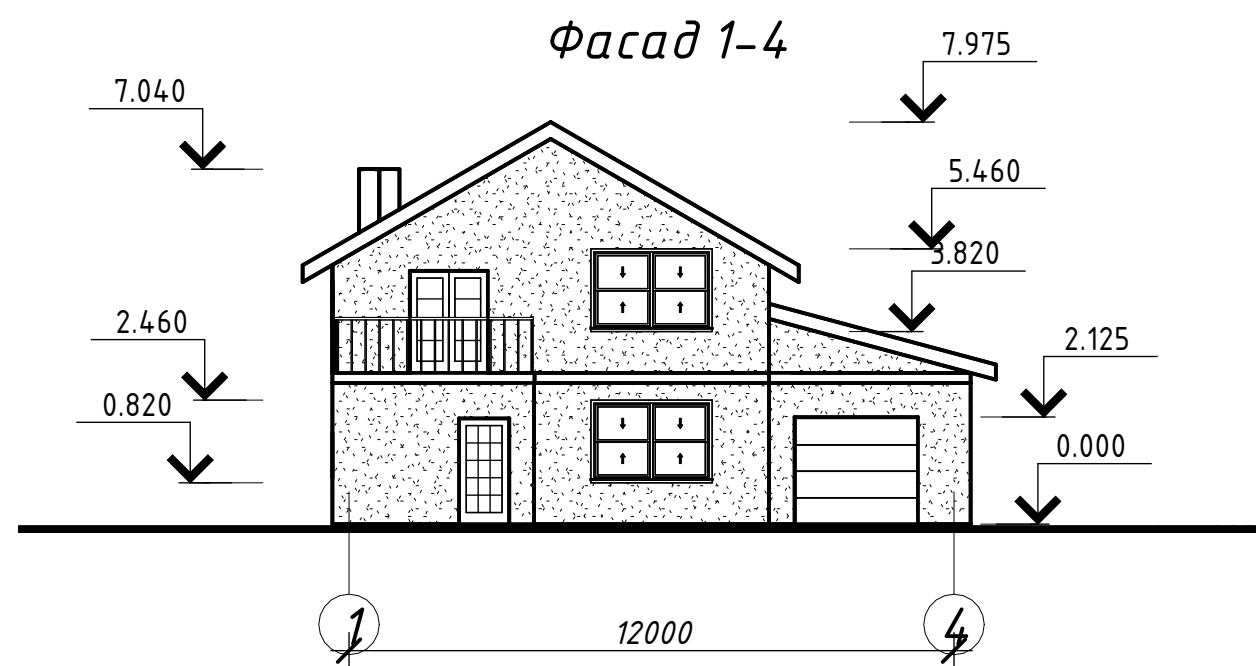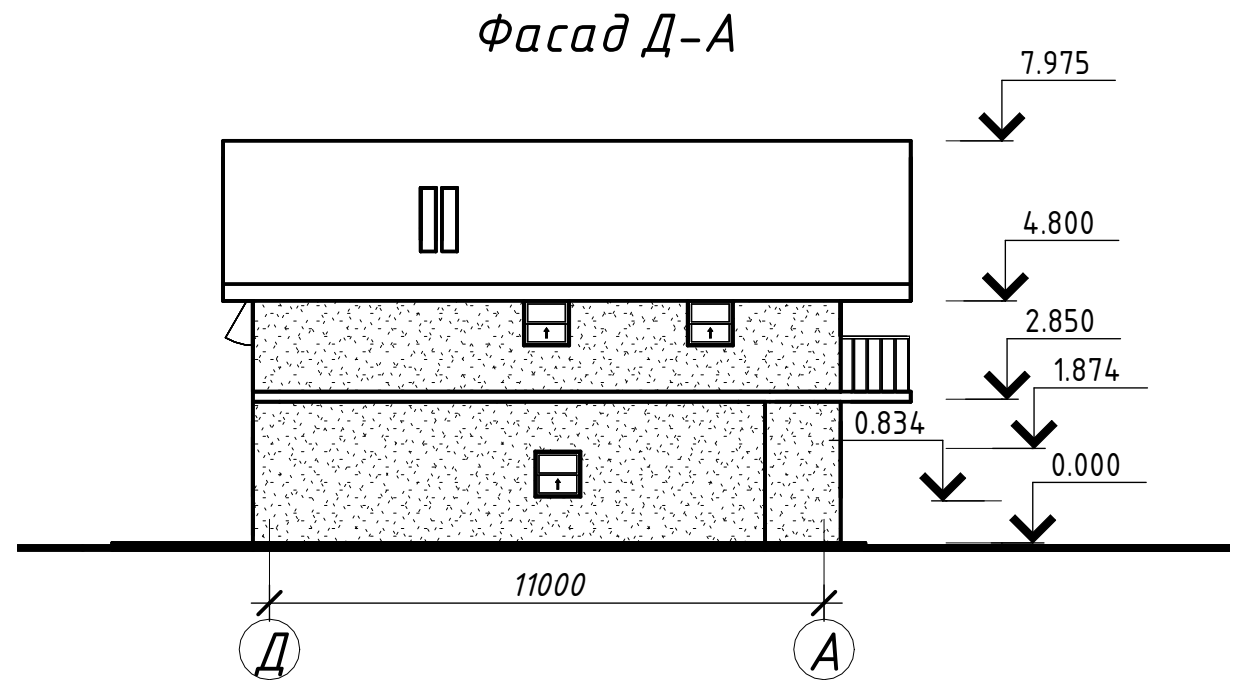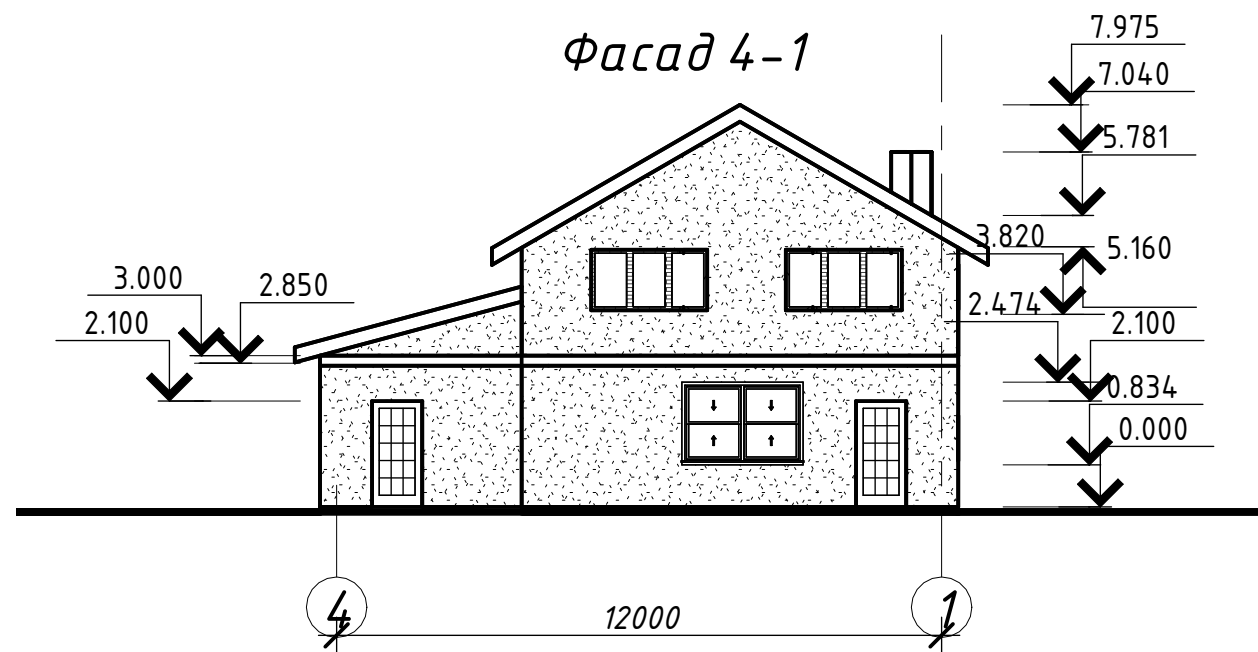


Условные обозначения:



						01-AP		
Изм.	Кол.	Лист	№	Подпись	Дата			
						Стадия	Лист	Листов
						У	З	
Разработал								
Проверил								

Разрез 1-1

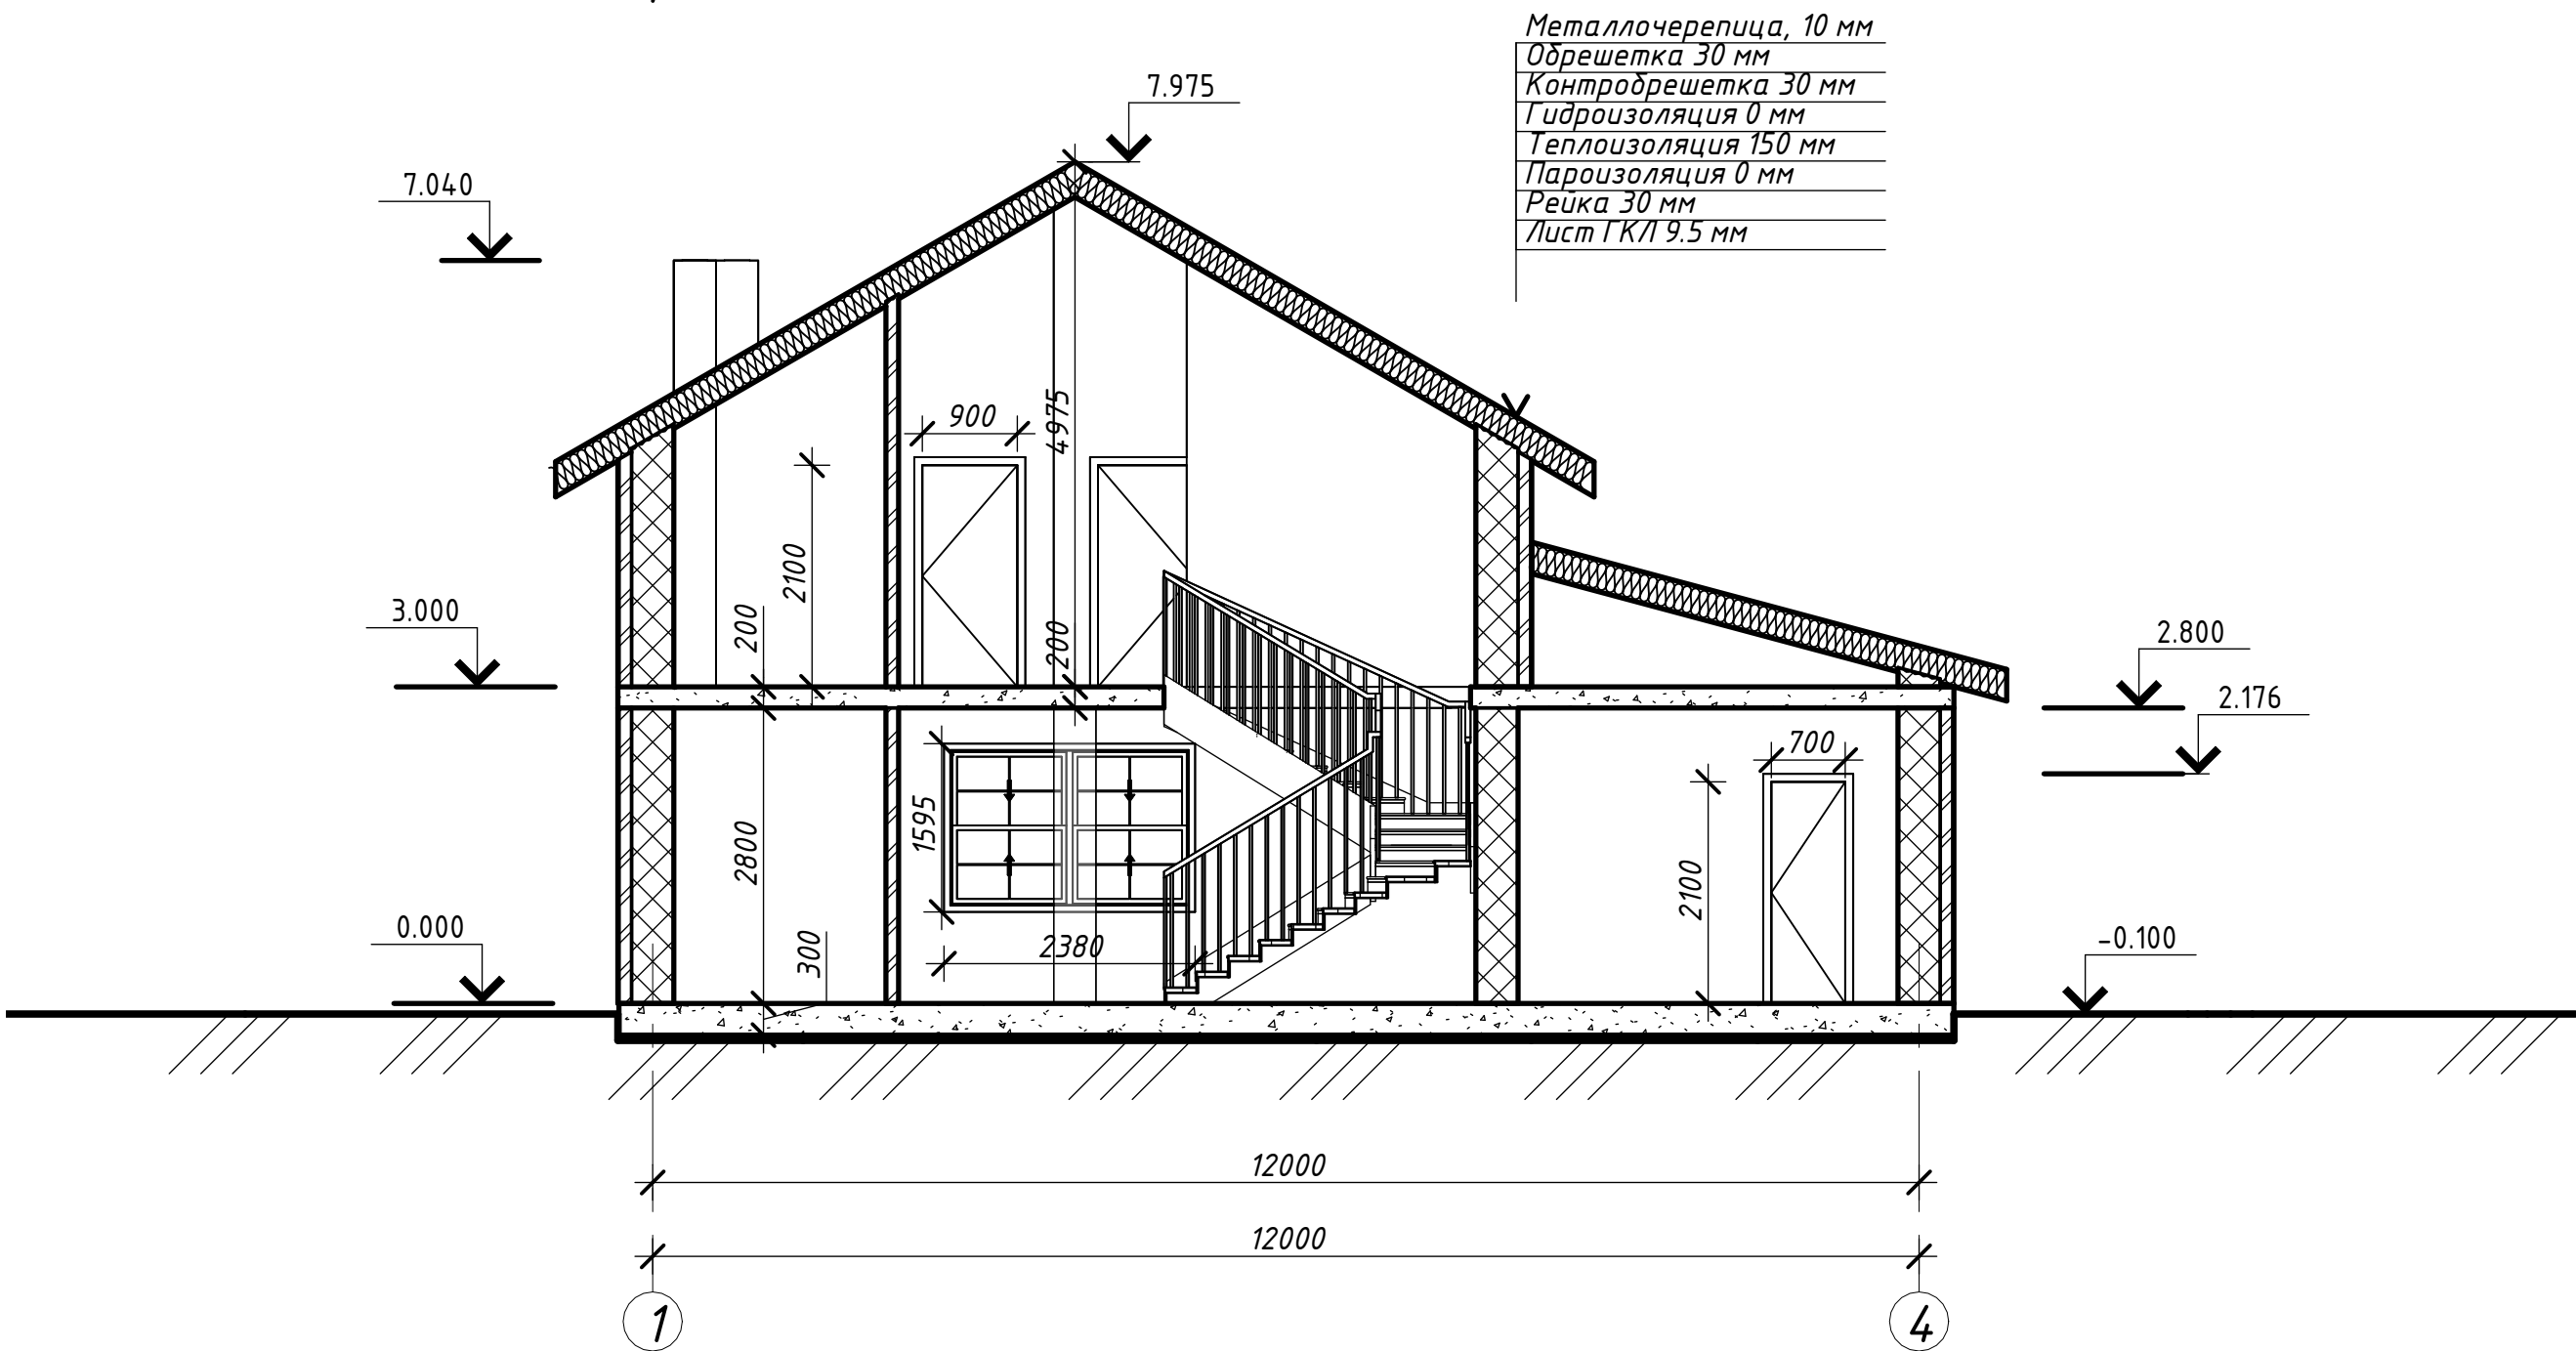

Согласовано					
Взам. инв. №					
Подп. и дата					
Инв. № подл.					

						01-AP			
Изм.	Кол.	Лист	№	Подпись	Дата				
							Стадия	Лист	Листов
							У	4	
Разработал									
Проверил									

Согласовано			Взам. инв. №		Подп. и дата		Инв. № подл.	



						01-AP			
Изм.	Кол.	Лист	№	Подпись	Дата				
							Стадия	Лист	Листов
							У	5	
Разработал									
Проверил									